



סביבת התחנה: מיפוי אגן היקוות התחנה

תחנה מס' 36 | שדרות הציונות

רדיוס שירות

תוואי מטר

תחנת מטר

עוגן ציבורי ברדיוס 800m

עוגן מסחרי ברדיוס 800m

מתחם ציבורי פתוח/גן/פארק

ציר עירוני ראשי - וקטור ביקוש


ציר עירוני - וקטור ביקוש

שביל אופניים קיים

שביל אופניים מתוכנן

ציר הולכי רגל ראשי

ציר הולכי רגל מתוכנן

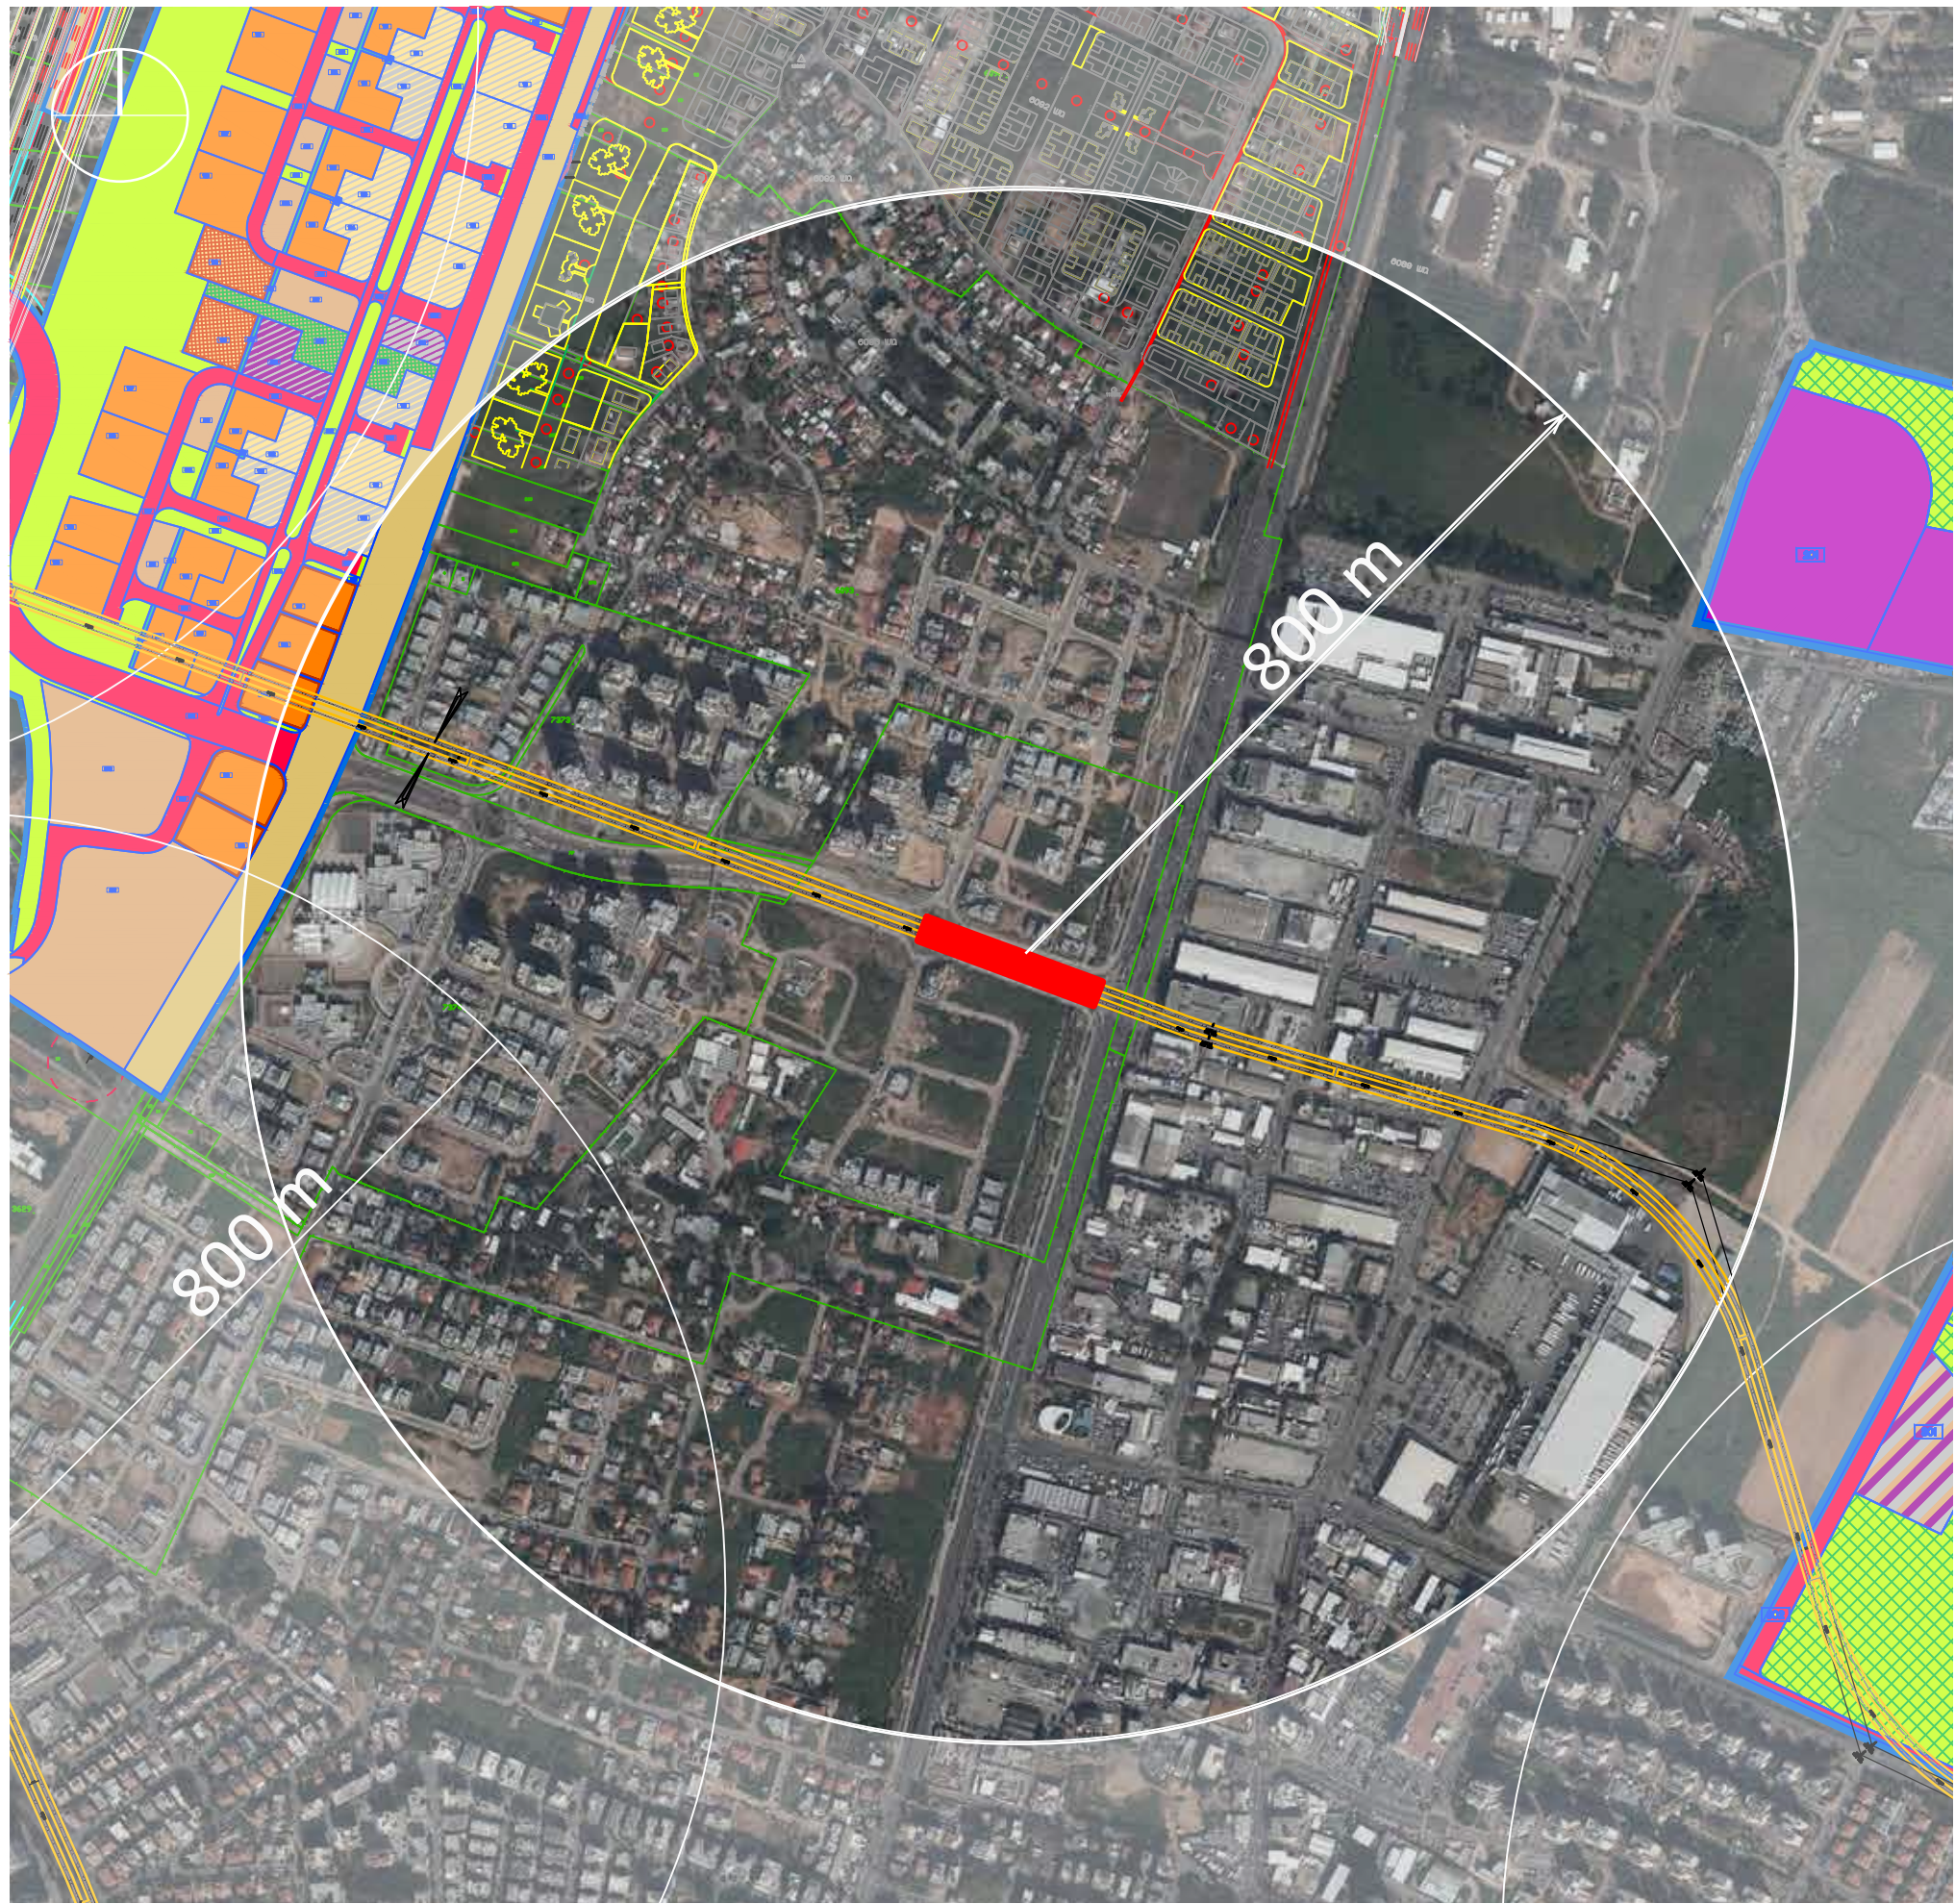


תכניות בהכנה
תחנה מס' 36 | שדרות הציונות

תכניות בהכנה
בסביבת התחנה

לא מקודמות תכניות ברדיוס 800m

רדיוס שירות

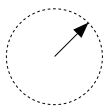

תוואי מטר



תחנת מטר




מפת ייעודי קרקע
תחנה מס' 36 | שדרות הציונות

ייעודי קרקע
מתכנית המתאר

- מגורים
- דרך מאושרת
- תעסוקה

תחנת מטר

- תוואי מטר
- תחנת מטר תת"ק
- מעברים תת קרקעיים
- מבנה כניסה לתחנה
- כניסה לתחנה

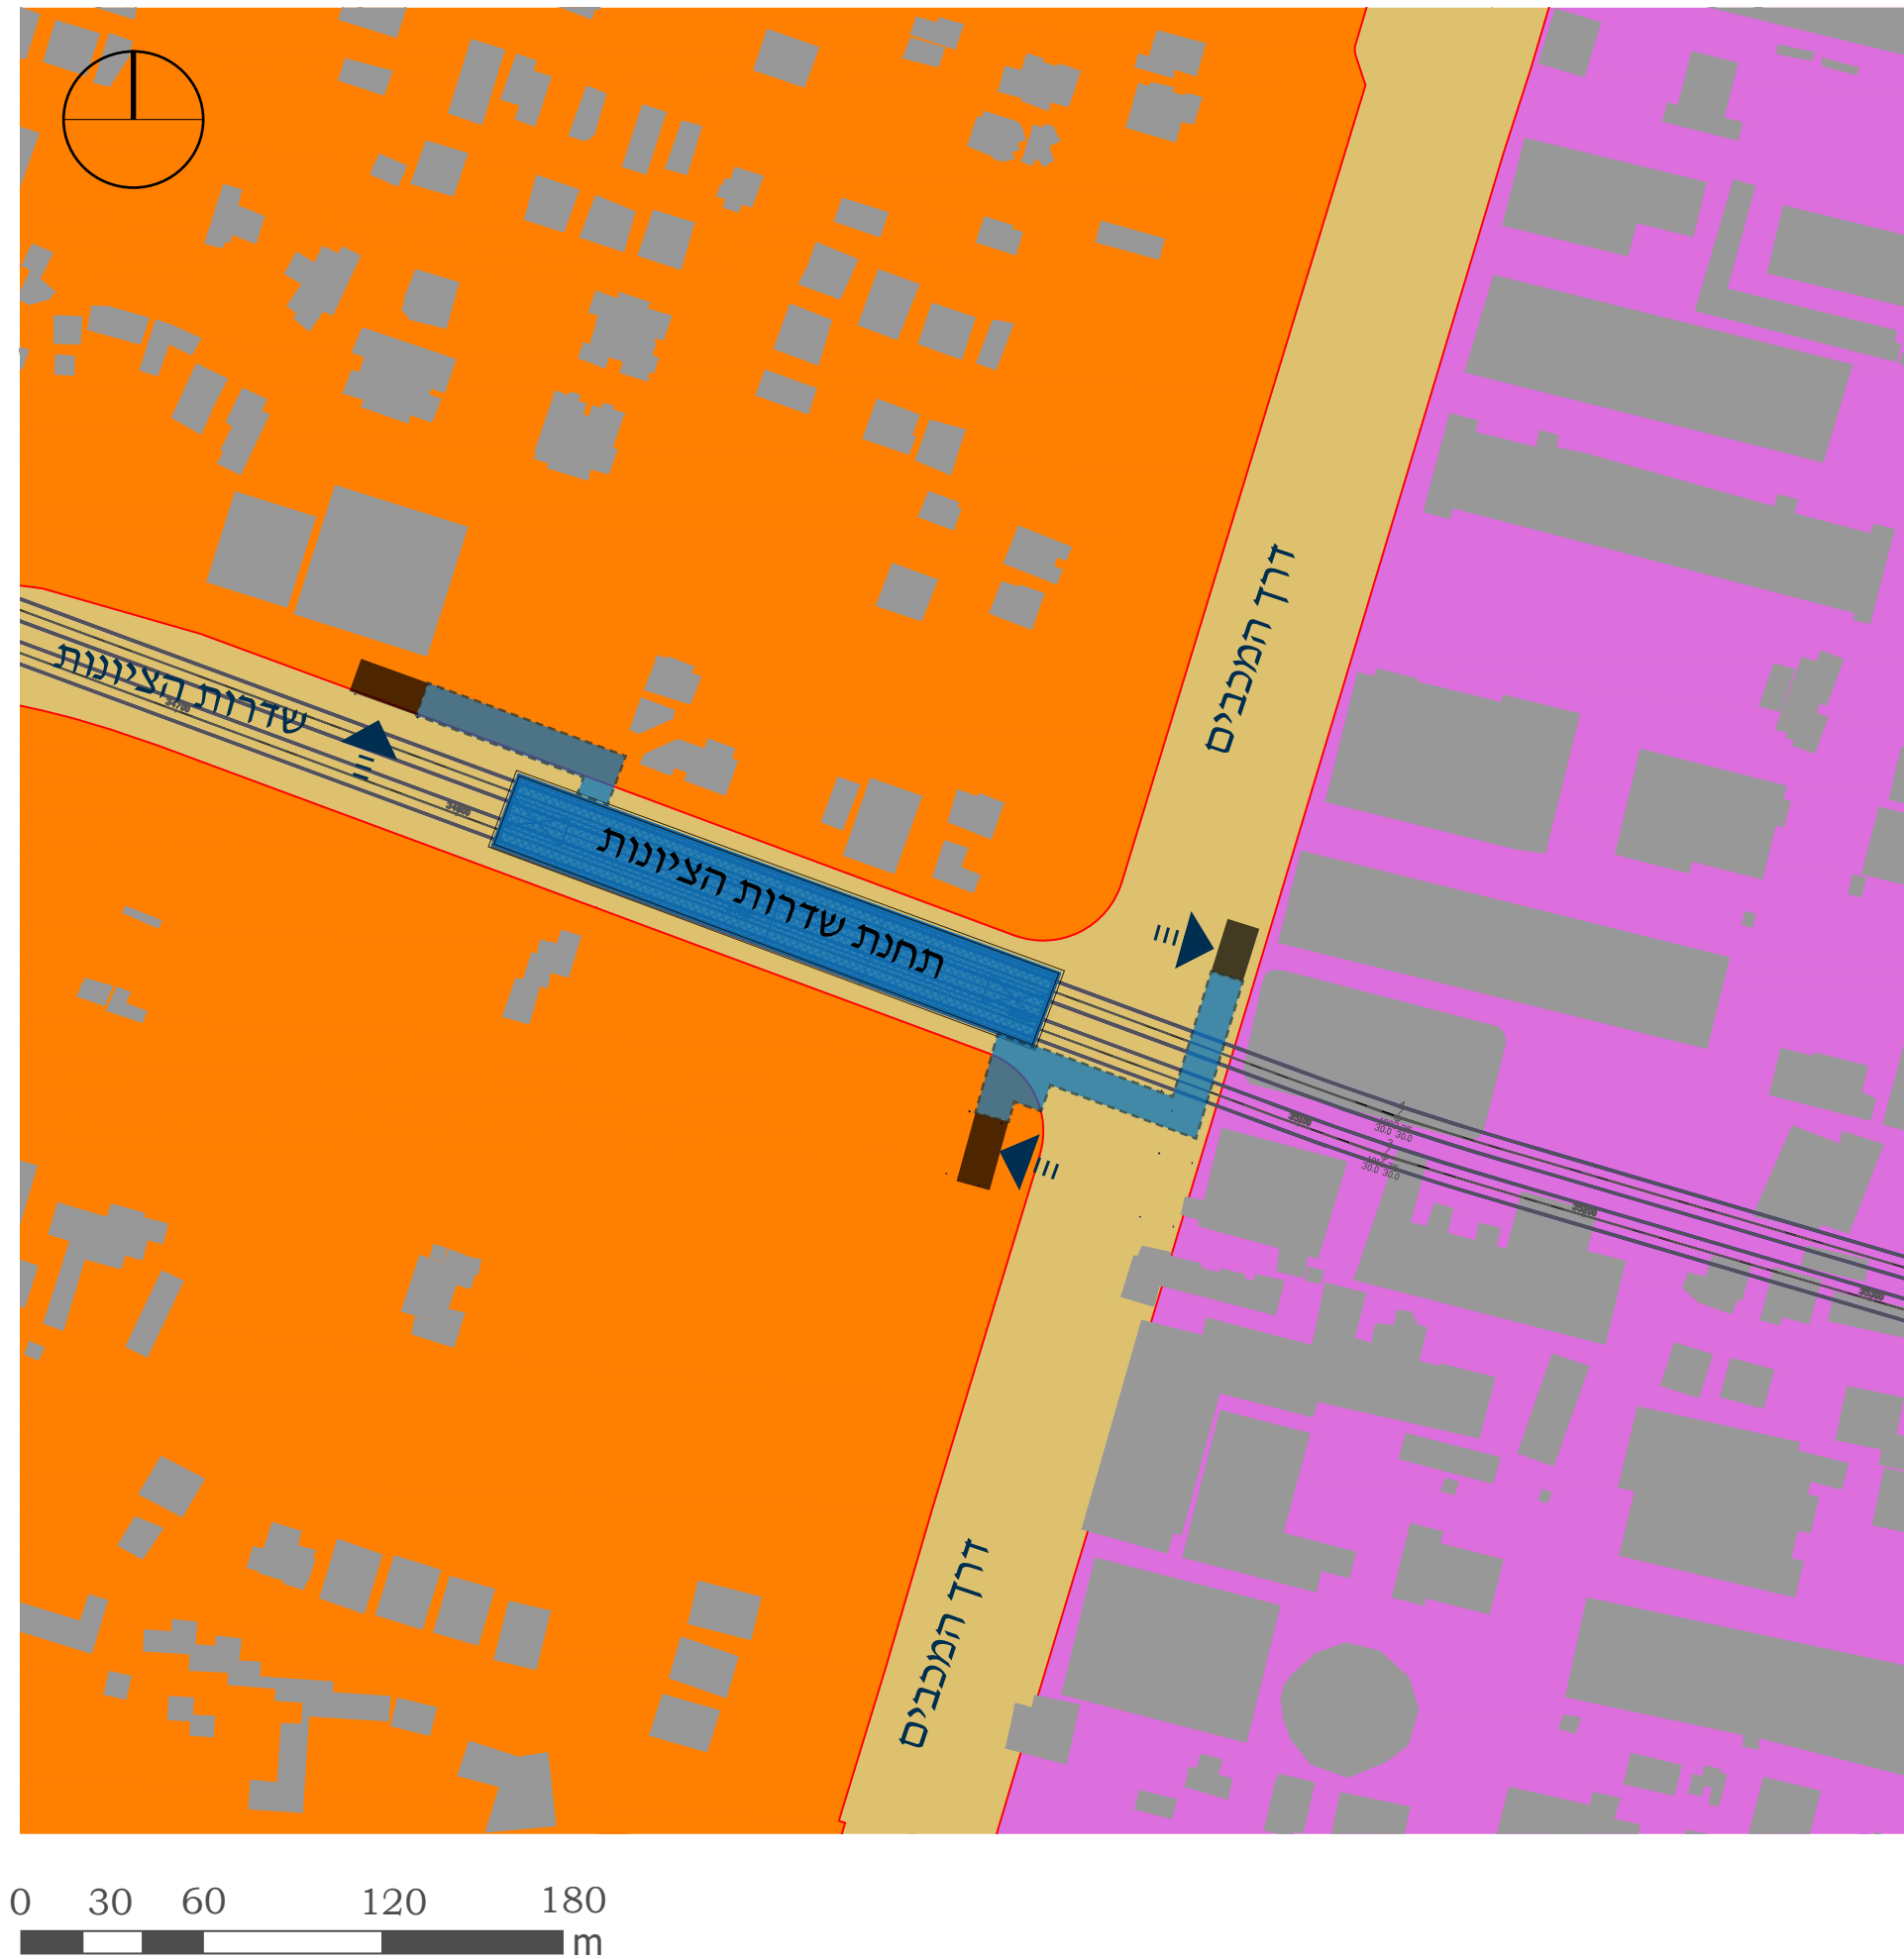

המרחב הציבורי

תחנה מס' 36 | שדרות הציונות

פיתוח קיים ומתוכנן

התחנה ממוקמת על רחוב שדרות הציונות בצומת עם דרך המכבים ציר ראשי המתחבר להרצל וחוצה את כל העיר מצפון לדרום. בשדרות הציונות 4 נתיבי תנועה המופרדים באי תנועה עם נטיעות של עצי הדר. בדרך המכבים 6 נתיבים, שניים מתוכם נתיבי תנועה, הנתיבים מופרדים באי תנועה מגוון. ממזרח תכנית לאנ"מ צפוני, במסגרתו מתוכננות 1,500 יח"ד. ממערב תכנית נחלת עילית, במסגרתה מתוכננות 4,000 יח"ד.

עוגנים למיקום הכניסות

התחנה ממוקמת באיזור מגורים, שכונות חדשות בראשון לציון וממערב לאיזור תעסוקה. תוכננו שלוש כניסות. הכניסה המערבית ממוקמת על שדרות הציונות ומשרתת את שכונת המגורים ממערב. ממזרח תוכננו שתי כניסות משני צידי דרך המכבים, המהווה ציר ראשי (כביש 412). הכניסות משרתות את שכונת המגורים ואת איזור התעסוקה ממזרח.

קישוריות ונגישות

נגישות להולכי רגל במערך הרחובות הקיימים בשדרות הציונות, דרך המכבים והעצמאות המקשרים אל גן האירועים ובתי הספר הנמצאים דרום מערבית לתחנה. שבילי אופניים מתוכננים בשדרות הציונות ובדרך המכבים אשר ממשיכה למתחברת לרחוב הרצל. קישוריות לתחנת אוטובוס על דרך המכבים.

תחנת מטר

- תוואי מטר
- תחנת מטר תת"ק
- מעברים תת קרקעיים
- מבנה כניסה לתחנה
- כניסה לתחנה
- מבנים
- שצי"פ סטטוטורי
- מבנים ומוסדות ציבור סטטוטוריים
- שביל אופניים קיים
- שביל אופניים מתוכנן
- ציר הולכי רגל ראשי
- ציר הולכי רגל משני





מצב מאושר
תחנה מס' 36 | שדרות הציונות
ייעודי קרקע
מאושרים

- דרך משולבת
- דרך מאושרת
- שטח ציבורי פתוח
- מגורים א'
- מגורים ב'
- מגורים ג'
- תעשייה
- מסחר ותעשייה
- תעשייה
- מבנים ומוסדות ציבור
- שטח המוכרז כאתר עתיקות




כניסה לתחנה



תחנת מטרו תת"ק



מעברים תת קרקעיים

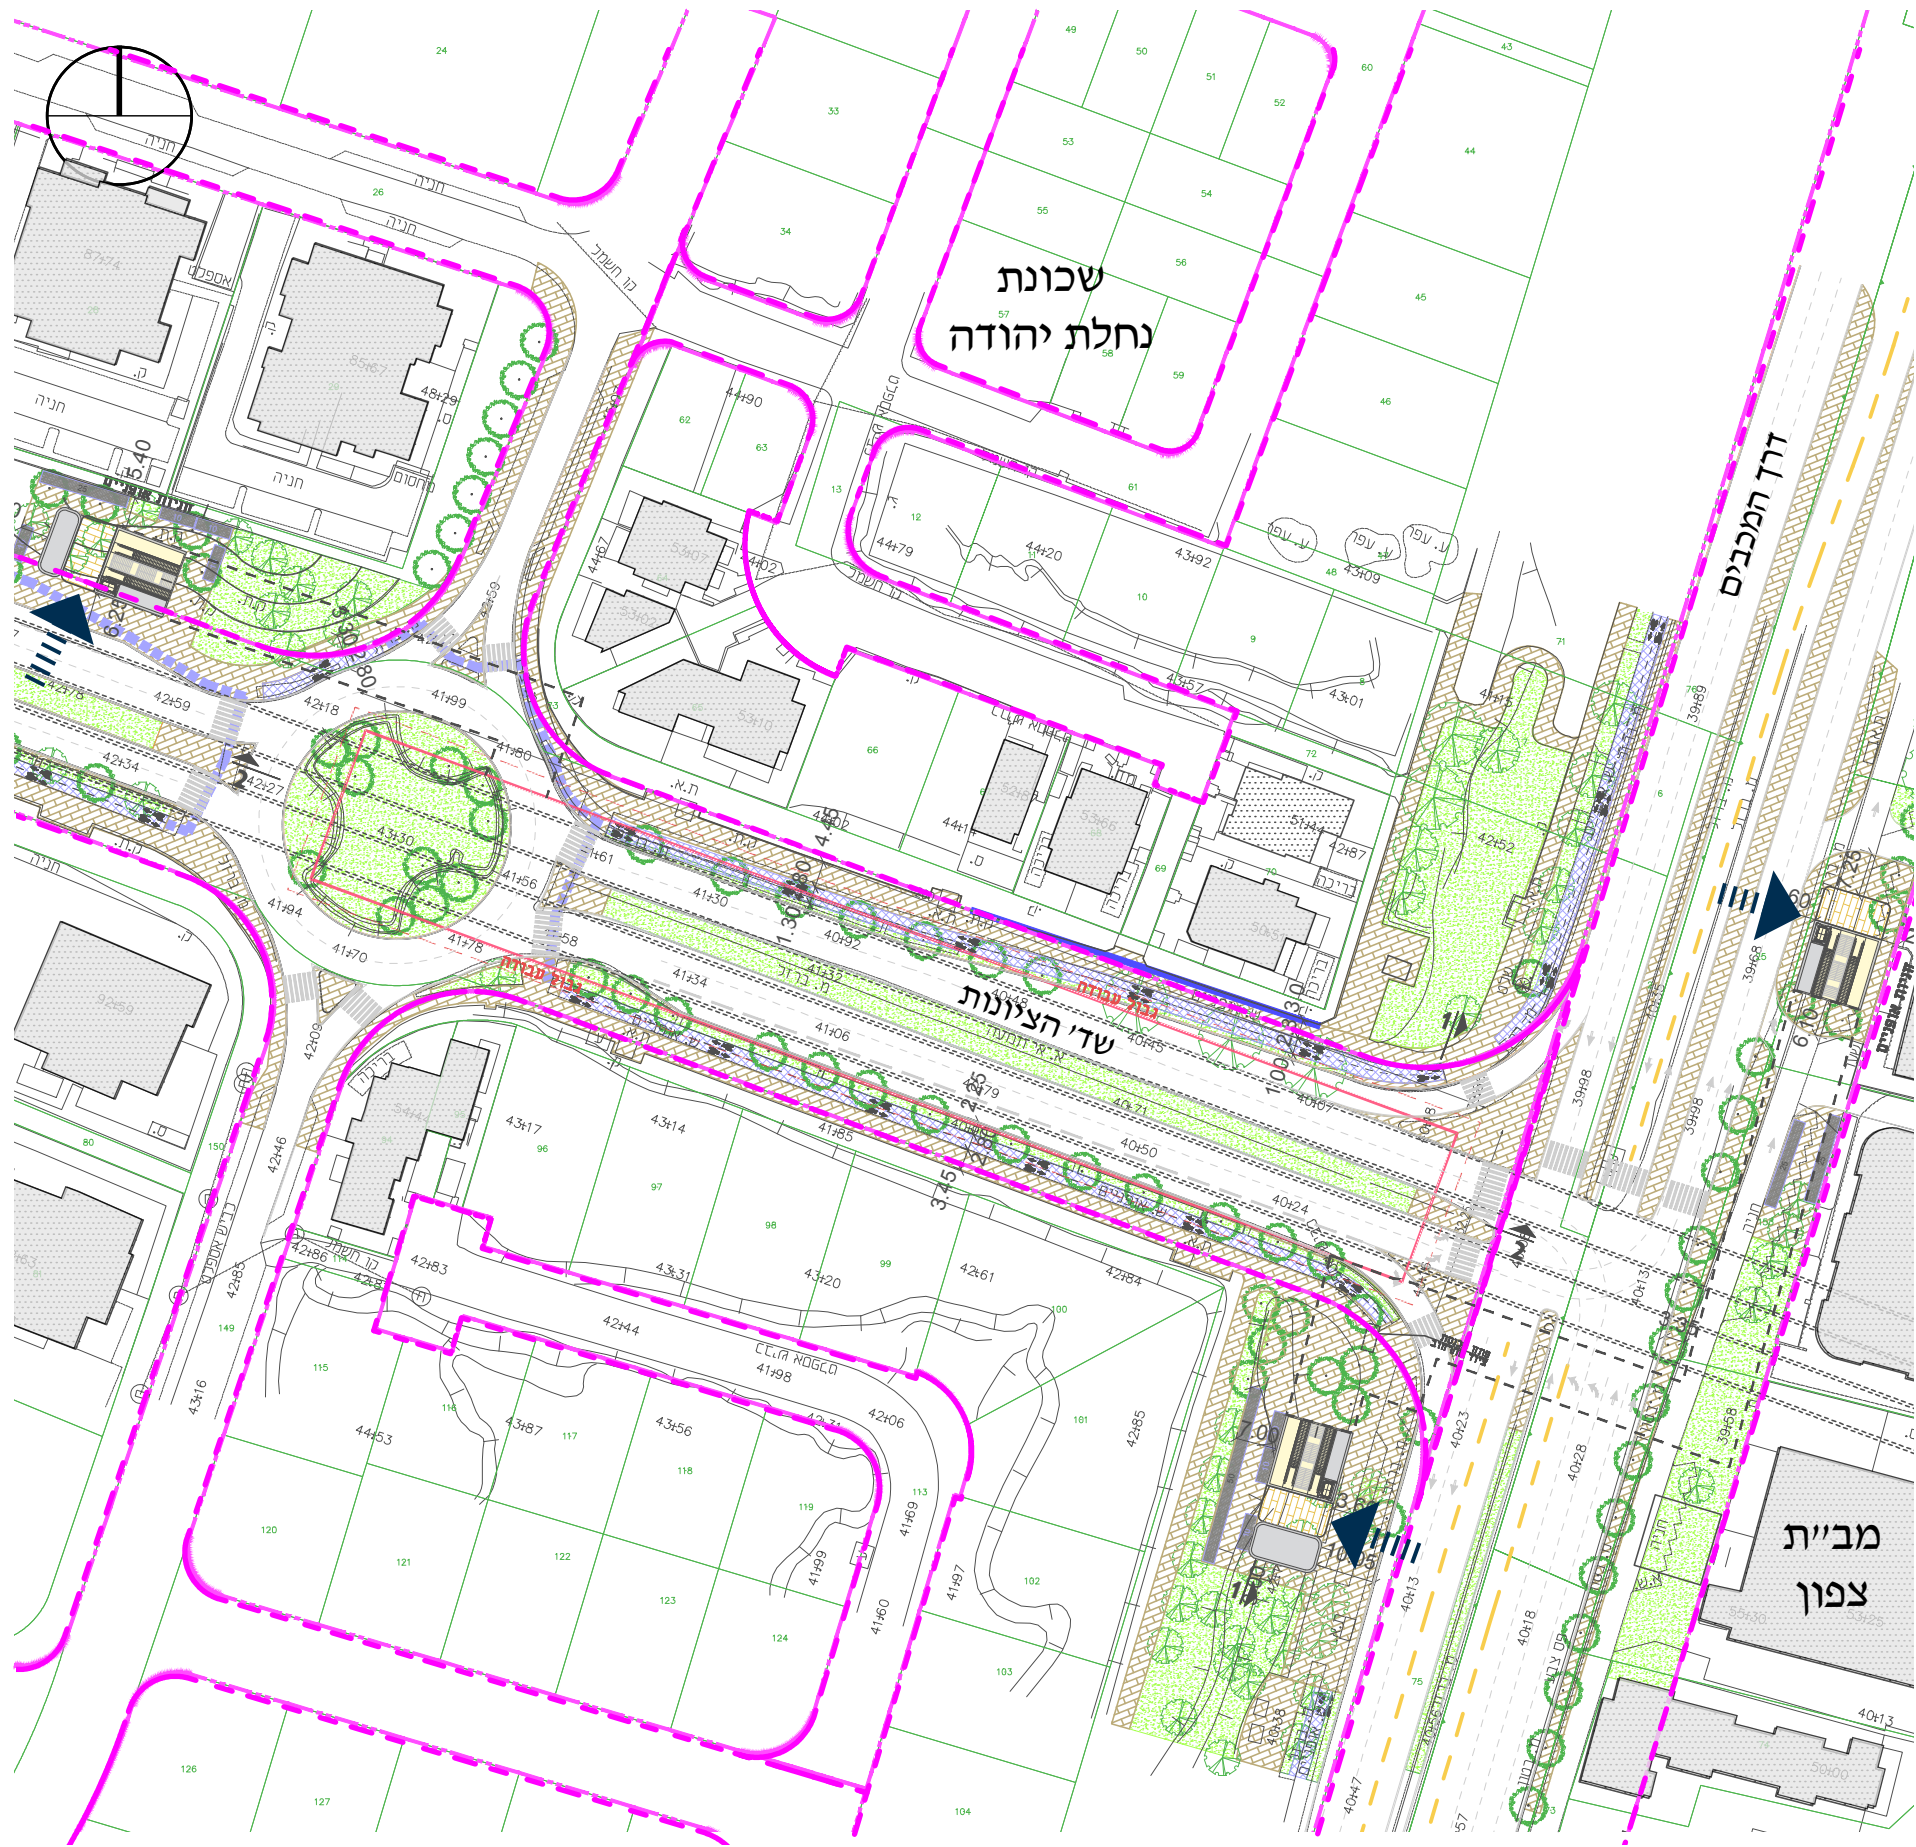

השתלבות במערך הסביבתי

תחנה מס' 36 | שדרות הציונות

עץ קיים



עץ מתוכנן



גינון



מדרכה



זכות הדרך




תחנת מטרו תת"ק



מעברים תת קרקעיים



תוואי מטרו

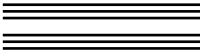

כניסה לתחנה





מבנה להריסה



תחנת אוטובוס



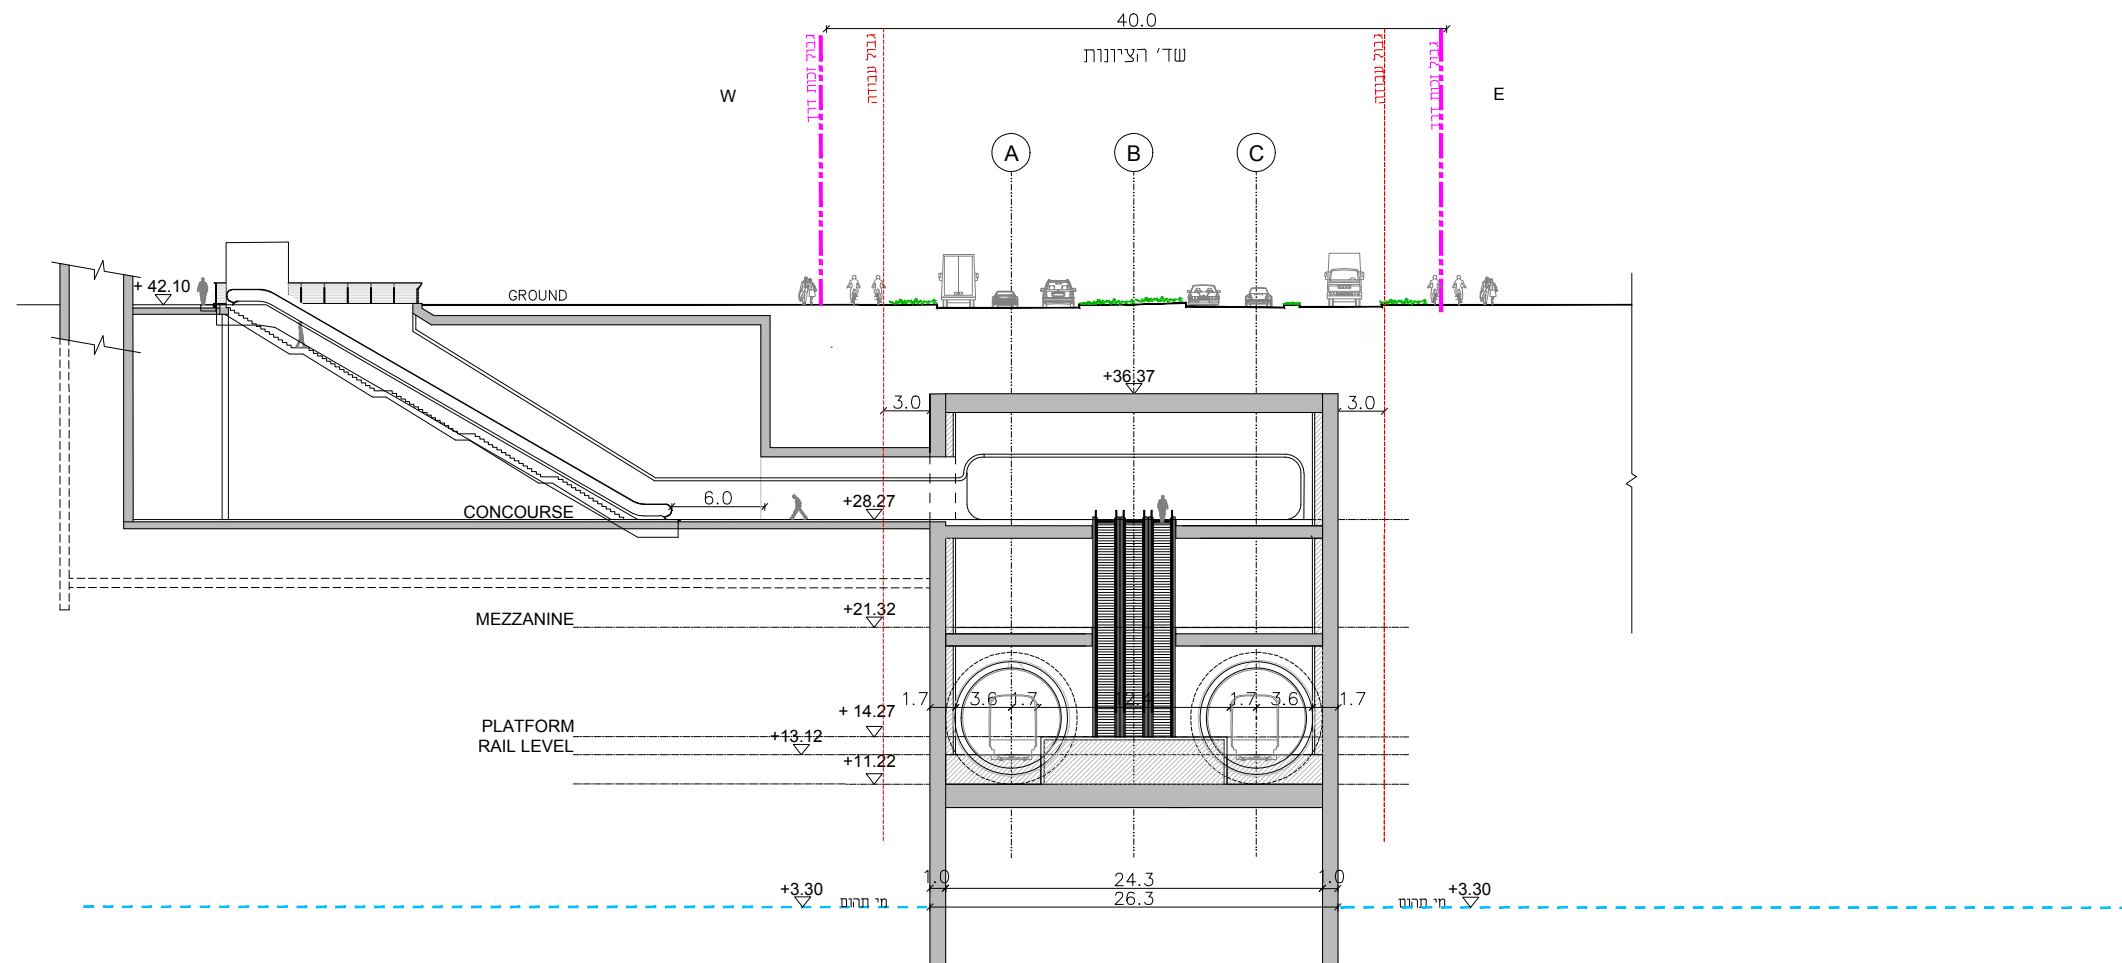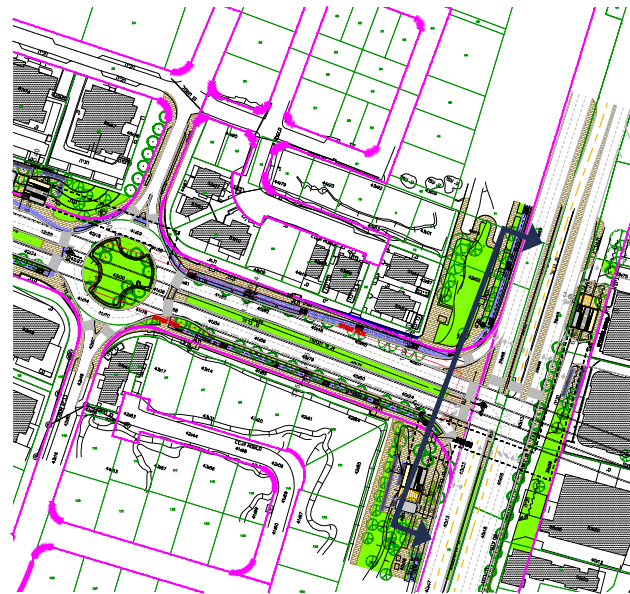

חתך רוחב
תחנה מסי 36 | שדרות הציונות



- תחנת מטרו תת"ק
- כניסה לתחנה

מסקנות והמלצות

תחנה מס' 36 | שדרות הציונות

1. התחנה משרתת איזור של פיתוח שכונות מגורים ממערב ואיזור תעסוקה ממזרח.
2. מתוכננות שלוש כניסות. כניסה מערבית המשרתת את השכונות ממערב. הכניסות המזרחיות מתוכננות משני עברי דרך המכבים. הכניסות ישמשו כמעבר הולכי רגל תת-קרקעי גם ללא כניסה לתחנת המטרו שיקשר את השכונה לאיזור התעסוקה ולפיתוח האנ"מ העתידי ממזרח לו.
3. מומלץ, במסגרת פיתוח האנ"מ, להמשיך את שדרות הציונות מזרחה בתוך איזור התעסוקה וכך לקשור את שטחי הפיתוח העתידיים באנ"מ לתחנת המטרו.

אפיון התחנה

תחנה מס' 37 | יוסף בורג

- **מיקום התחנה**
ראשון לציון, ממוקמת על רחוב יעקב פריימן מערב לצומת ד"ר יוסף בורג/מנחם גינדי. מצפון שטחים חקלאיים. מדרום לתחנה בית העלמין הישן ראשון לציון. ממזרח לתחנה כביש 44 הראשי. מדרום מערב לתחנה שכונת המגורים נעורים. מדרום מזרח שכונת מרום ראשון.


- **סוג תחנה**
תחנה רגילה

- **אפיון פיסי | סביבת התחנה**
שכונת המגורים נעורים היא שכונה חדשה ובה מבנים דו משפחתיים צמודי קרקע ומבני מגורים עד 12 קומות. שכונת מרום ראשון היא שכונה חדשה עם מבנים עד 12 קומות. מצפון שטחים חקלאיים - באיזור זה תכנית בהכנה אנ"מ צפוני - רצ/130, בה מתוכננים 1,500 יח"ד.

- **מוקדי עניין**
(במרחק של עד 800 מ' מהתחנה)
בית העלמין הישן ראשון לציון. כמו כן, תכנית האנ"מ המ' תוכננת מצפון תתאים עצמה ע"י עירוב שימושים ומוקדי עניין עפ"י למיקום התחנה.

- **קישוריות ונגישות**
נגישות הולכי רגל המחברת בין גנים ציבוריים ברחובות יעקב פריימן, ד"ר יוסף בורג וכתריאל רפפורט. שביל אופניים מתוכנן ברחוב יעקב פריימן (מזרח מערב), בדרך חיים הרצוג (צפון דרום), שביל אופניים מתוכנן המוביל לאזור האנ"מ העתידי (צפונה) ושביל אופניים מתוכנן המוביל דרומה לאורך בית העלמין אל תוך העיר. קישוריות לתחנות אוטובוס על רחוב פריימן.

- **קיבולת נוסעים צפויה**
תחזית נוסעים לשנת 2040 צופה כ- 1430 נוסעים עולים ויורדים בשעת שיא.

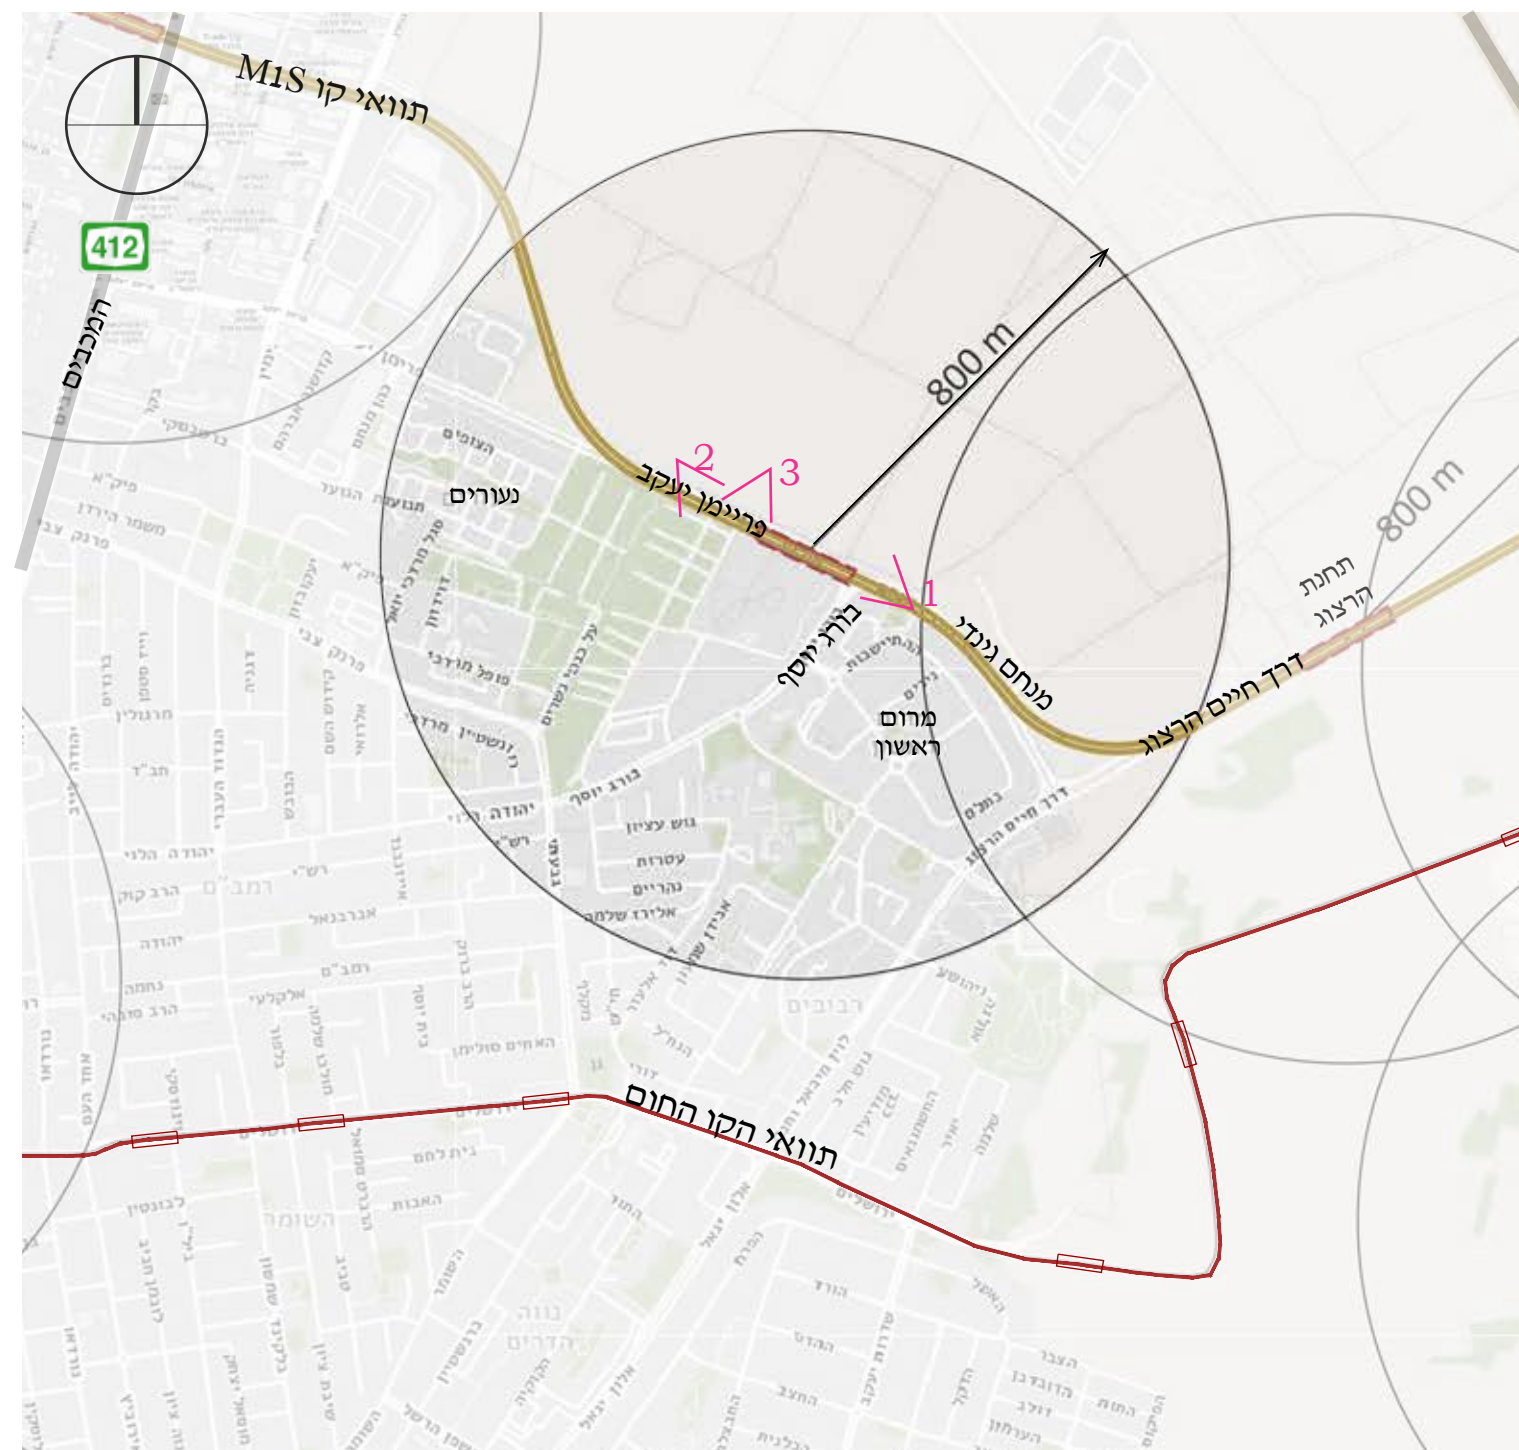

1. מבט מכיוון דרום
2. מבט מכיוון צפון
3. מבט מערבה

