
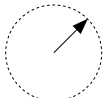


סביבת התחנה:
 מיפוי אגן
 היקוות התחנה
 תחנה מס' 37 | יוסף בורג

- רדיוס שירות 
- תוואי מטר 
- תחנת מטר 

- מתחם ציבורי פתוח/גן/פארק 
- ציר עירוני ראשי - וקטור ביקוש 
- ציר עירוני - וקטור ביקוש 
- שביל אופניים קיים 
- שביל אופניים מתוכנן 
- ציר הולכי רגל ראשי 
- ציר הולכי רגל מתוכנן 

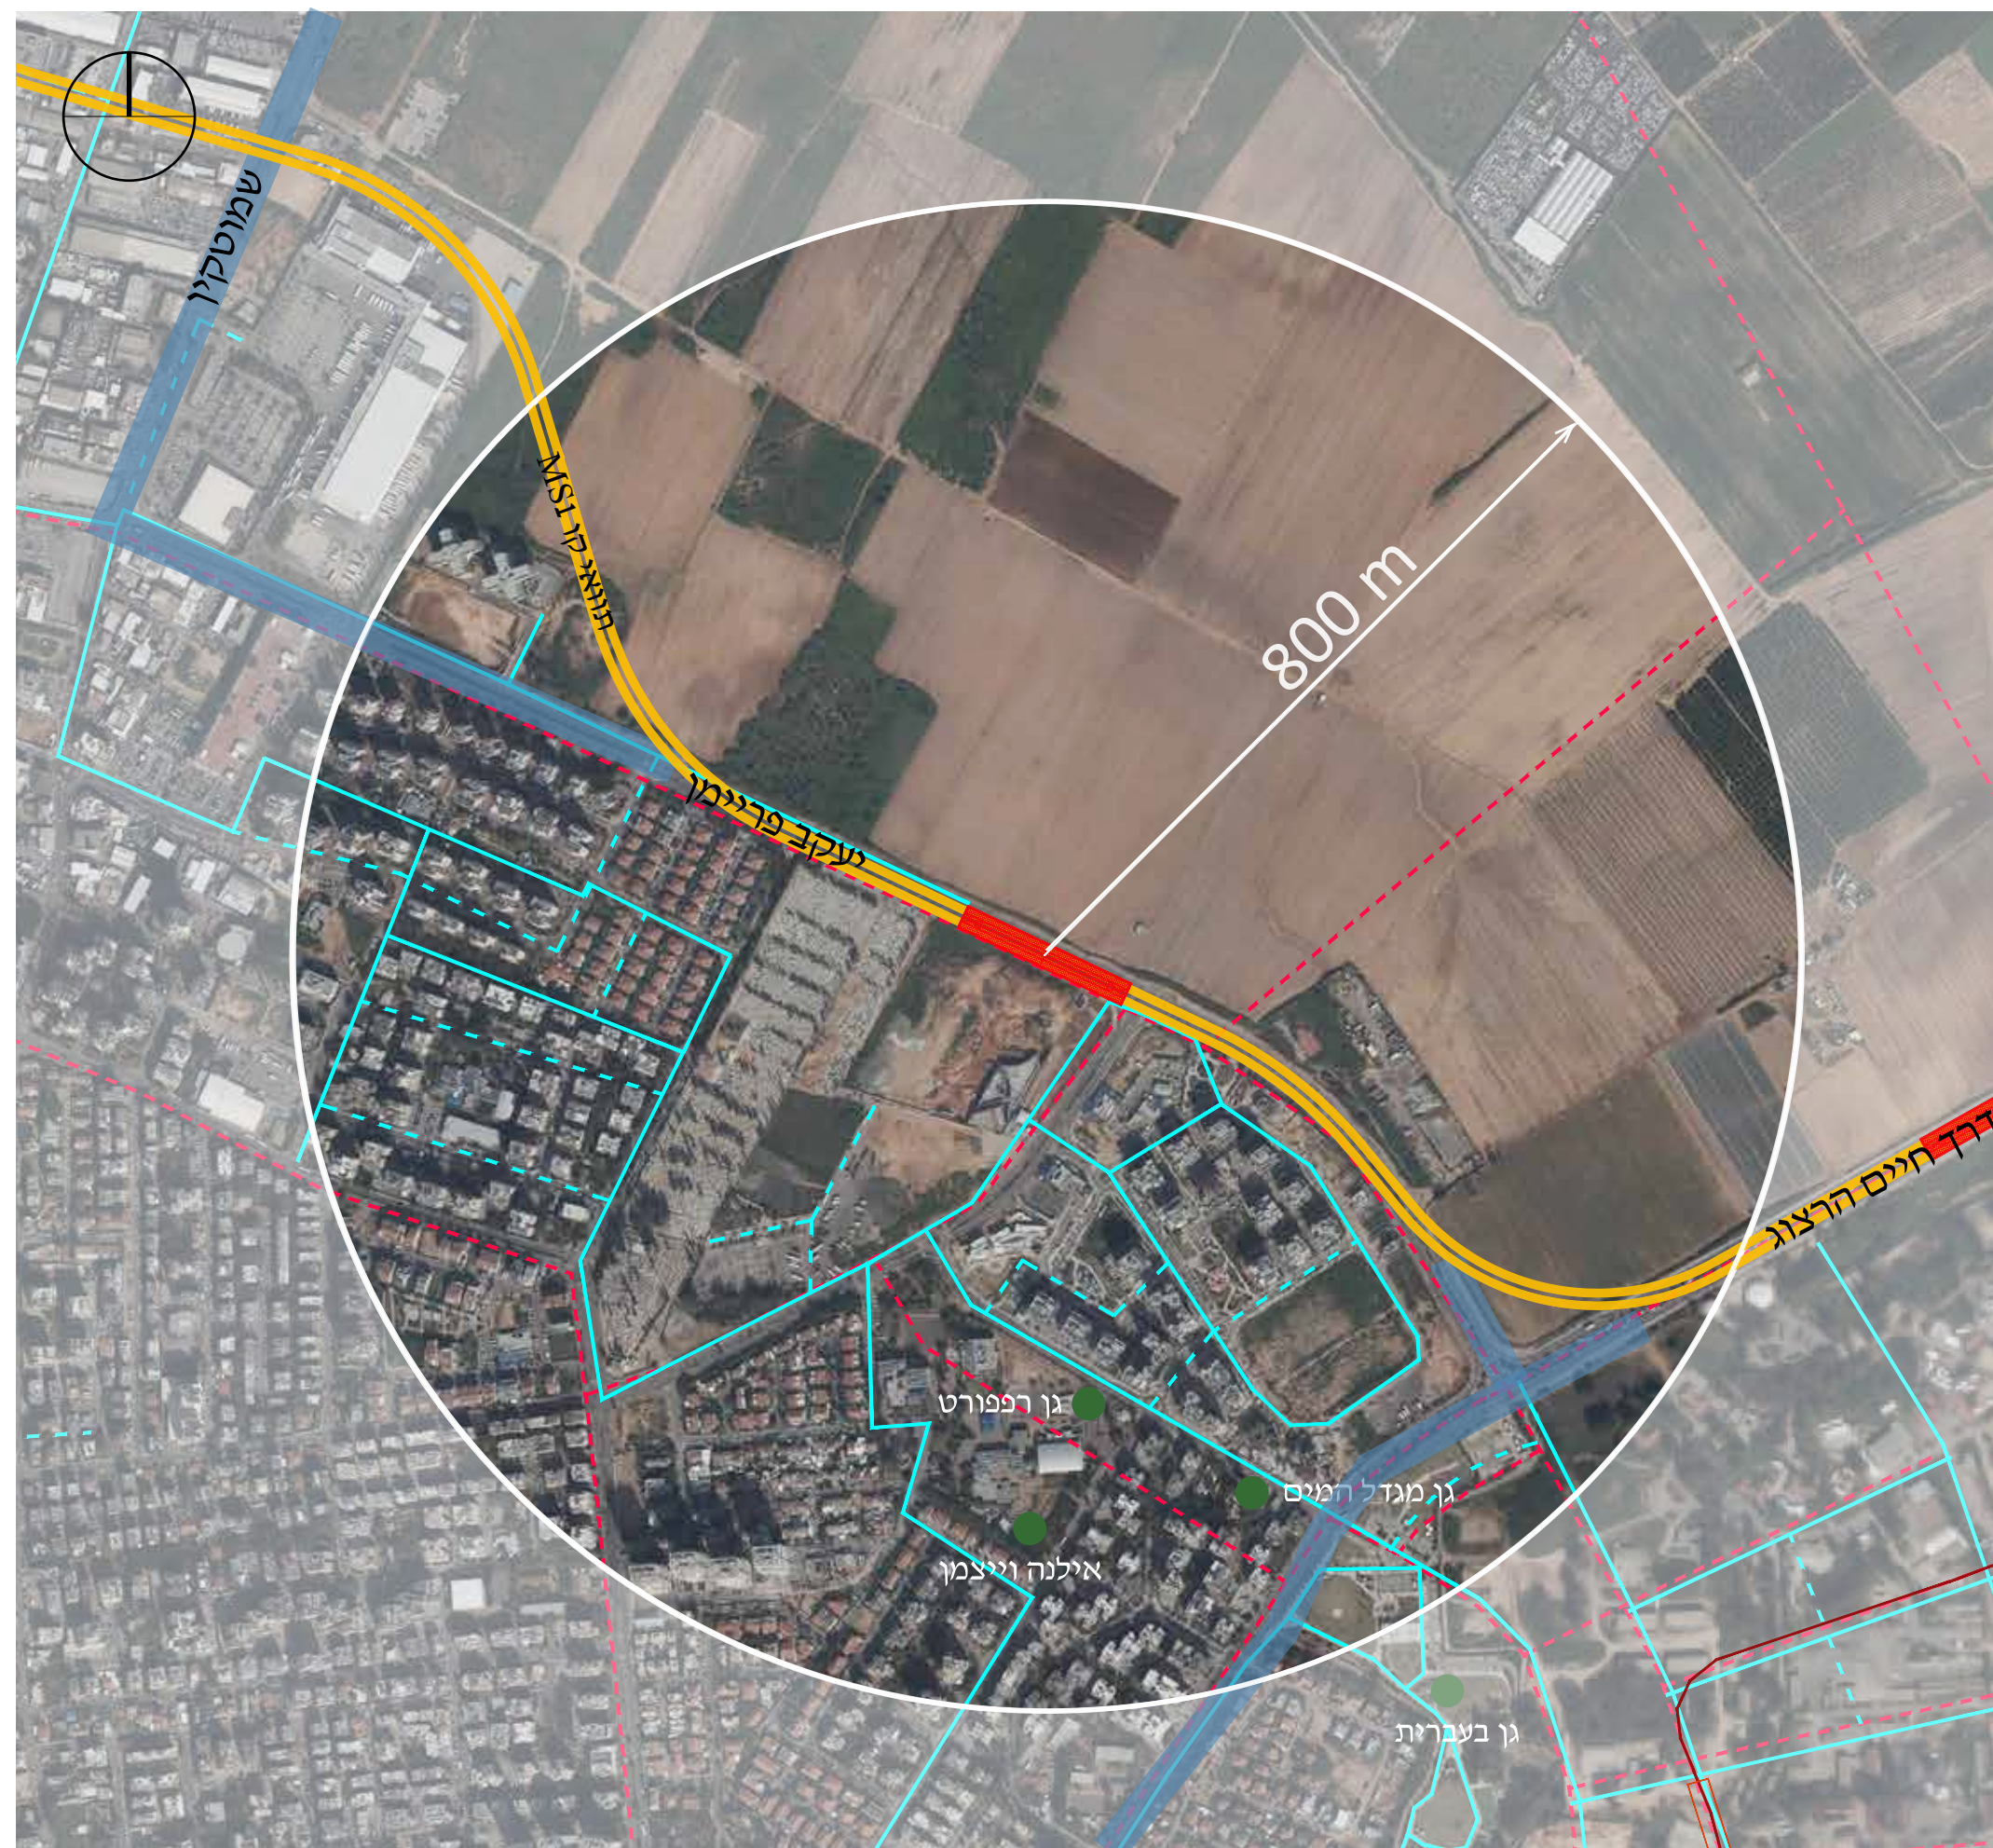


M1S

ת. יוסף בורג

סביבת התחנה

1:7500

171

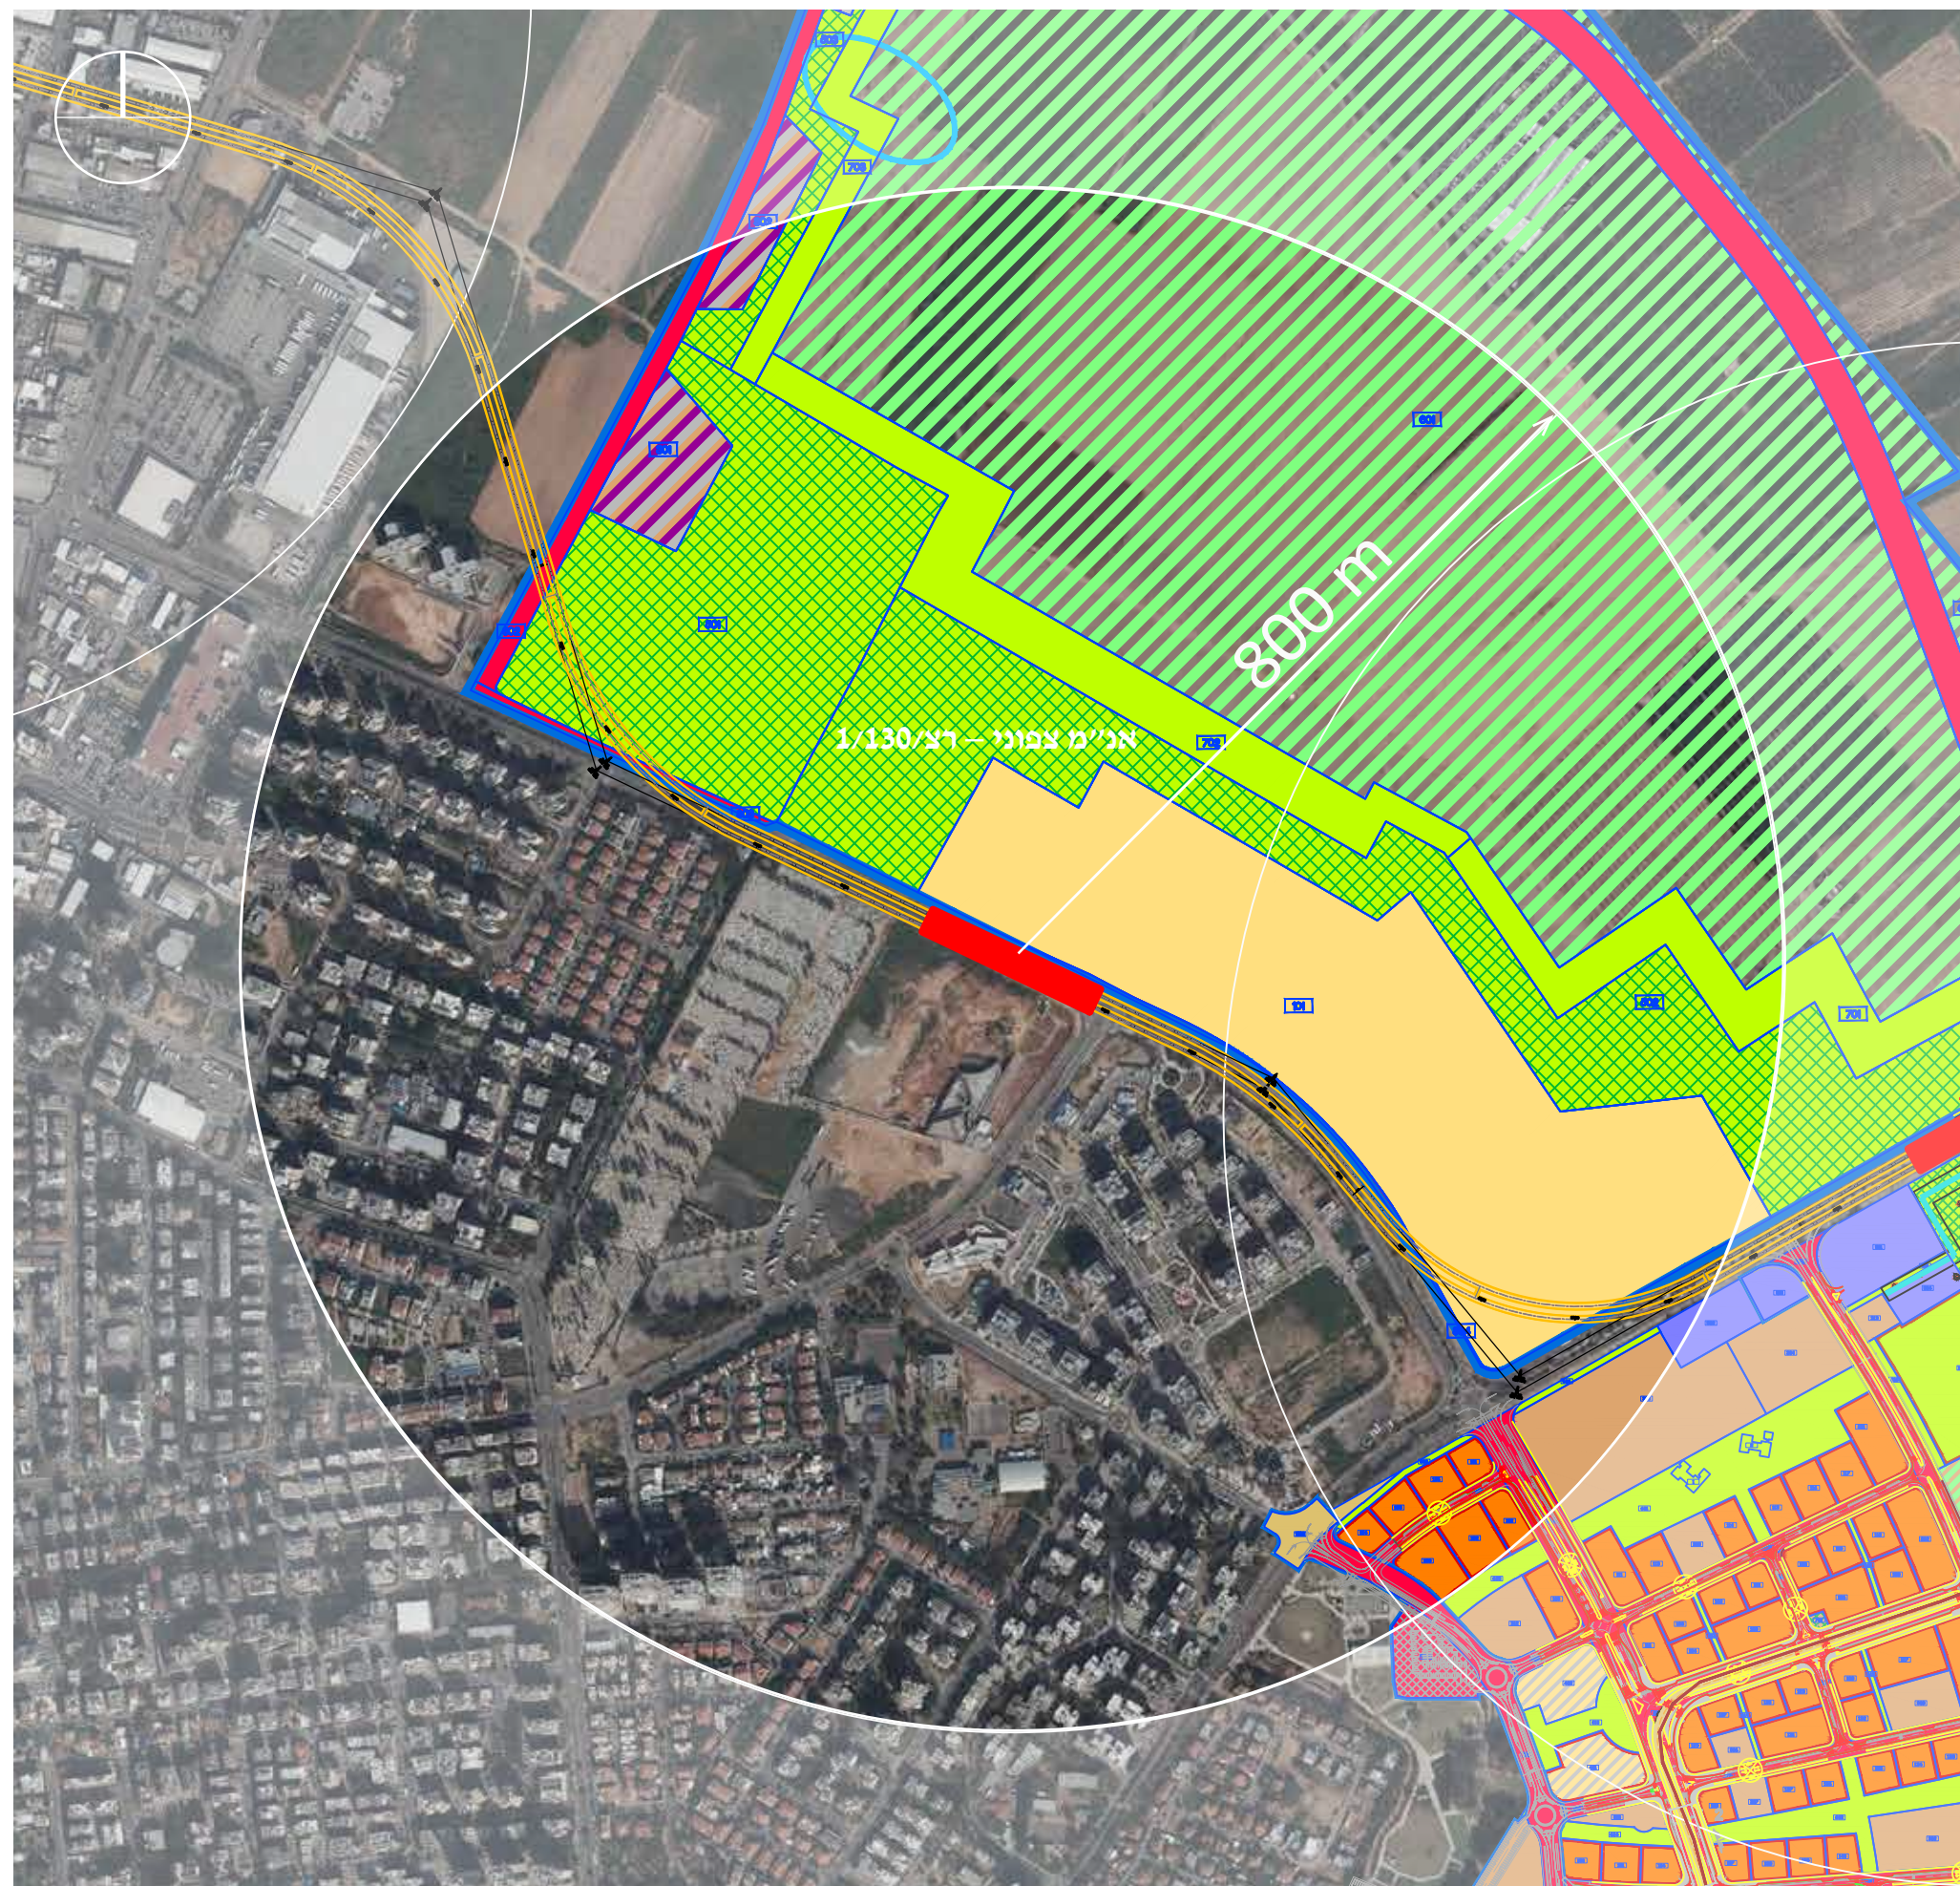


תכניות בהכנה תחנה מס' 37 | יוסף בורג

תכניות בהכנה בסביבת התחנה

שם התכנית:
אני"מ צפוני – רצ/130
בתכנון: יאיר אביגדור אדריכלים
סטטוס: לפני הפקדה
מתוכנן: 1,500 יח"ד.

רדיוס שירות

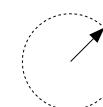

תוואי מטר



תחנת מטר




מפת ייעודי קרקע

תחנה מס' 37 | יוסף בורג

ייעודי קרקע מתכנית המתאר

- מגורים
- מגורים
- דרך מאושרת
- מגורים, מסחר ומבנים
ומוסדות ציבור
- דרך מוצעת
- בית עלמין
- קרקע חקלאית

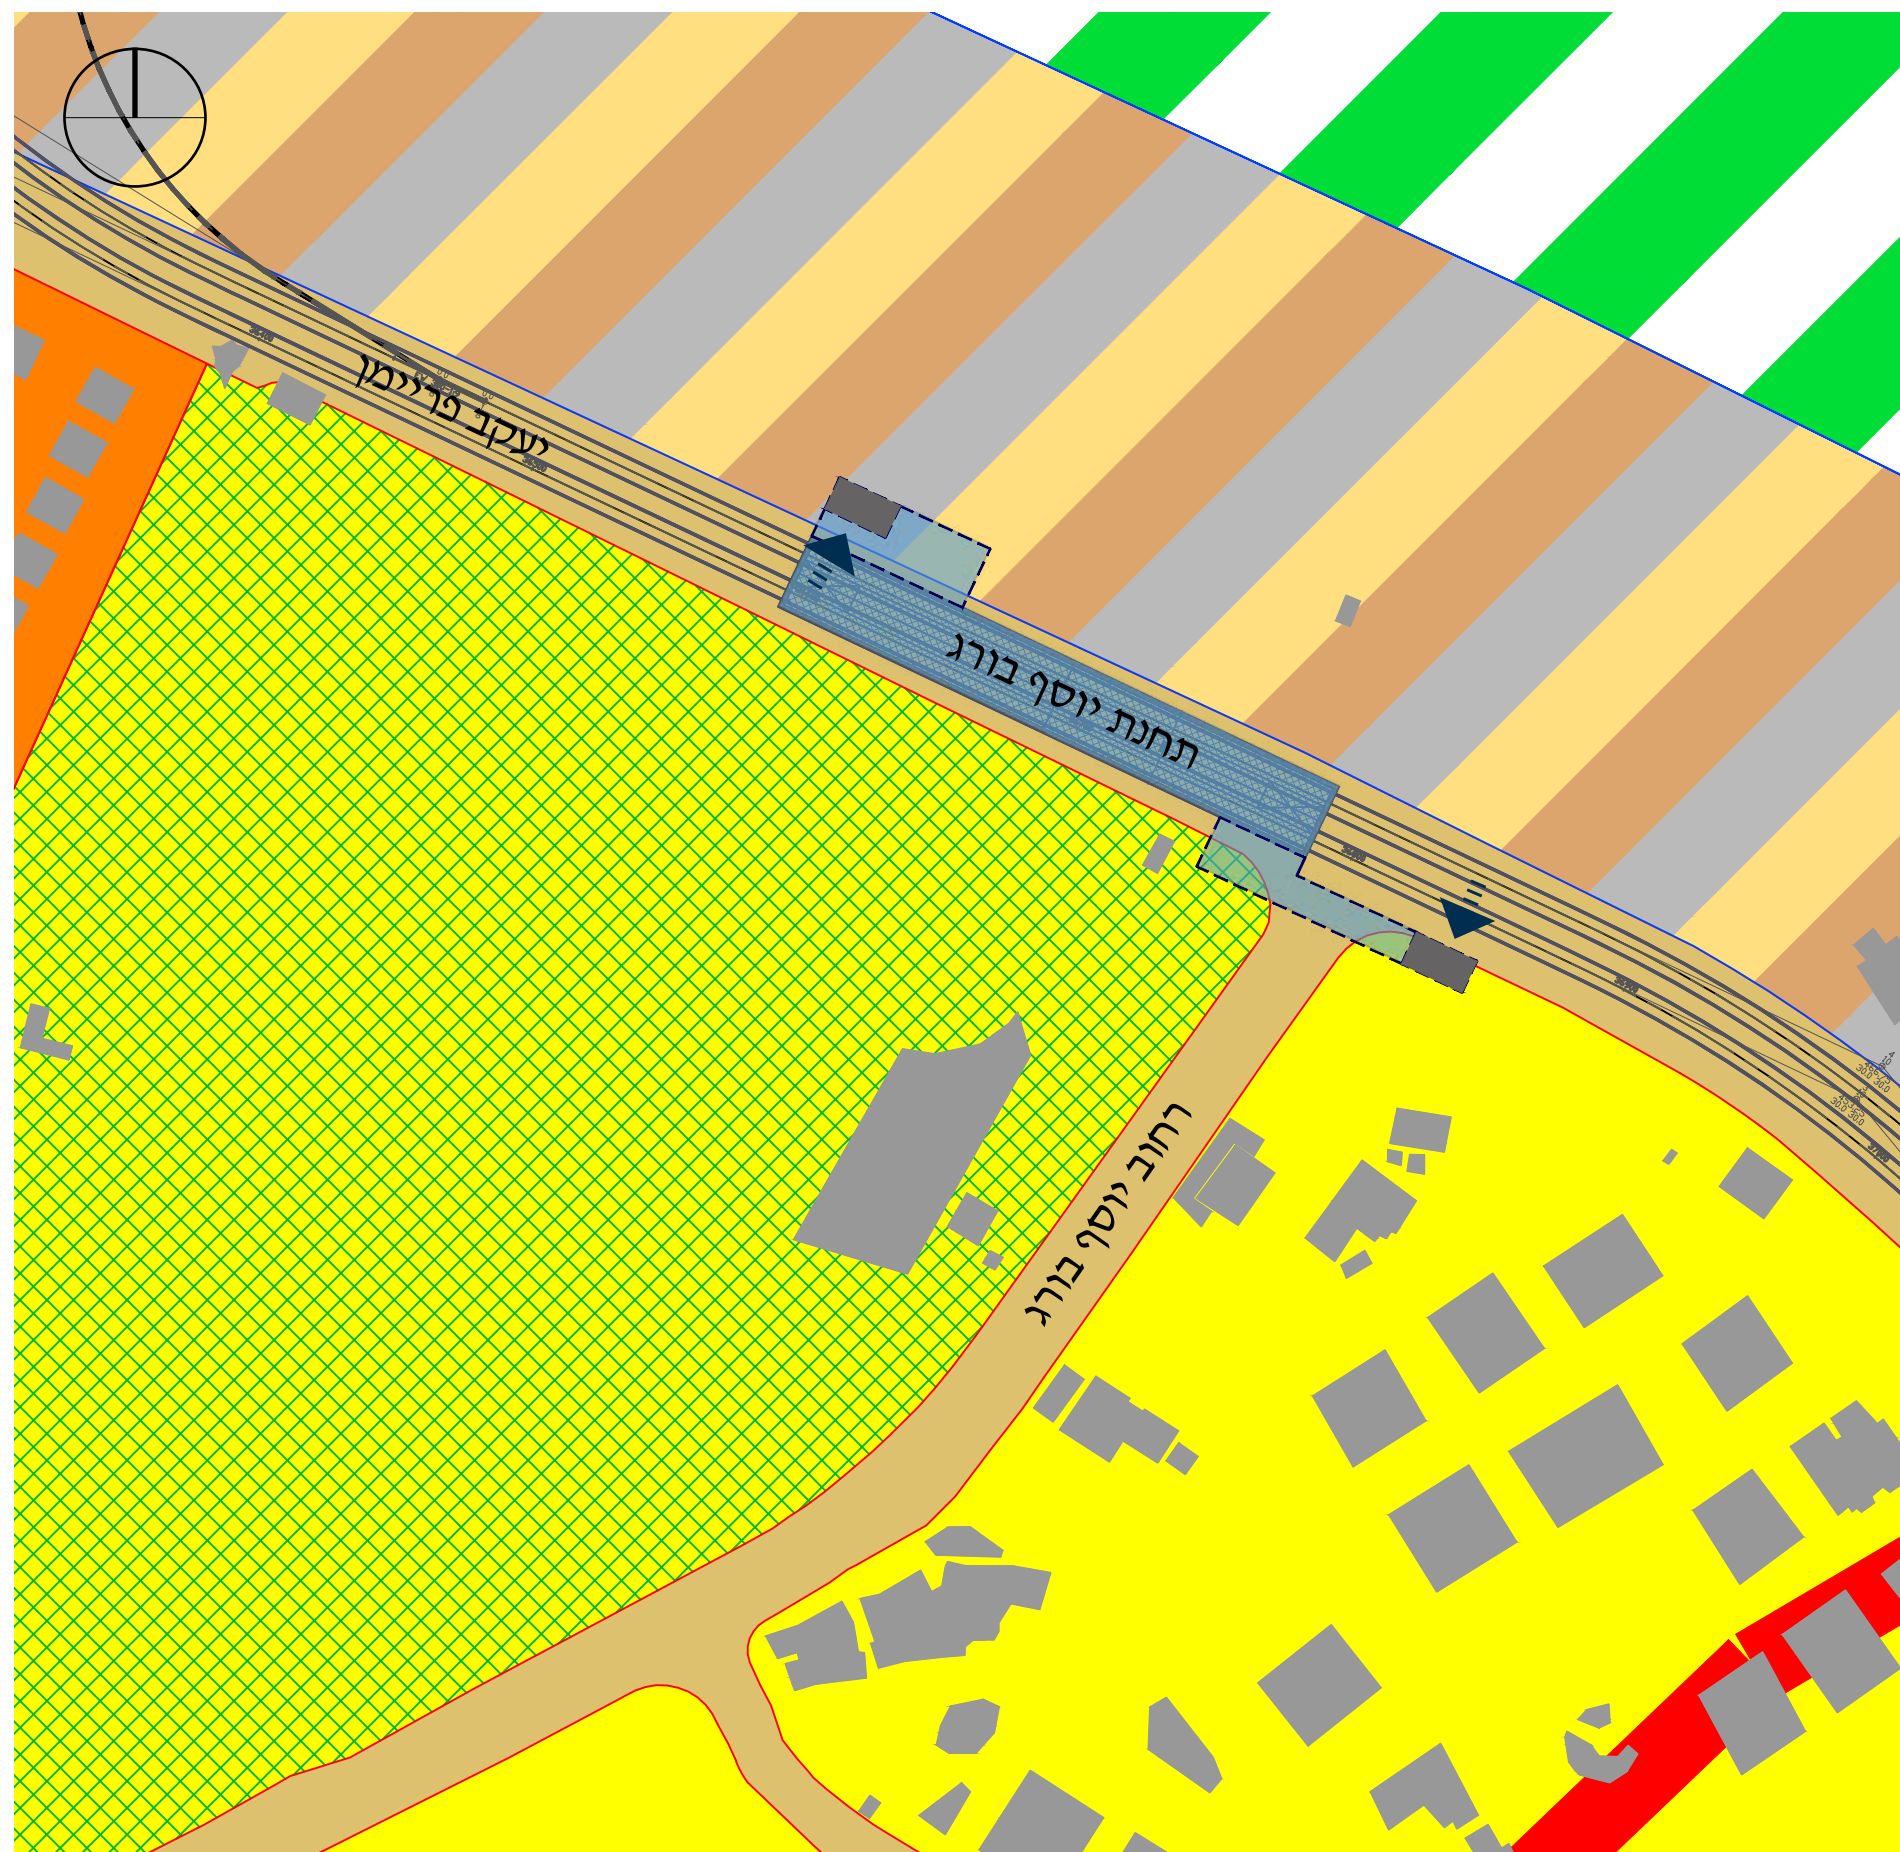

0 30 60 120 180 m

M1S

ת. יוסף בורג

ייעודי קרקע

1:2500

173

המרחב הציבורי

תחנה מס' 37 | יוסף בורג

פיתוח קיים ומתוכנן

התחנה ממוקמת על רחוב יעקב פריימן בסמוך לרחוב יוסף בורג. ברחוב זה 4 נתיבי תנועה ובניהם אי תנועה עם שדרת דקלים מרכזית. ברחוב יוסף בורג 4 נתיבי תנועה המופרדים באי תנועה מגוון. התחנה בקרבה לאזור מגורים עתידי ואזור נופש מטרופוליני של מזרח ראשון.

עוגנים למיקום התחנה והכניסות

התחנה מוקמה על ציר עירוני ראשי מדרום לאזור לפיתוח עתידי במסגרת האני"מ צפוני. תוכננו שתי כניסות. הכניסה המערבית ממוקמת מצפון לרחוב יעקב פריימן. כניסה זו נמצאת כיום בשטח חקלאי, אך עתידה לשרת את פיתוח עתידי של אני"מ, עפ"י תכנית המתאר. הכניסה ממזרח מתוכננת על הצומת עם רחוב ד"ר יוסף בורג, המהווה את דרך הכניסה לשכונה מדרום, וכמו כן משרתת את בית הקברות הקיים.

קישוריות ונגישות

נגישות הולכי רגל במערך רחובות קיימים יעקב פריימן, ד"ר יוסף בורג, ההתיישבות, ההכשרות ובשבילי הולכי רגל בשצ"פ. שבילי אופניים מתוכננים ברחוב יעקב פריימן, שביל המוביל לאני"מ העתידי ושביל לאורך בית העלמין דרומה.

תחנת מטר


- תוואי מטר
- תחנת מטר תת"ק
- מעברים תת קרקעיים
- מבנה כניסה לתחנה
- כניסה לתחנה
- מבנים
- שצ"פ סטטוטורי
- מבנים ומוסדות ציבור סטטוטוריים
- שביל אופניים קיים
- שביל אופניים מתוכנן
- ציר הולכי רגל ראשי
- ציר הולכי רגל משני

M1S

ת. יוסף בורג

המרחב הציבורי

1:2500

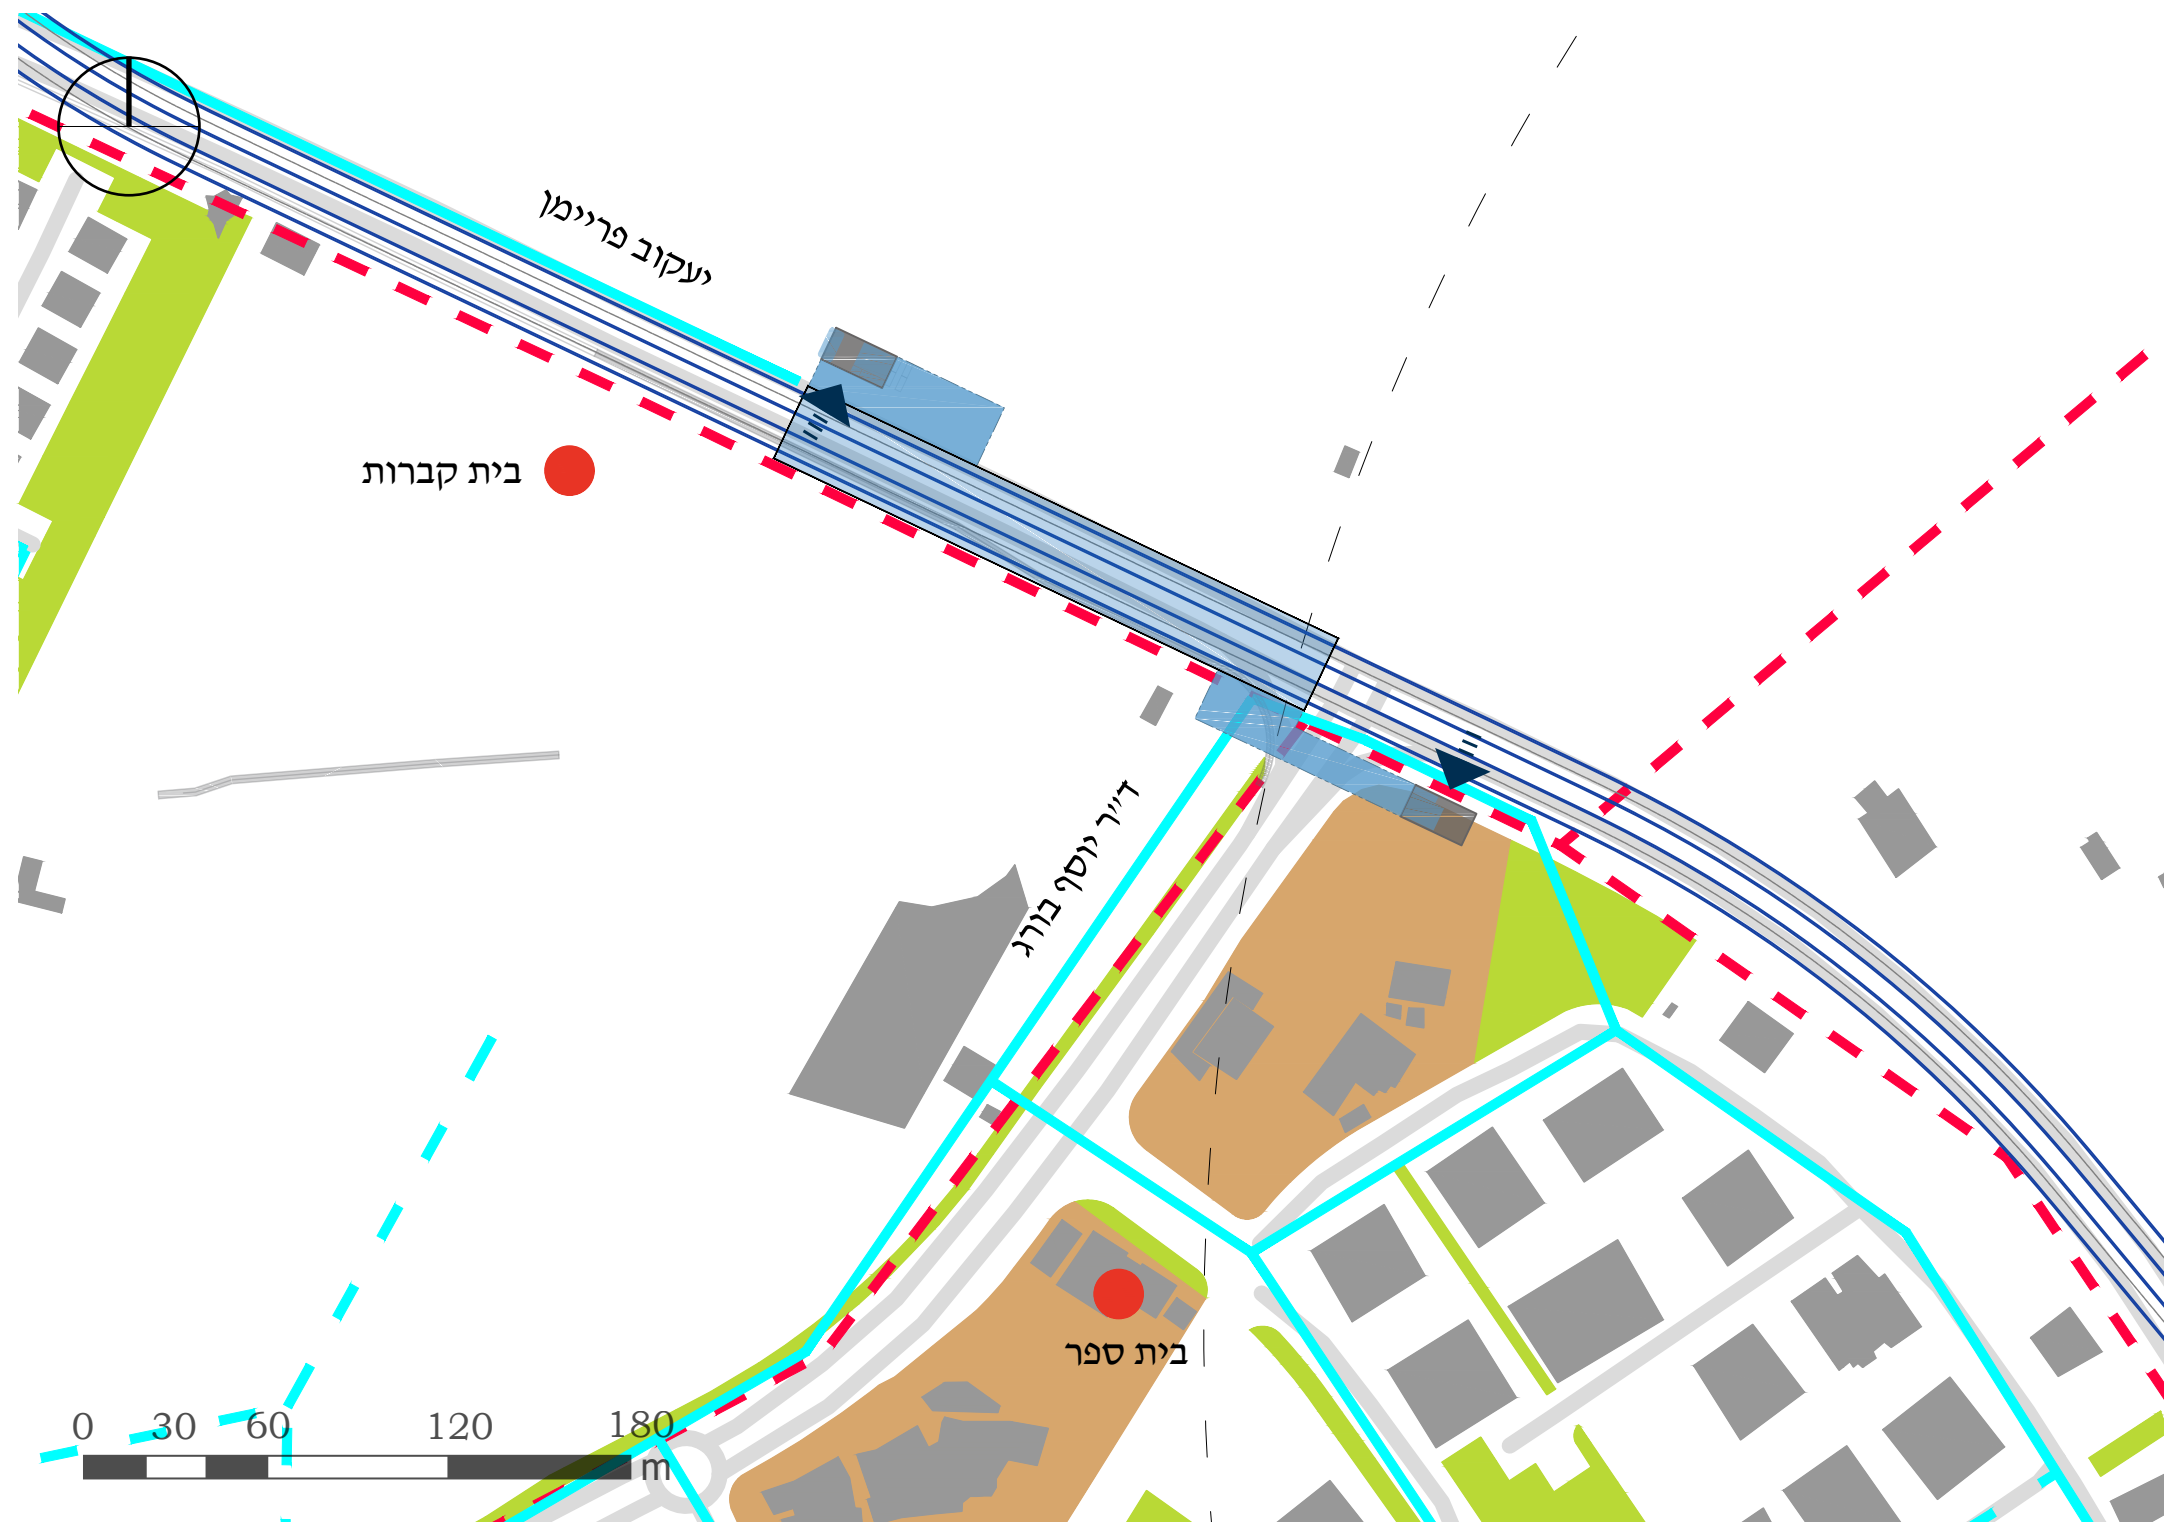

מצב מאושר
תחנה מס' 37 | יוסף בורג

ייעודי קרקע
מאושרים

- שטח חקלאי
- דרך מאושרת
- שטח ציבורי פתוח
- מבנים ומוסדות ציבור
- בית קברות

כניסה לתחנה

תחנת מטרו תת"ק

מעברים תת קרקעיים




M1S

ת. יוסף בורג

תכניות מאושרות

1:1250




175

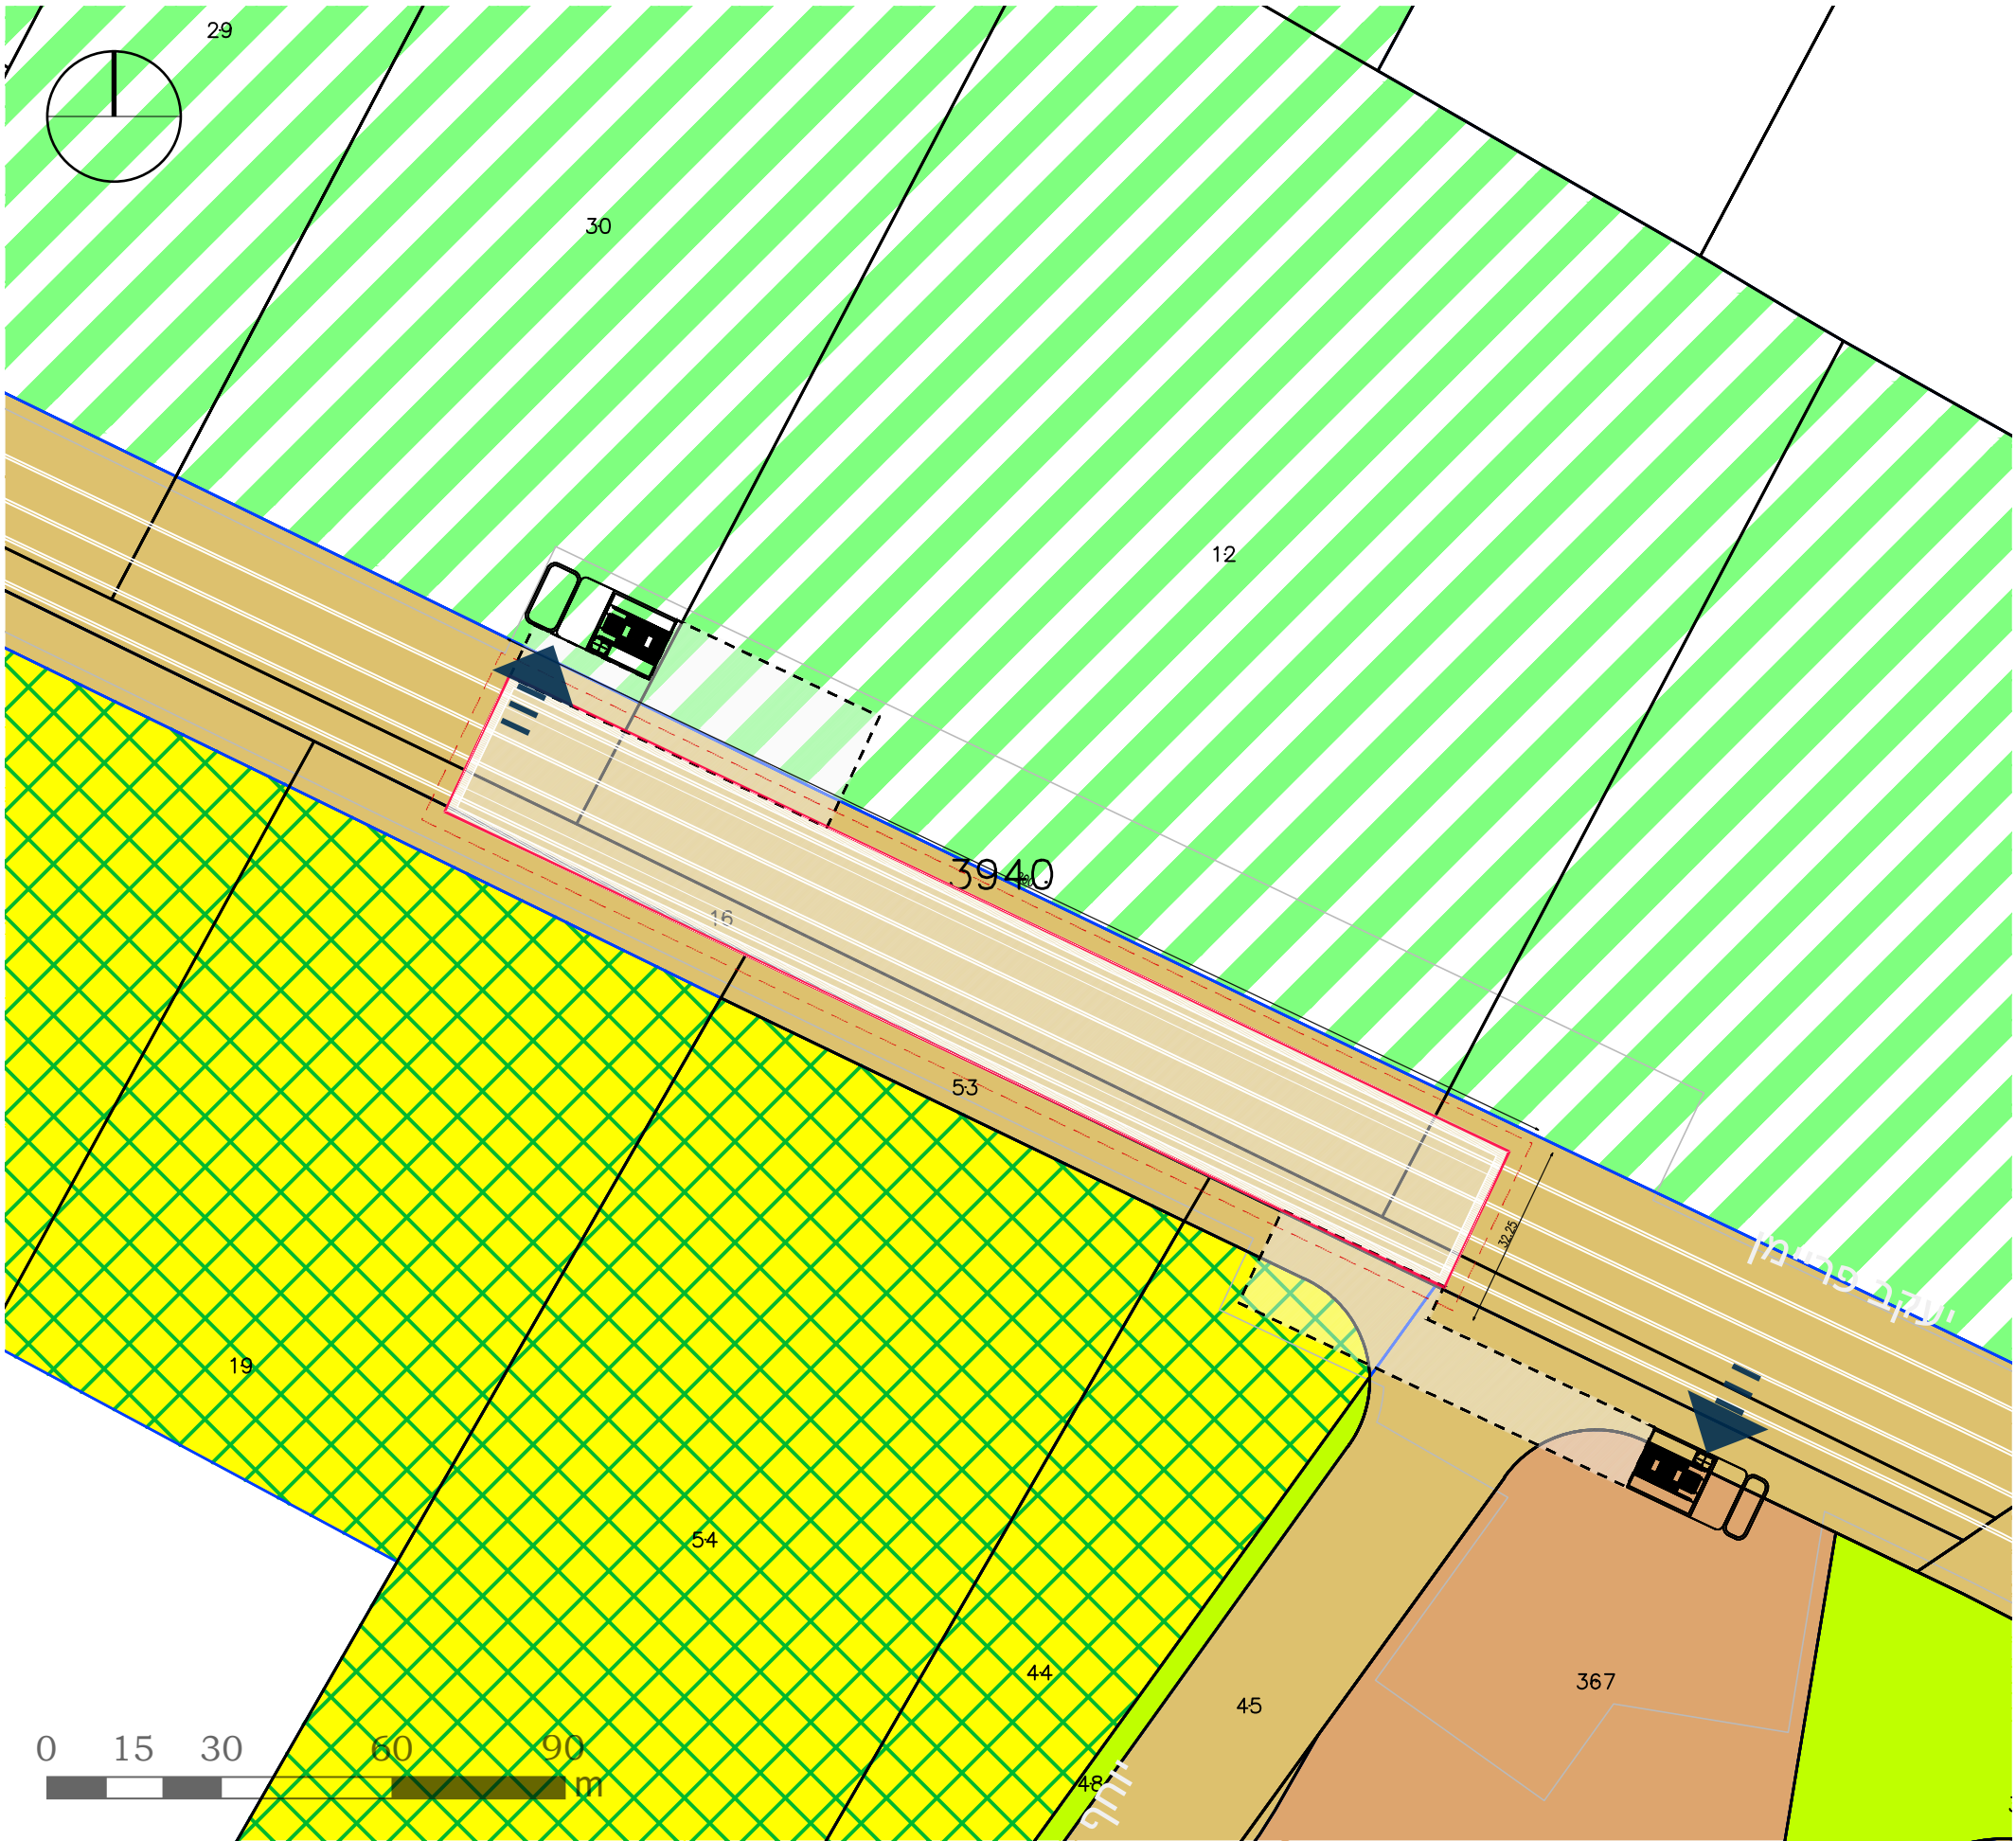






השתלבות במערך הסביבתי


תחנה מס' 37 | יוסף בורג

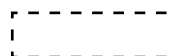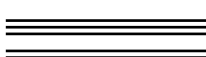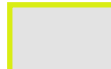-  עץ קיים
-  עץ מתוכנן
-  גיזון
-  מדרכה
-  זכות הדרך
-  תחנת מטרו תת"ק
-  מעברים תת קרקעיים
-  תוואי מטרו
-  כניסה לתחנה
-  מבנה להריסה
-  תחנת אוטובוס

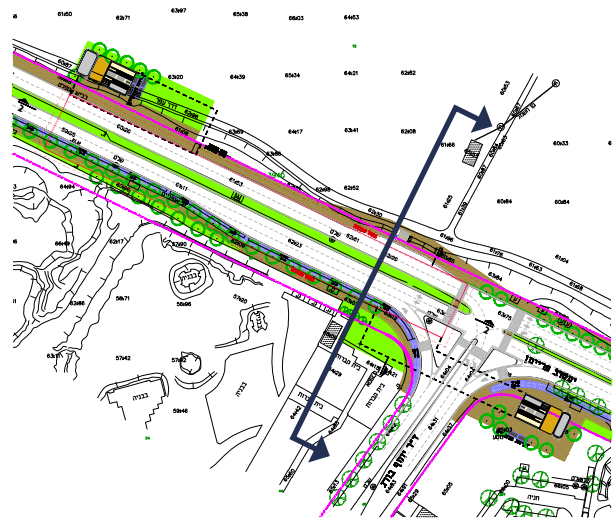

חתך רוחב
תחנה מסי' 37 | יוסף בורג

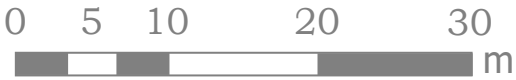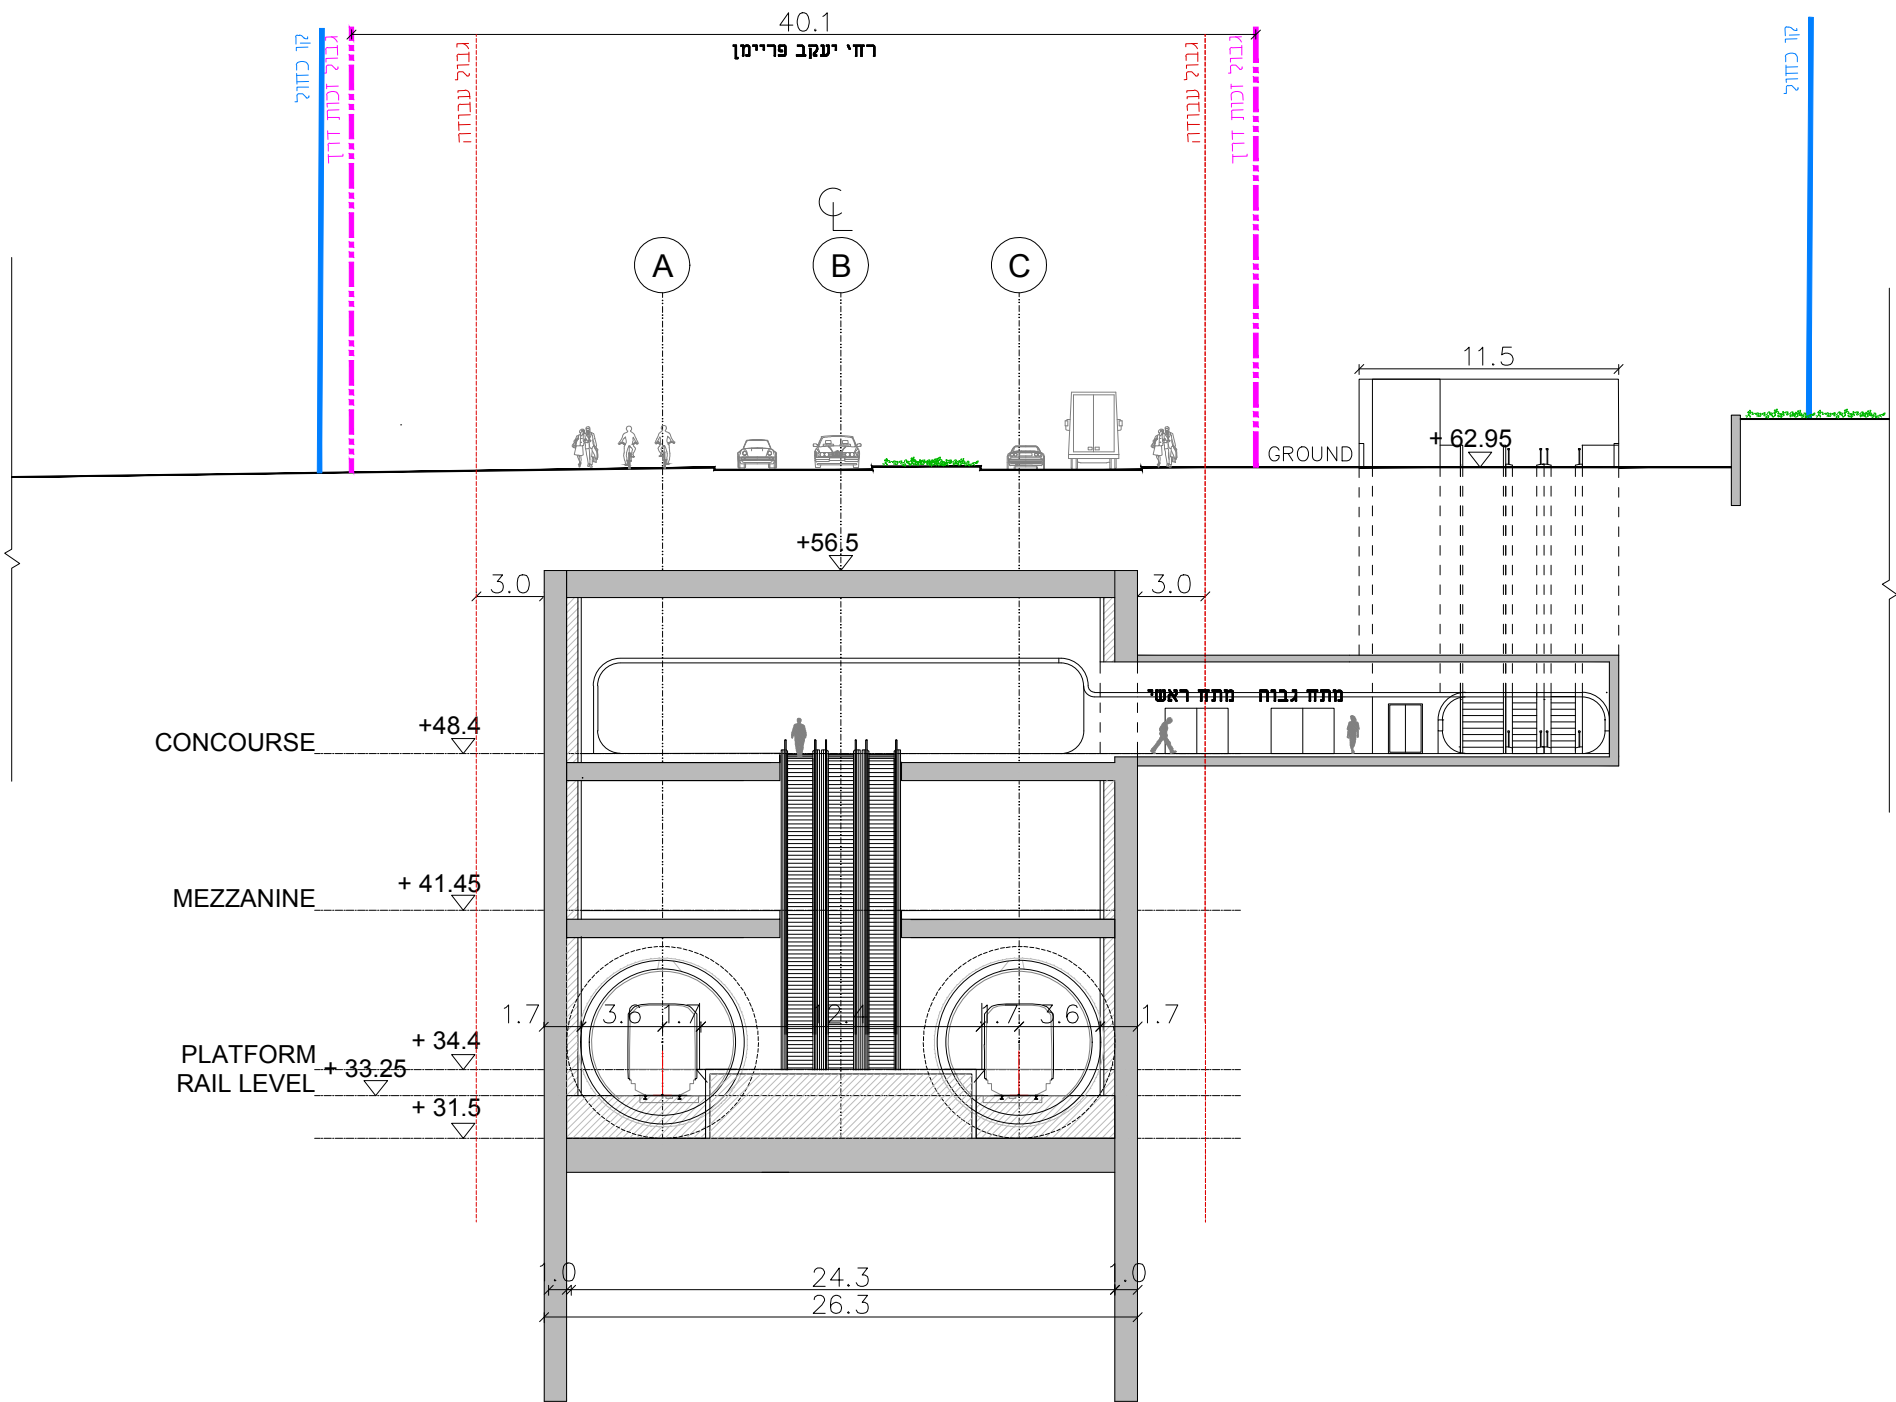

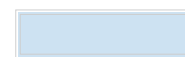

תחנת מטרו תת"ק




כניסה לתחנה

מסקנות והמלצות

תחנה מס' 37 | יוסף בורג

1. התחנה ממוקמת על דרך פריימן, מצפון לשכונות מגורים חדשות. מצפון לתחנה שטחים חקלאיים, שעתידיים להיות מפותחים כשכונת מגורים.
2. מתוכננות שתי כניסות. כניסה צפון-מערבית שתשרת את הפיתוח העתידי של האני"מ, וכניסה דרום-מזרחית, בסמוך לרחוב הכניסה לשכונות מדרום.
3. בעתיד ניתן יהיה להתחבר לתחנה עם כניסה נוספת מצפון מזרח, בהתאם לתכנית הפיתוח של האני"מ.

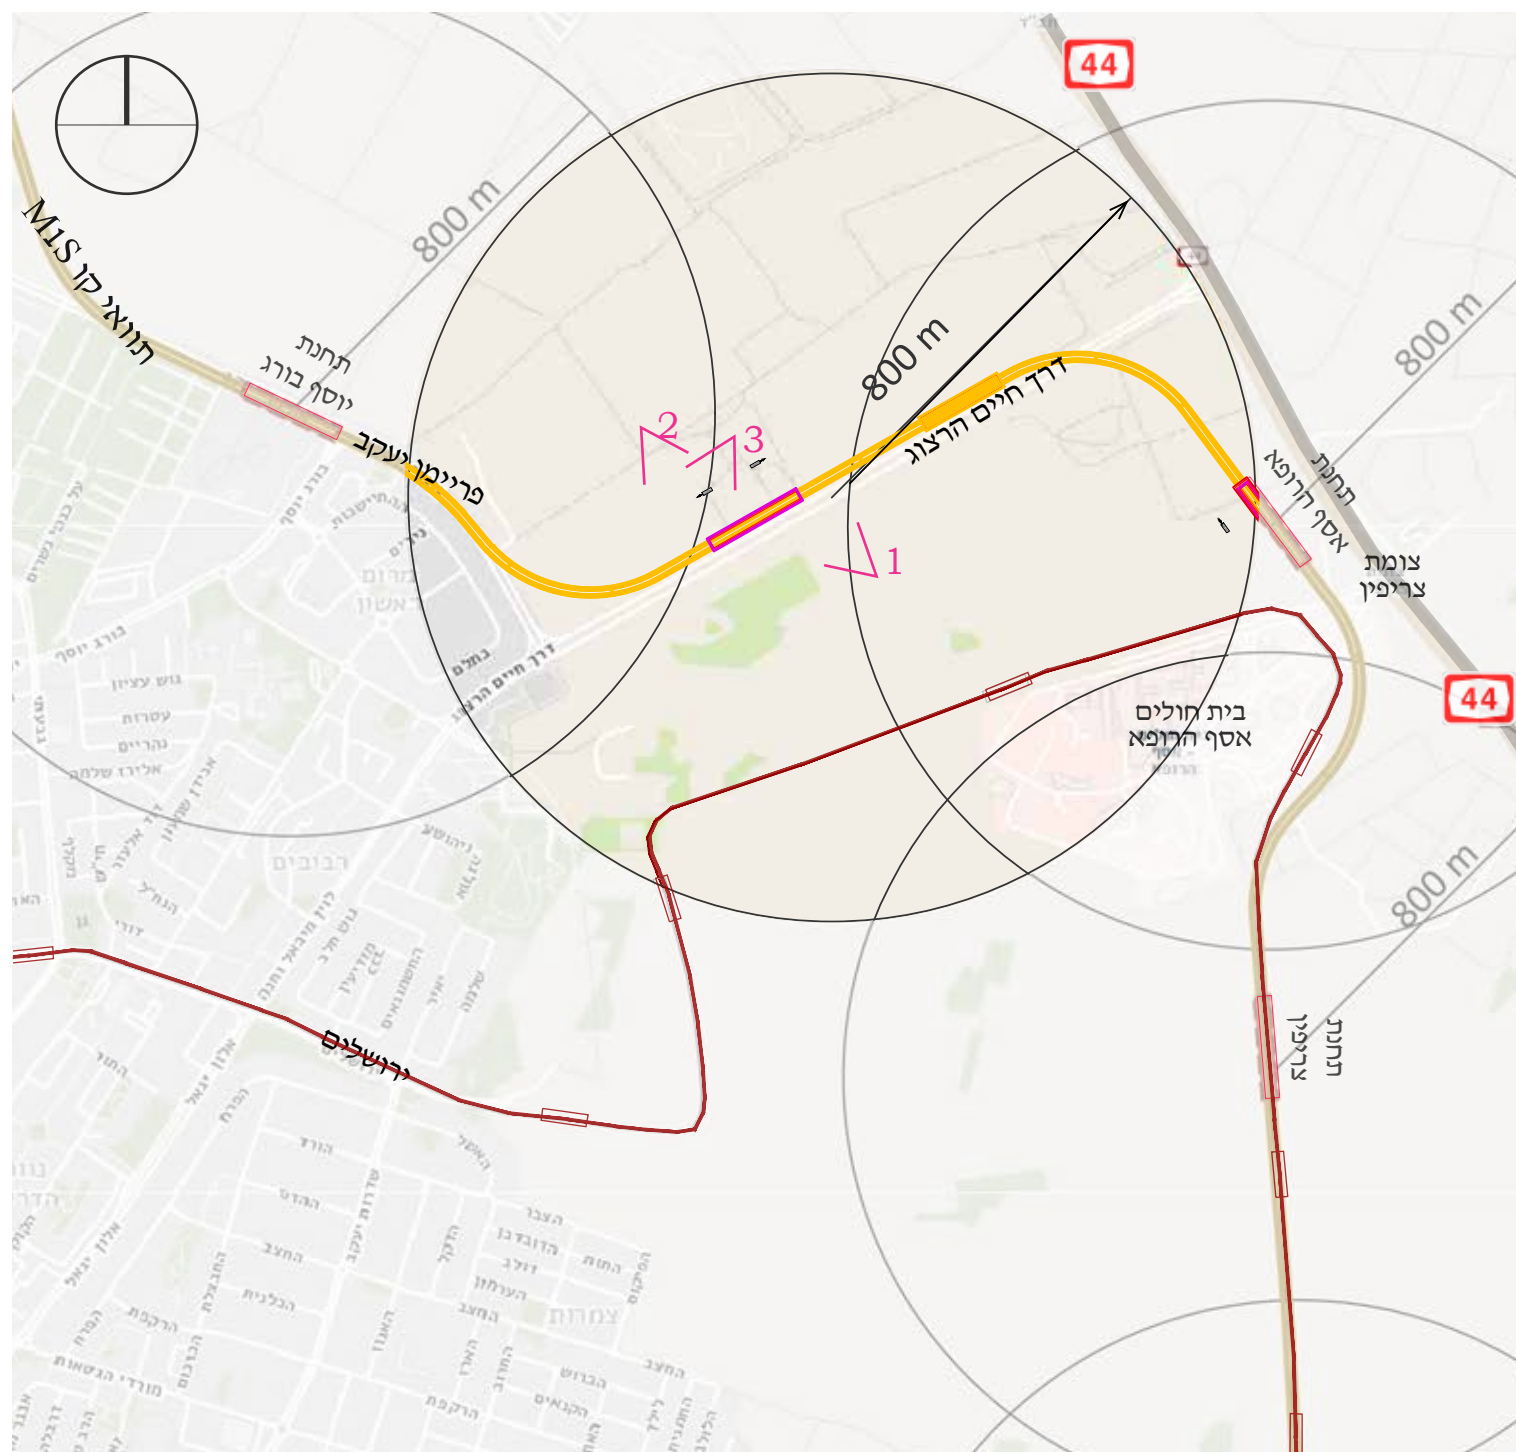

תחנה מס' 38 | הרצוג

- | | |
|--|--|
| <p>ראשון לציון, התחנה ממוקמת צפונית לרחוב הרצוג, ממערב למחלף המקשר אל כביש 44.
מצפון שטחים חקלאיים.
מדרום תחמ"ש של חברת חשמל ומחנה צריפין.
ממזרח לתחנה כביש 44 הראשי.</p> | <p>מיקום התחנה</p> |
| <p>תחנה רגילה</p> | <p>סוג תחנה</p> |
| <p>מצפון שטחים חקלאיים - באיזור זה תכנית בהכנה אנ"מ צפוני - רצ/130, רצ/130 - אזור נופש מטרופוליני.
מתוכננים- 1,500 יח"ד.</p> <p>מדרום - פיתוח מתחמי מגורים בתחום מחנה צריפין המתפנה:
מתחם 5 - רצ/151 מתוכנן- 4050 יח"ד, מבנים ומוסדות ציבור, מסחר ושטחים פתוחים.
מתחם 6 - מתוכנן- 170,000 מ"ר תעסוקה ו15,000 דוור מיוחד (בתי אבות ודוור לבעלי צרכים מיוחדים). התכנית בהפקדה.</p> | <p>אפיון פיסי סביבת התחנה</p> |
| <p>שבילי הולכי רגל מתוכננים בתכניות עתידיות. שביל אופניים קיים (מזרח מערב) בתוואי המטרו על דרך חיים הרצוג.</p> | <p>קישוריות ונגישות</p> |
| <p>תחזית נוסעים לשנת 2040 צופה כ- 300 נוסעים עולים ויורדים בשעת שיא.</p> | <p>קיבולת נוסעים צפויה</p> |
| <p>פיתוח איזורים לשטחים פתוחים מצפון ולמגורים ממערב.</p> | <p>היבטים נוספים</p> |

1. מבט מכיוון דרום
2. מבט מכיוון צפון
3. מבט מערבה