


סביבת התחנה:

מיפוי אגן

היקוות התחנה

תחנה מס' 39 | אסף הרופא

רדיוס שירות

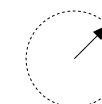

תוואי מטר



תחנת מטר



הקו החום



עוגן ציבורי ברדיוס 800m



ציר עירוני ראשי - וקטור ביקוש



ציר עירוני - וקטור ביקוש



שביל אופניים קיים



שביל אופניים מתוכנן



ציר הולכי רגל ראשי



ציר הולכי רגל מתוכנן



M1S


ת. אסף הרופא

סביבת התחנה

1:7500

189



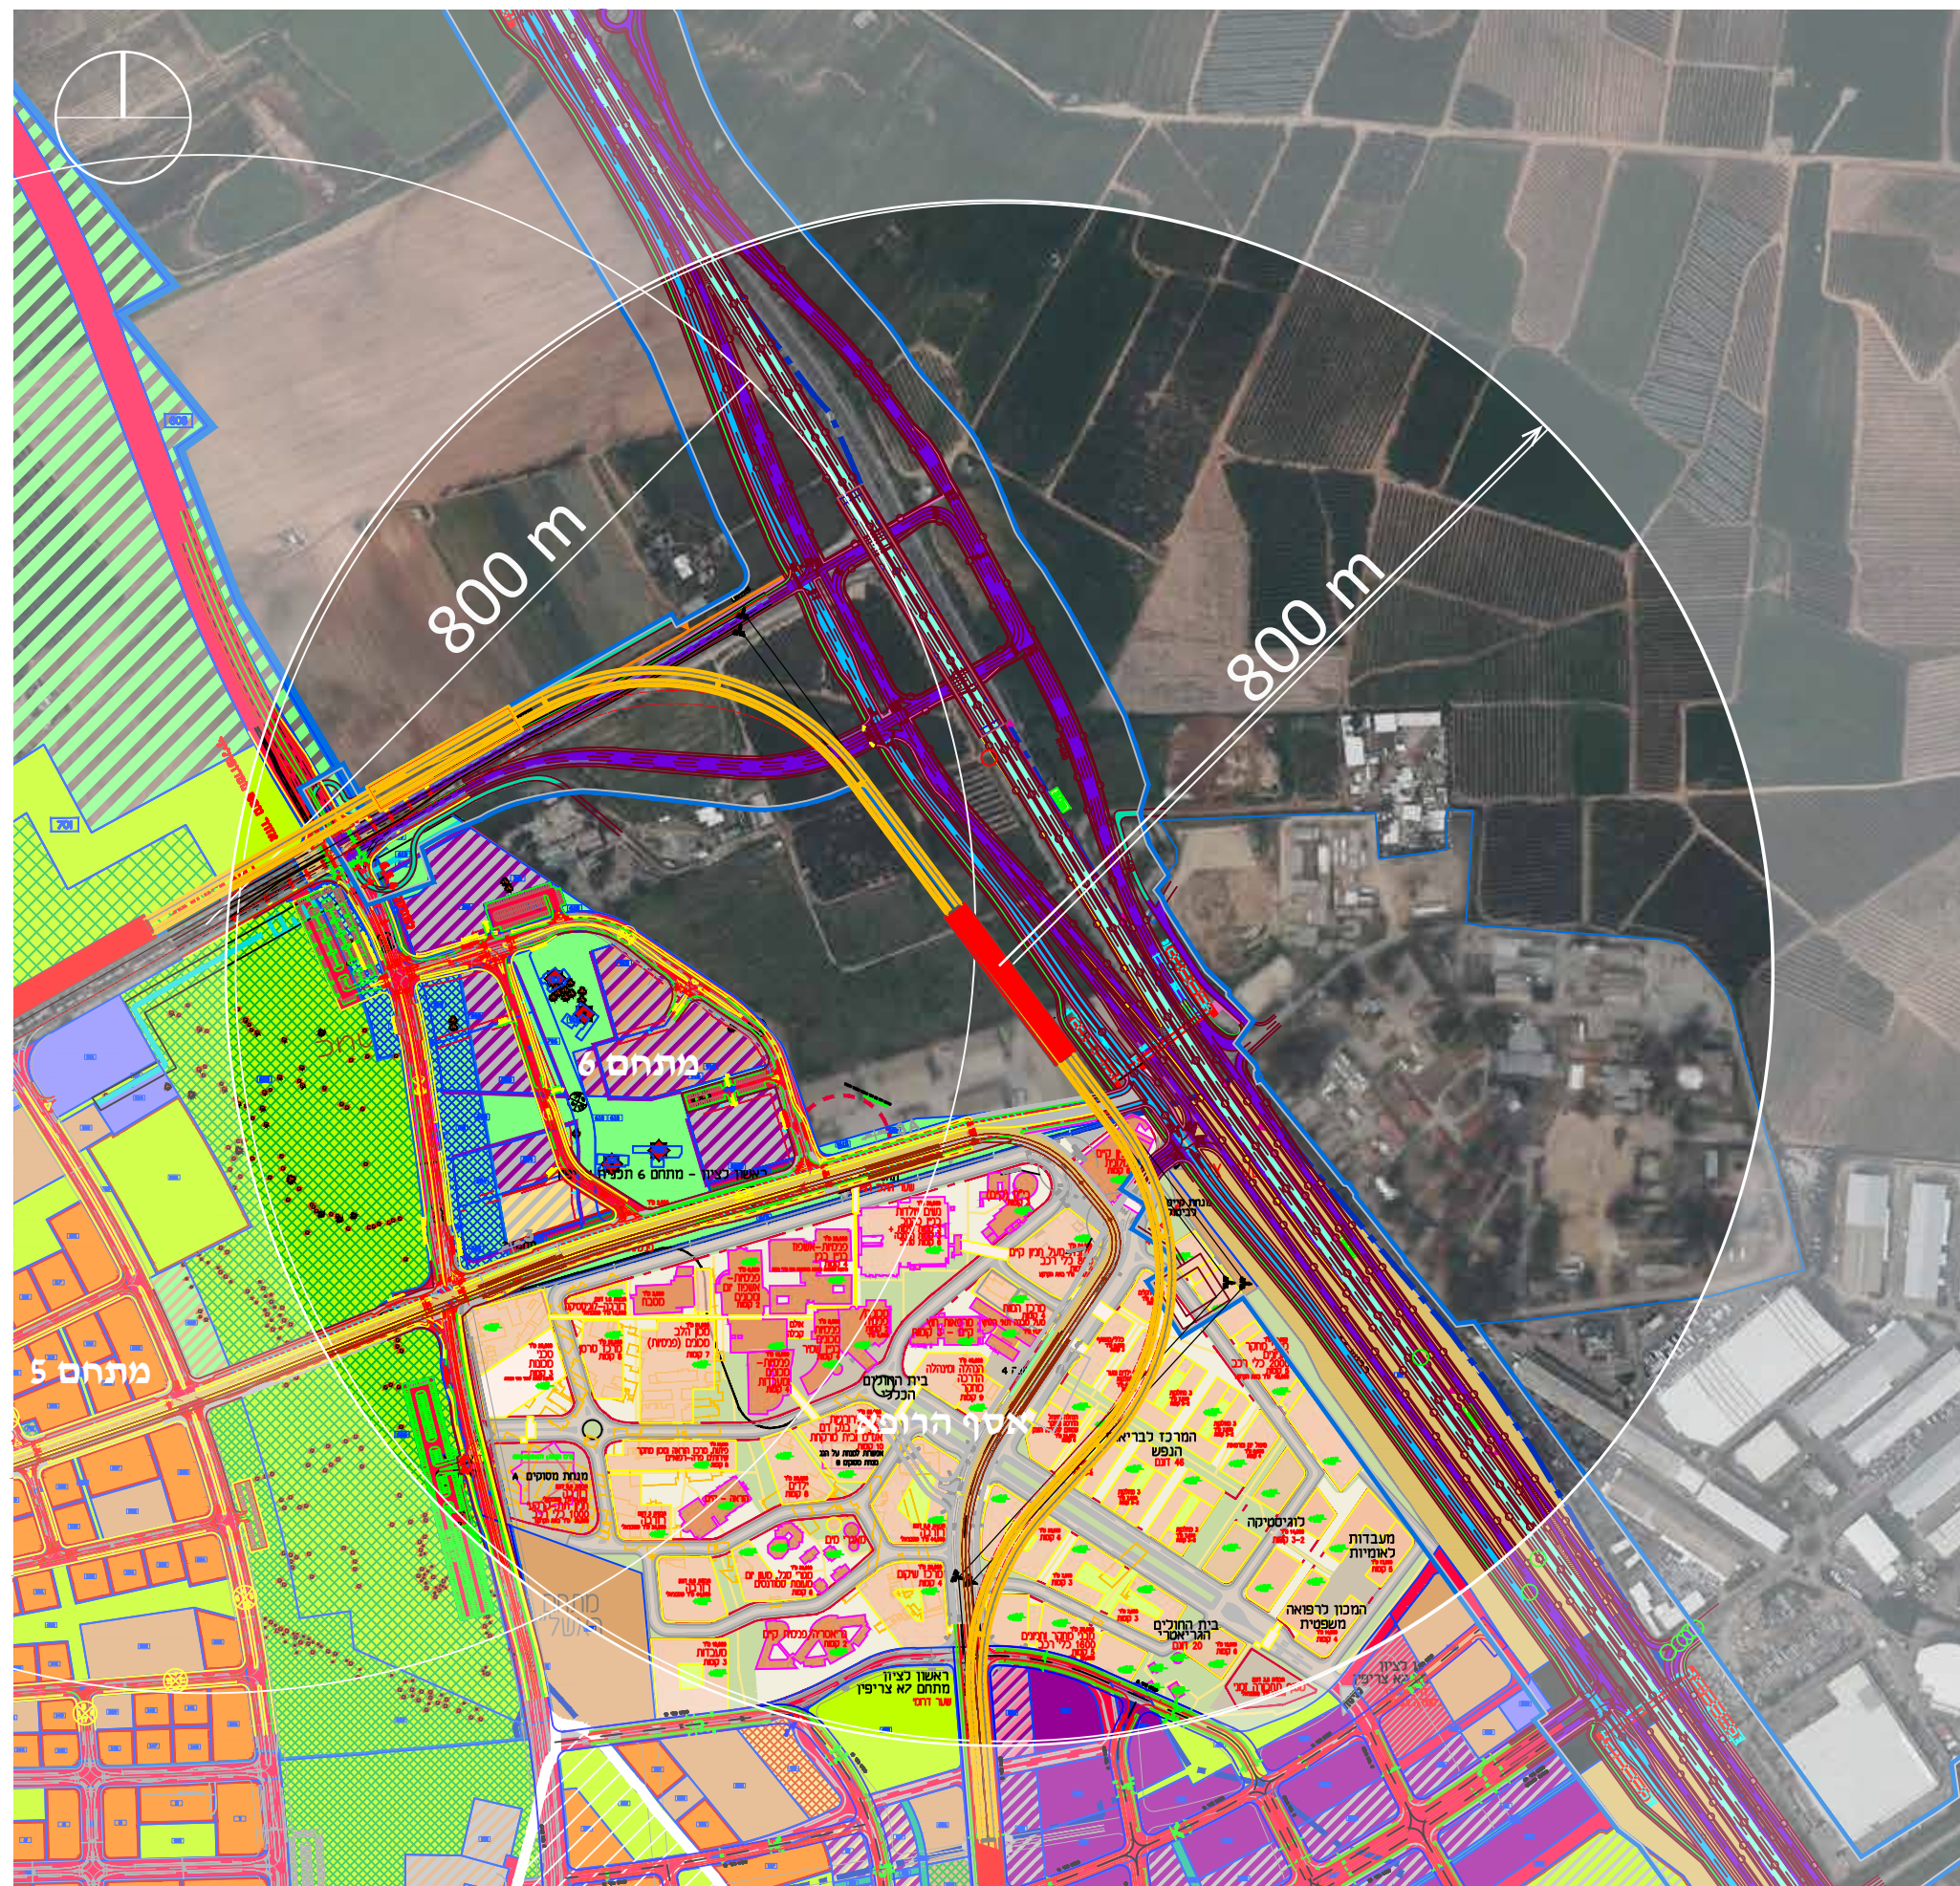

תכניות בהכנה

תחנה מסי 39 | אסף הרופא

תכניות בהכנה בסביבת התחנה

שם התכנית : אסף הרופא - 455
0631754
בתכנון : קולקר אדריכלים
סטטוס : החלטת הפקדה
מתוכנן : 1.1 מיליון מ"ר עבור
שירותים רפואיים .

שם התכנית : מתחם 6 -
בתכנון : מאיר בוכמן.
סטטוס : הפקדה.
מתוכנן : רובע תעסוקה חדש עם
משרדים, מסחר, מבני ציבור ודוור
מיוחד
(בתי אבות ודוור לבעלי צרכים
מיוחדים).


שם התכנית : כביש 44
בתכנון : P.G.L הנדסה
סטטוס : בתכנון
מתוכנן : מחלף חדש

רדיוס שירות

תוואי מטר

תחנת מטר

הקו החום

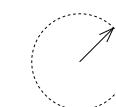

מפת ייעודי קרקע

תחנה מס' 39 | אסוף הרופא


ייעודי קרקע
מתכנית המתאר

- תעסוקה
- דרך מוצעת
- דרך מאושרת



תחנת מטרו

- תוואי מטרו
- תחנת מטרו תת"ק
- מעברים תת קרקעיים
- מבנה כניסה לתחנה

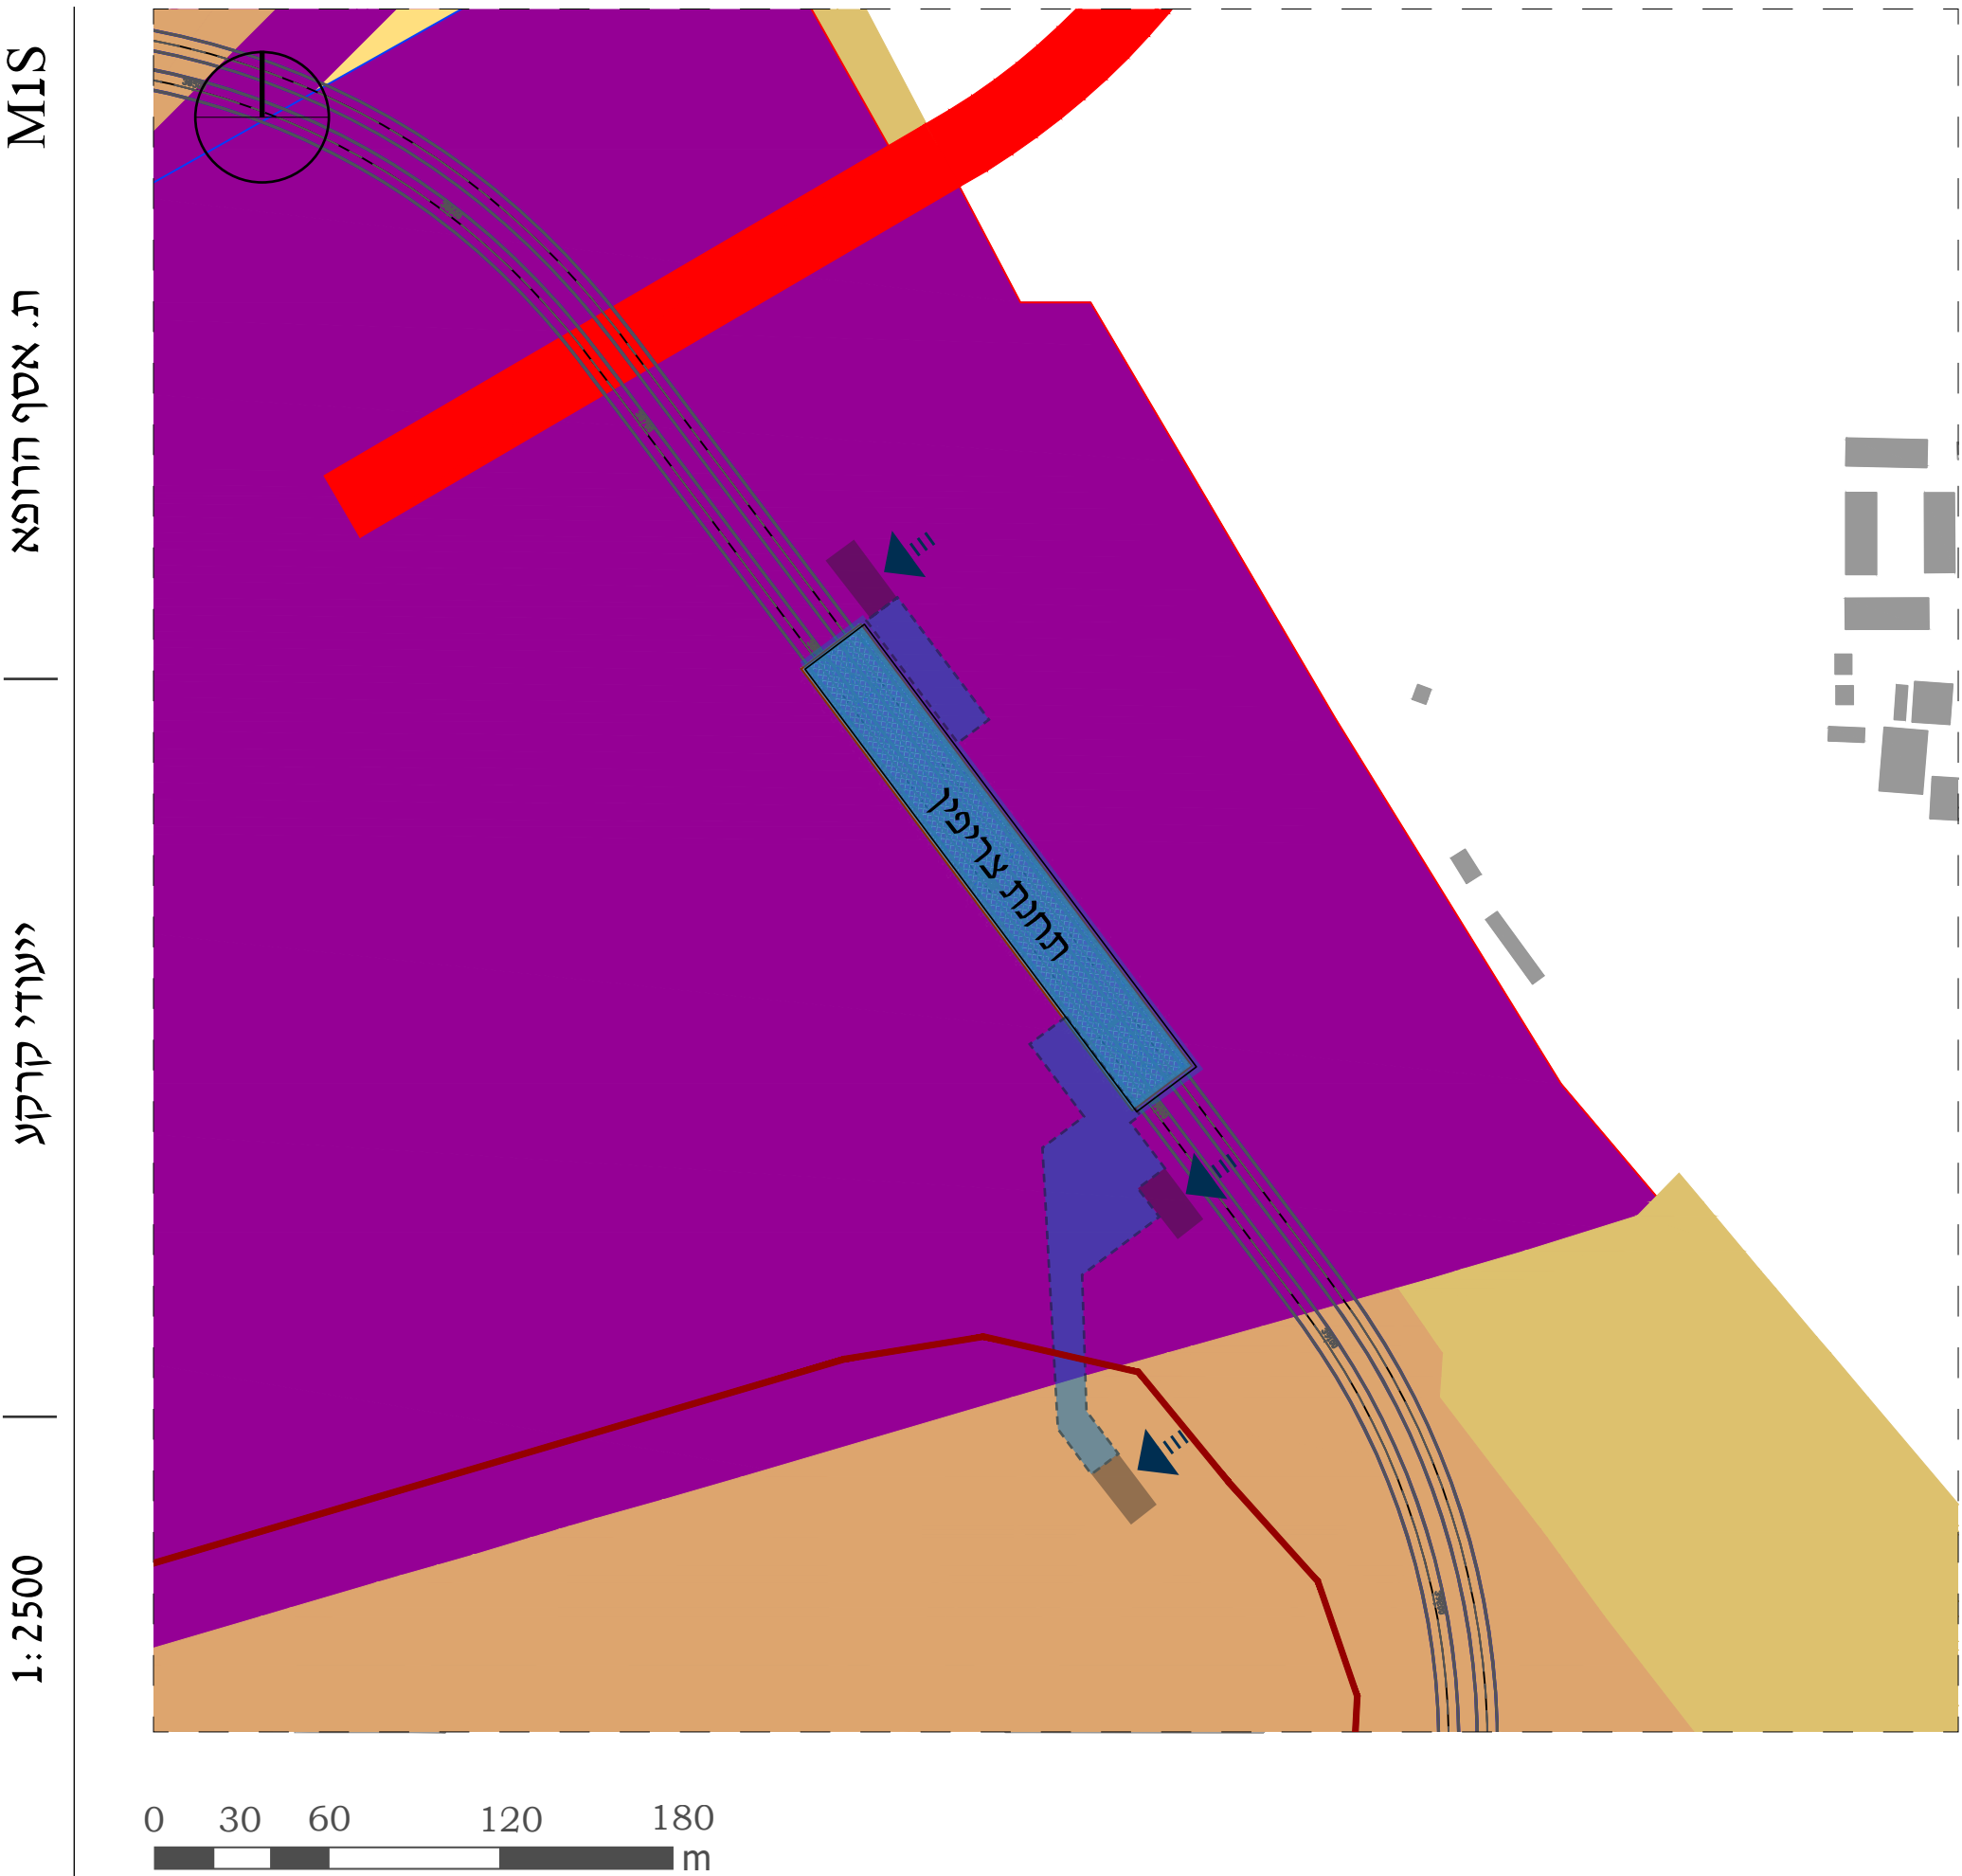

המרחב הציבורי

תחנה מס' 39 | אסף הרופא

תחנת מטרו

- תוואי מטרו
- תחנת מטרו תת"ק
- מעברים תת קרקעיים
- מבנה כניסה לתחנה
- כניסה לתחנה
- מבנים
- שצ"פ סטטוטורי
- מבנים ומוסדות
ציבור סטטוטוריים
- הקו החום
- שביל אופניים קיים
- שביל אופניים מתוכנן
- ציר הולכי רגל ראשי
- ציר הולכי רגל משני

פיתוח קיים ומתוכנן


התחנה ממוקמת בסמוך לכביש 44 ובכניסה לאסף הרופא. בכביש 44, 4 נתיבי תנועה מופרדים באי תנועה. התחנה מצפון לאזורים המיועדים לבניה בבית החולים. לביה"ח מקודמת תכנית לעיבוי פנימי והרחבה.

עוגנים למיקום התחנה והכניסות

התחנה ממוקמת בסמוך לכניסה לבית החולים אסף הרופא ובצמוד לכביש 44 שבו מתוכנן נת"צ. מתוכננות שלוש כניסות: כניסה צפונית, כניסה עתידית שתשרת פיתוח עתידי מצפון-מערב. שרוול דרומי, המפוצל לשתי כניסות: כניסה אחת צמודה לתחנה, משרתת את הבסיס הצבאי ממערב, את בסיס גדעונים ממזרח ואת תחנות האוטובוס על כביש 44. המעבר לתחנות האוטובוס ולבסיס ממזרח לכביש דרך גשר הולכי הרגל. מכניסה זו יבוצע שרוול תת-קרקעי אל תוך תחום בית החולים, עם יציאה בסמוך למבנה בית ספר הקיים. כמו כן, תחנת הקו החום מתוכננת 140 מ' מדרום. לכניסה.

קישוריות ונגישות


קישוריות לתחנת הקו החום ממזרח לתחנה דרך הליכה במפלס הרחוב ללא מעבר כביש. נגישות להולכי רגל במערך השבילים הקיימים אל ובתוך אסף הרופא. שבילי אופניים מתוכננים בסביבת התחנה לפי תוכניות בינוי עתידיות של בית החולים והתוכנית החדשה של משרד התחבורה ומחוז מרכז לשבילי אופניים.

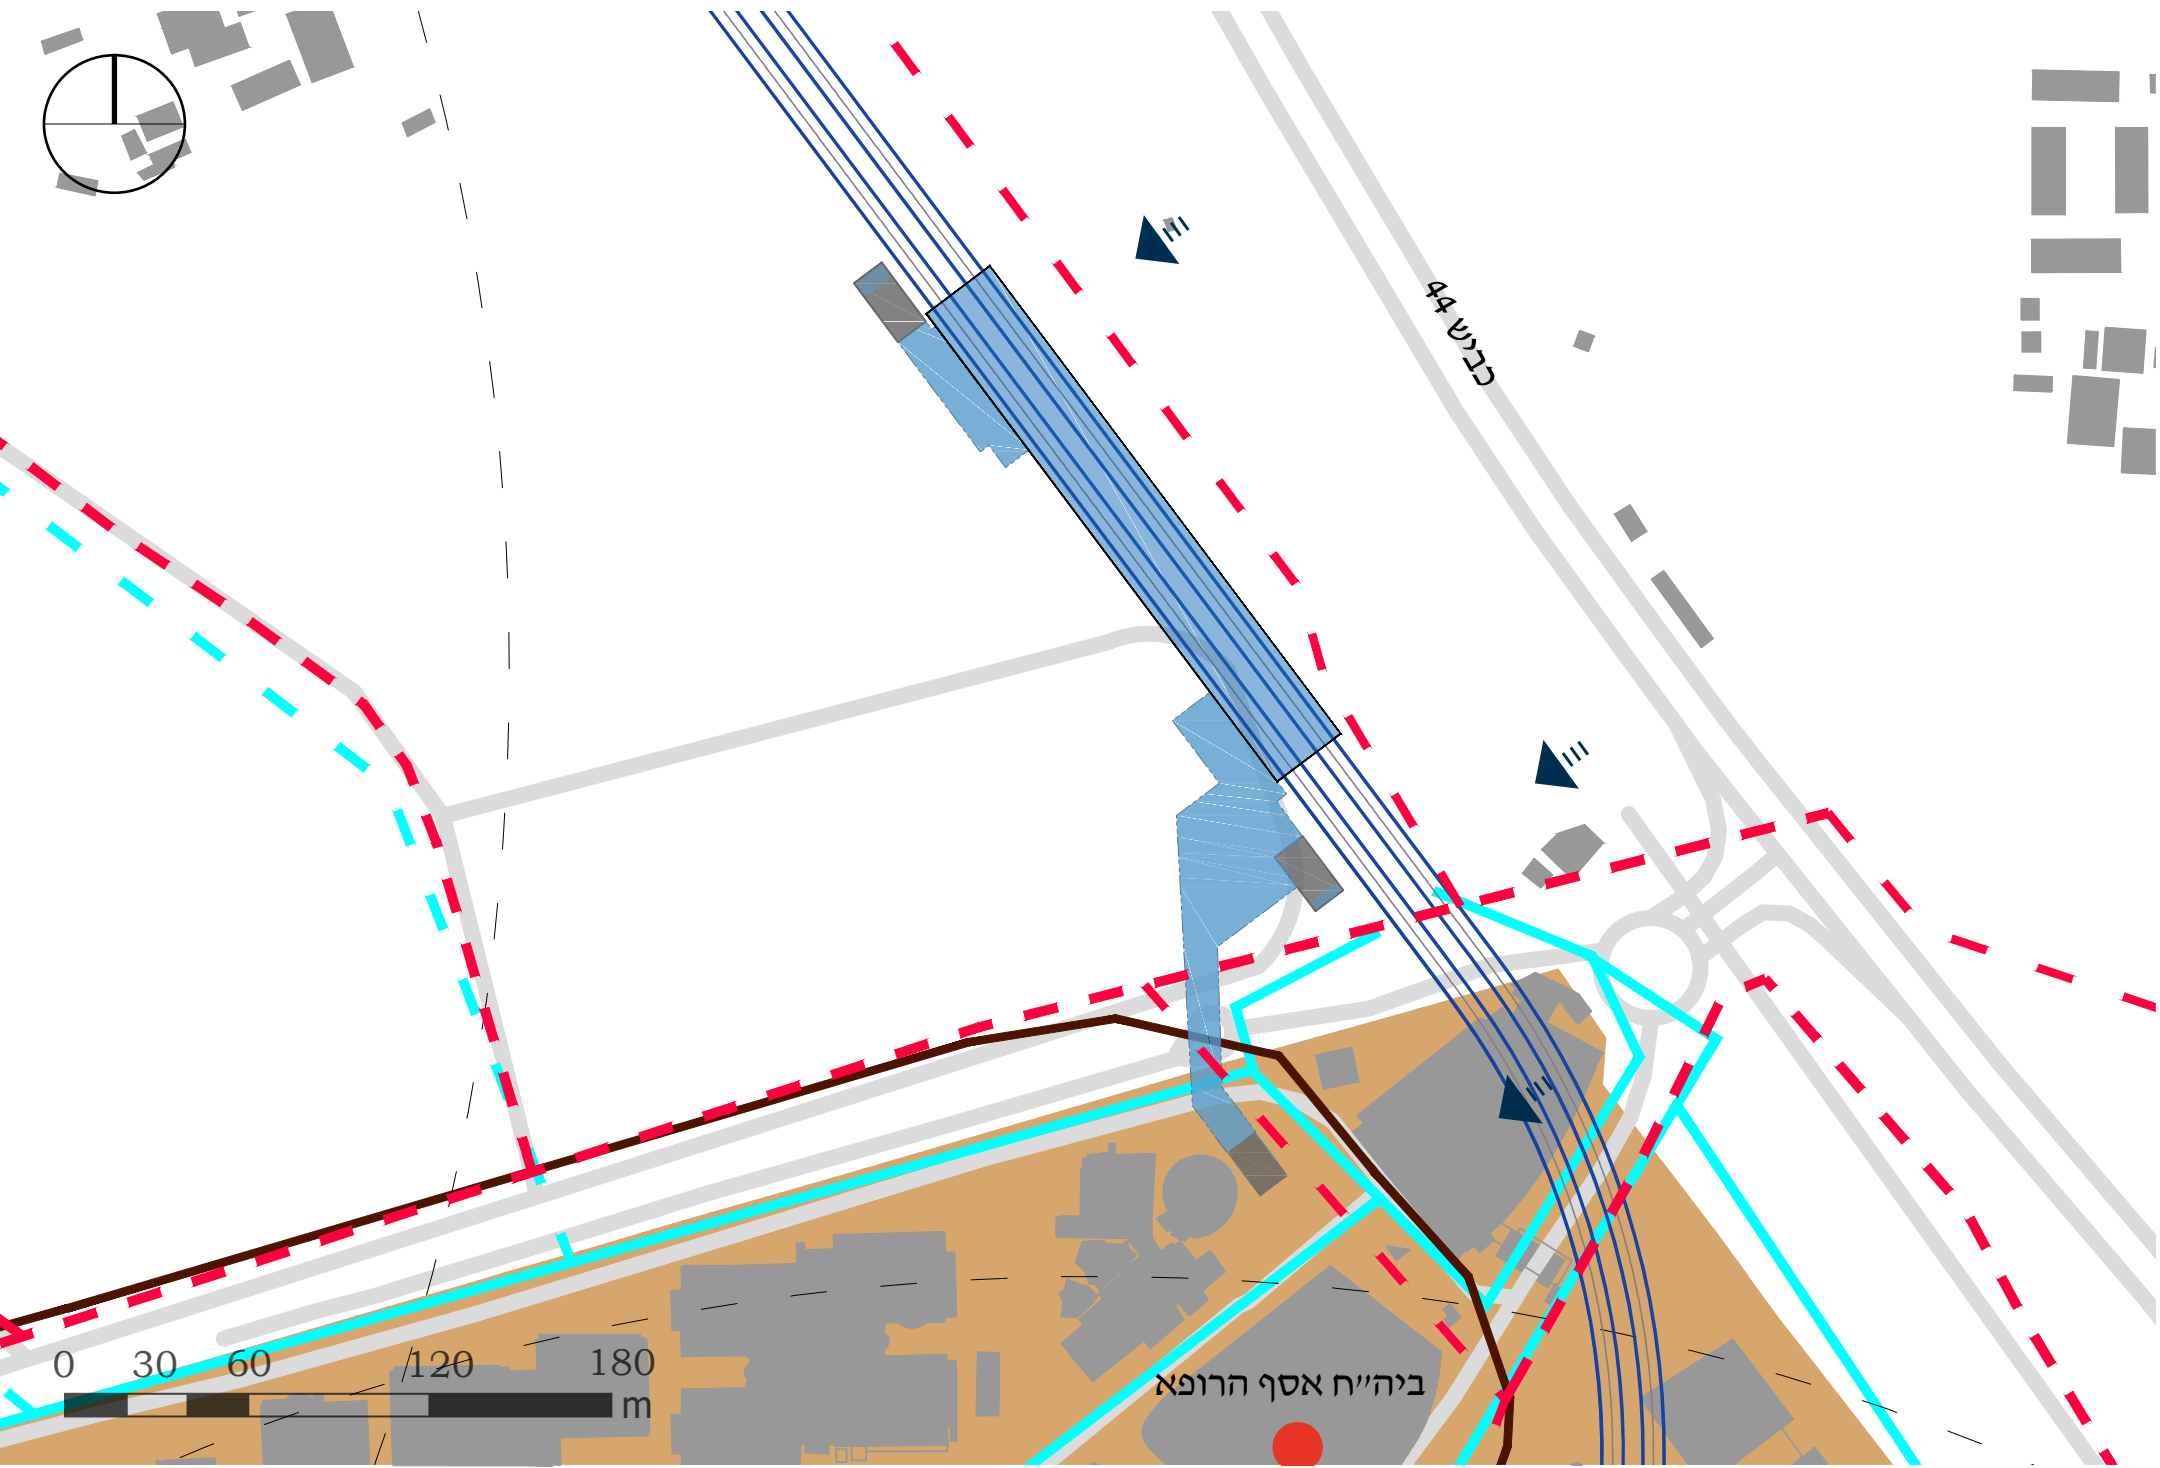

מצב מאושר
תחנה מס' 39 | אסף הרופא

ייעודי קרקע
מאושרים

- תחנת דלק
- שטח למבני ציבור
- דרך מאושרת
- שטח חקלאי
- מגבלות בניה
- תחום מחלף עתידי
- תעשייה
- רצועת מתע"ן
ע"פ תכנית בהכנה
- שטח ציבורי פתוח

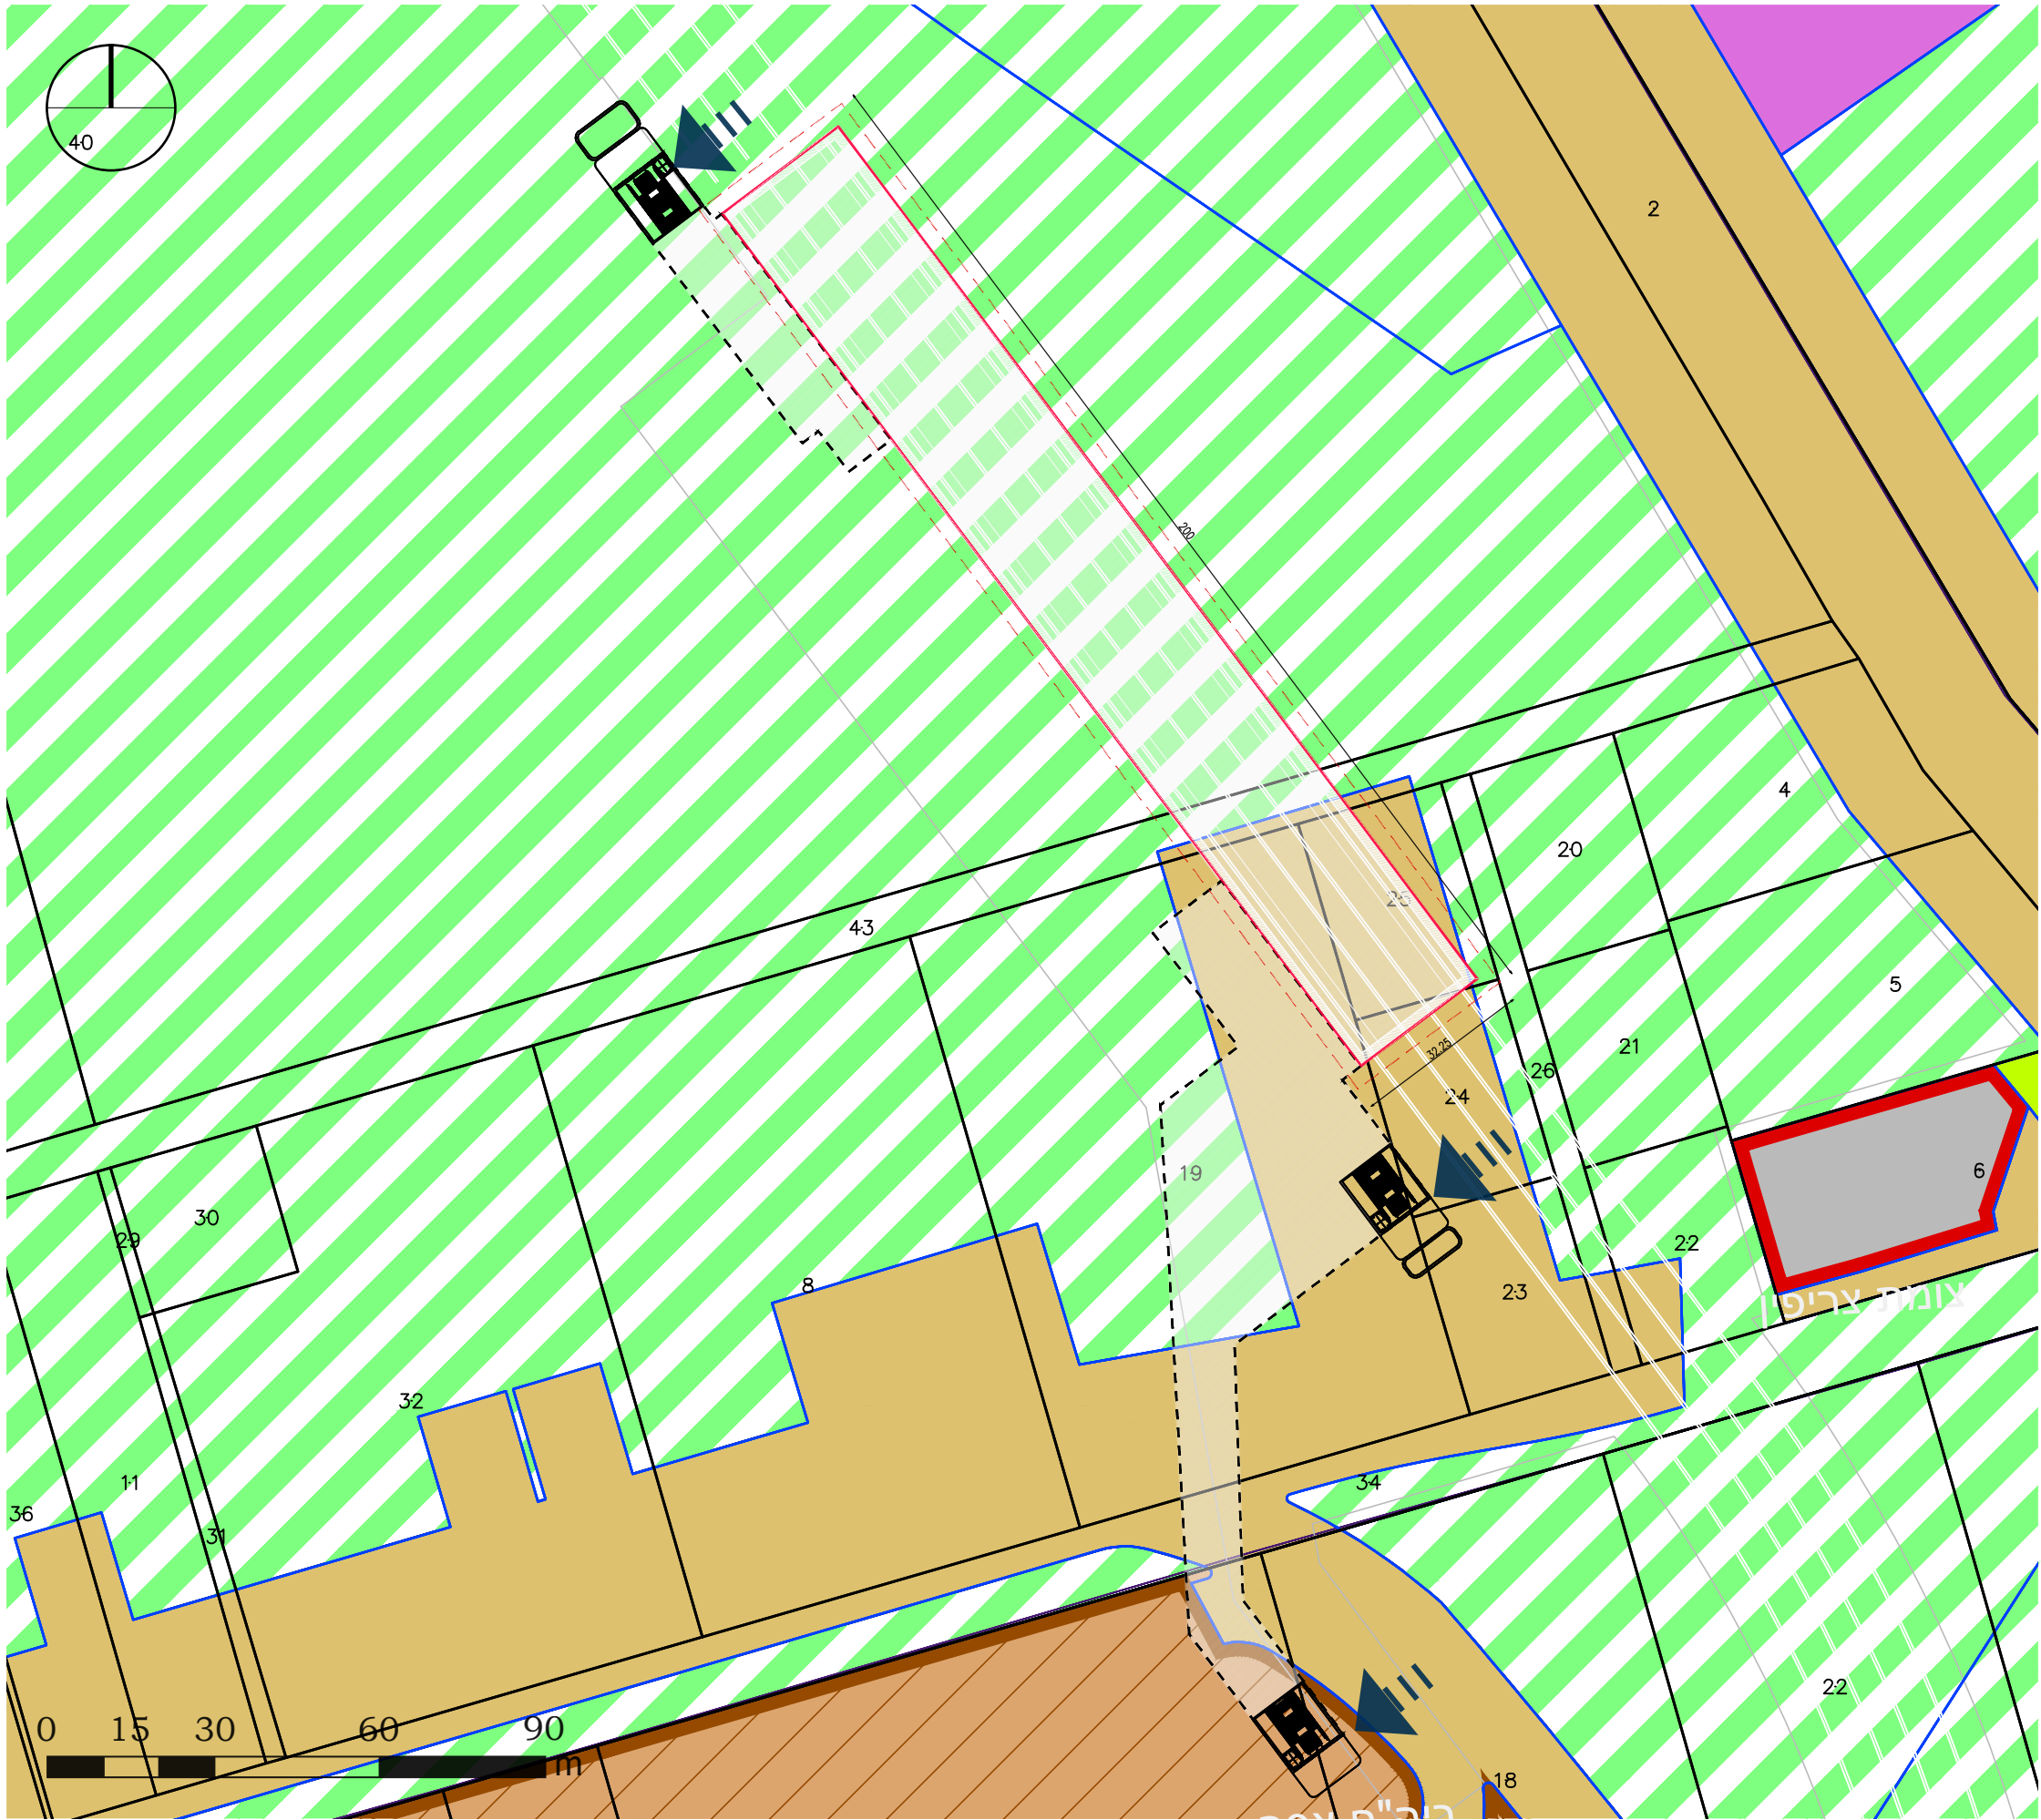


M1S


ת. אסף הרופא

תכניות מאושרות


1:1250


193

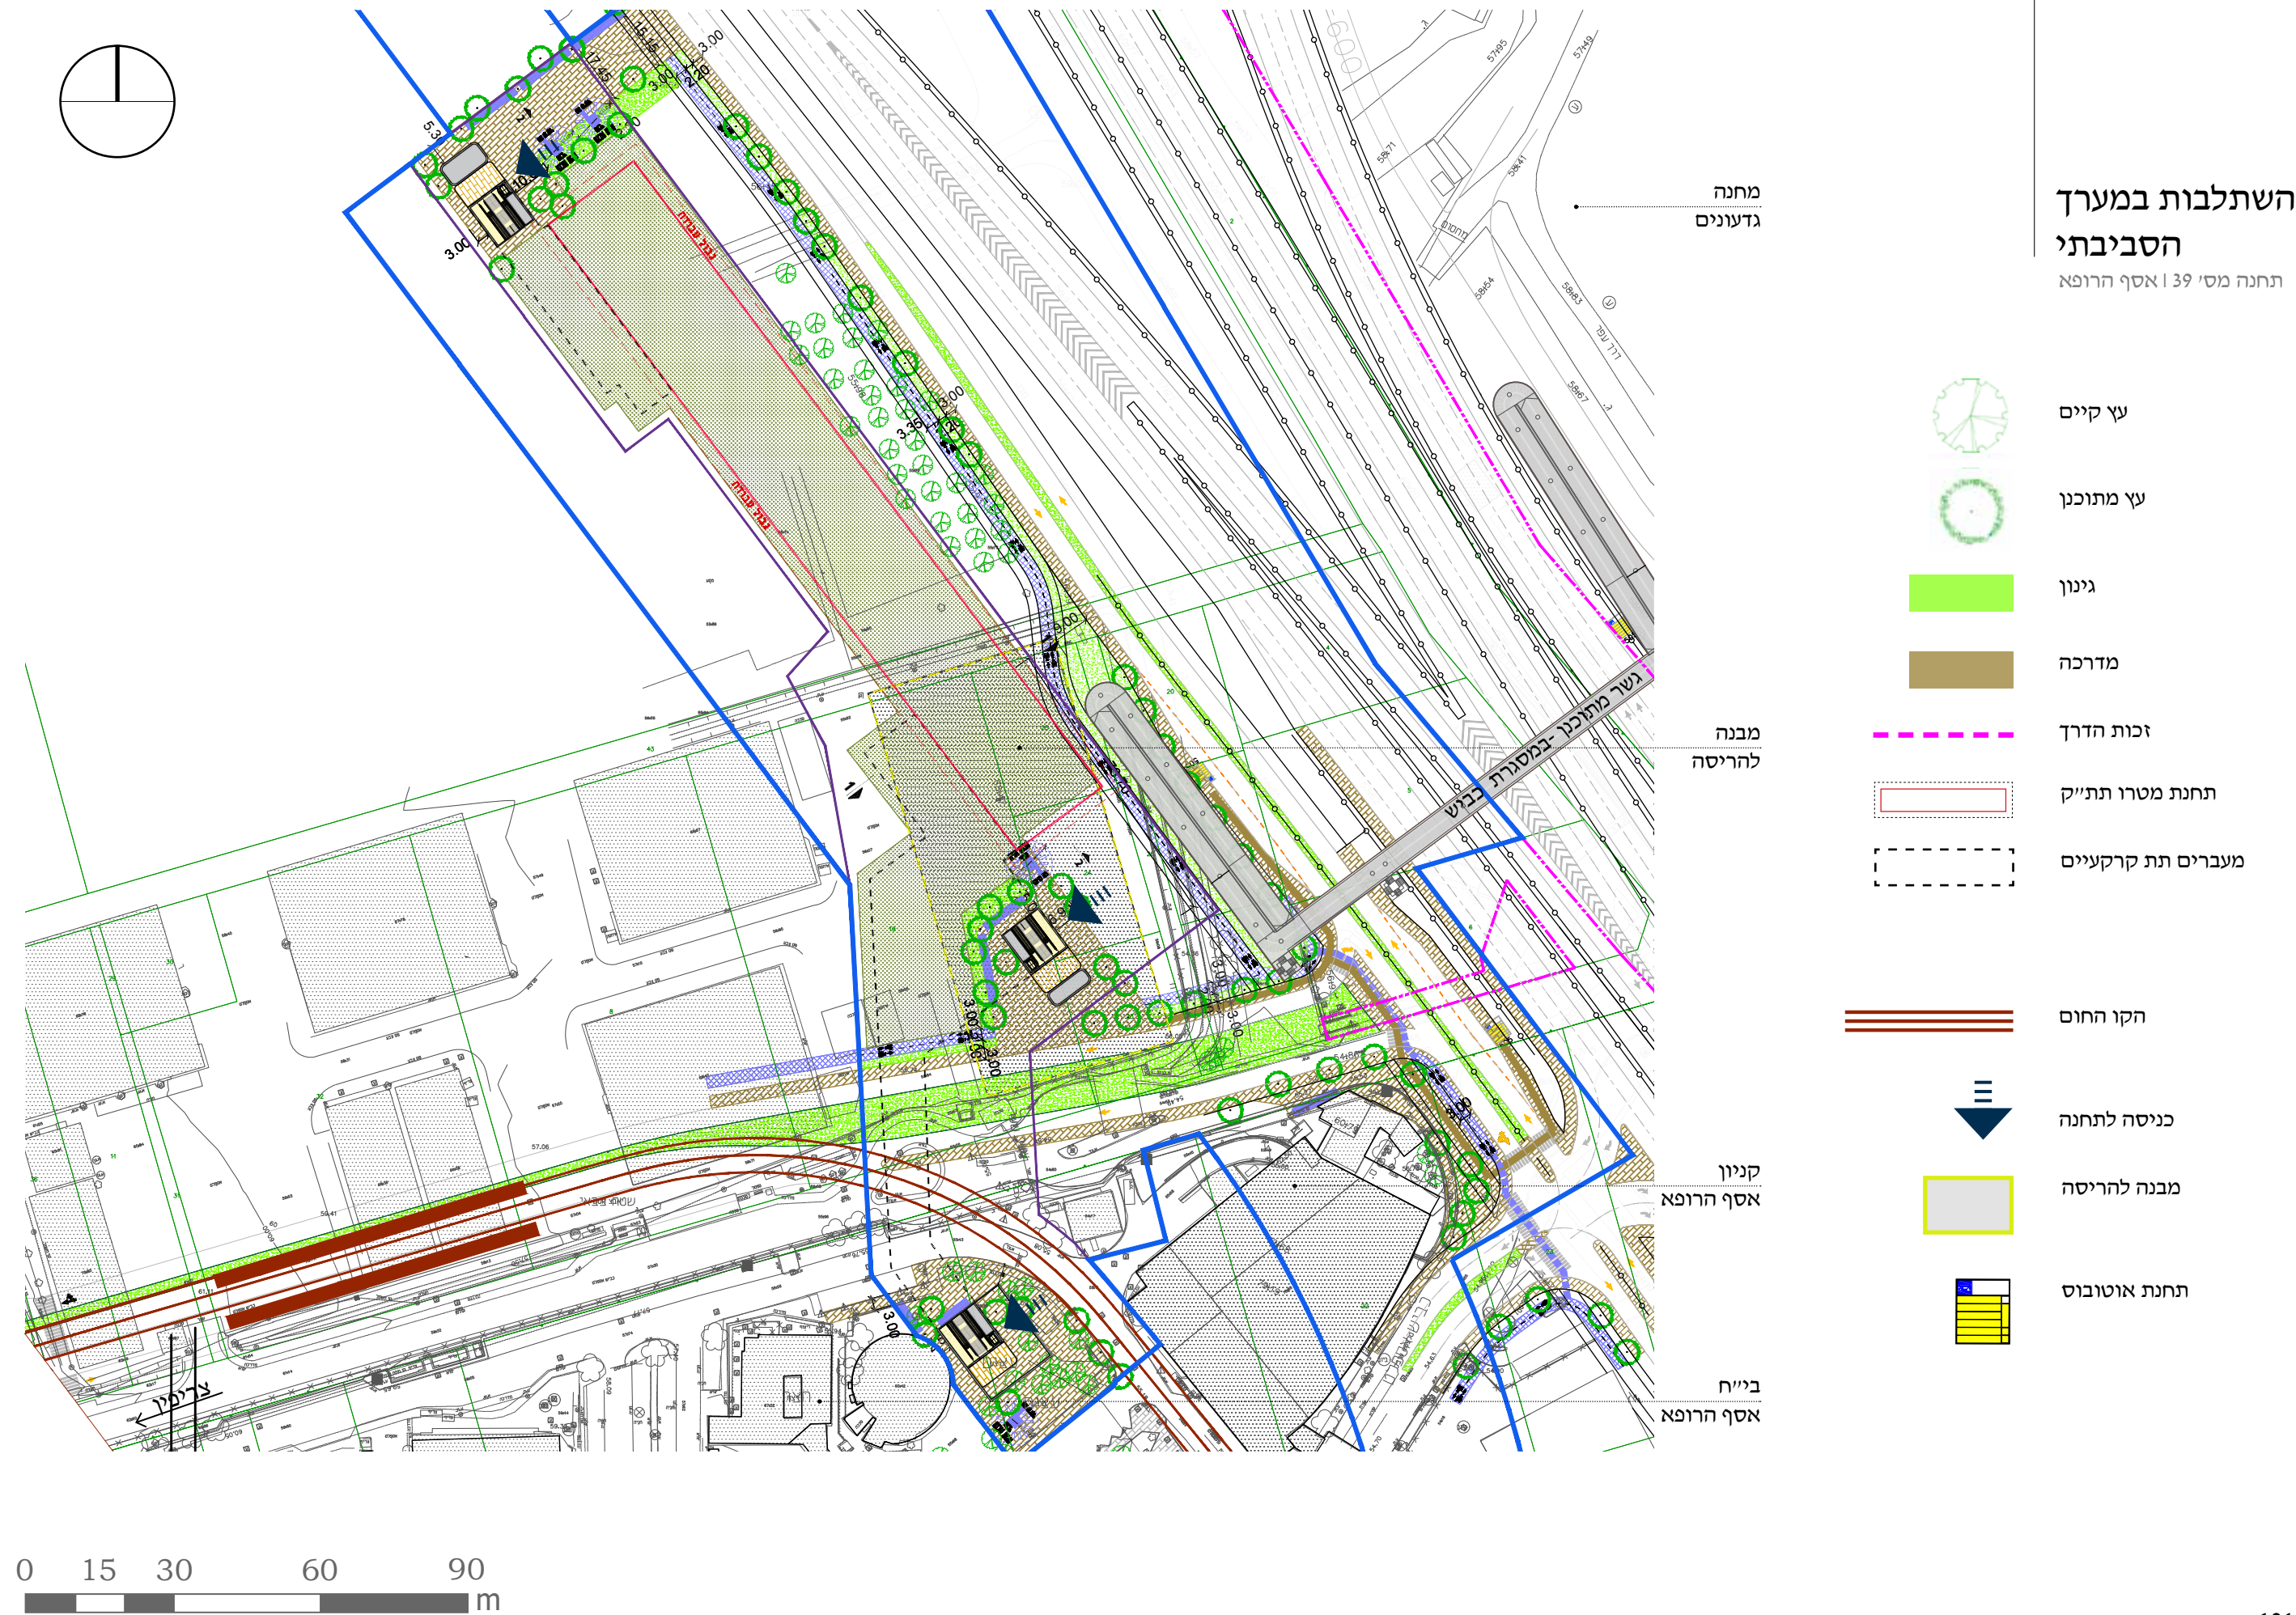

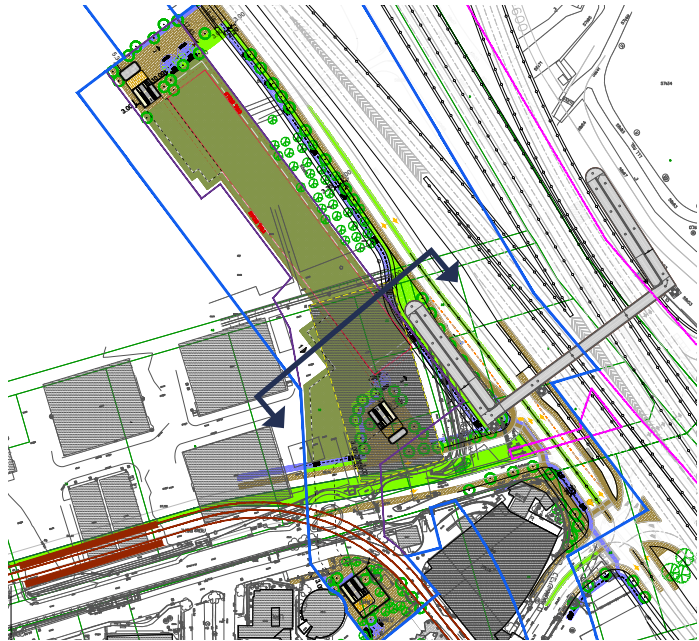

חתך רוחב
תחנה מס' 39 | אסף הרופא

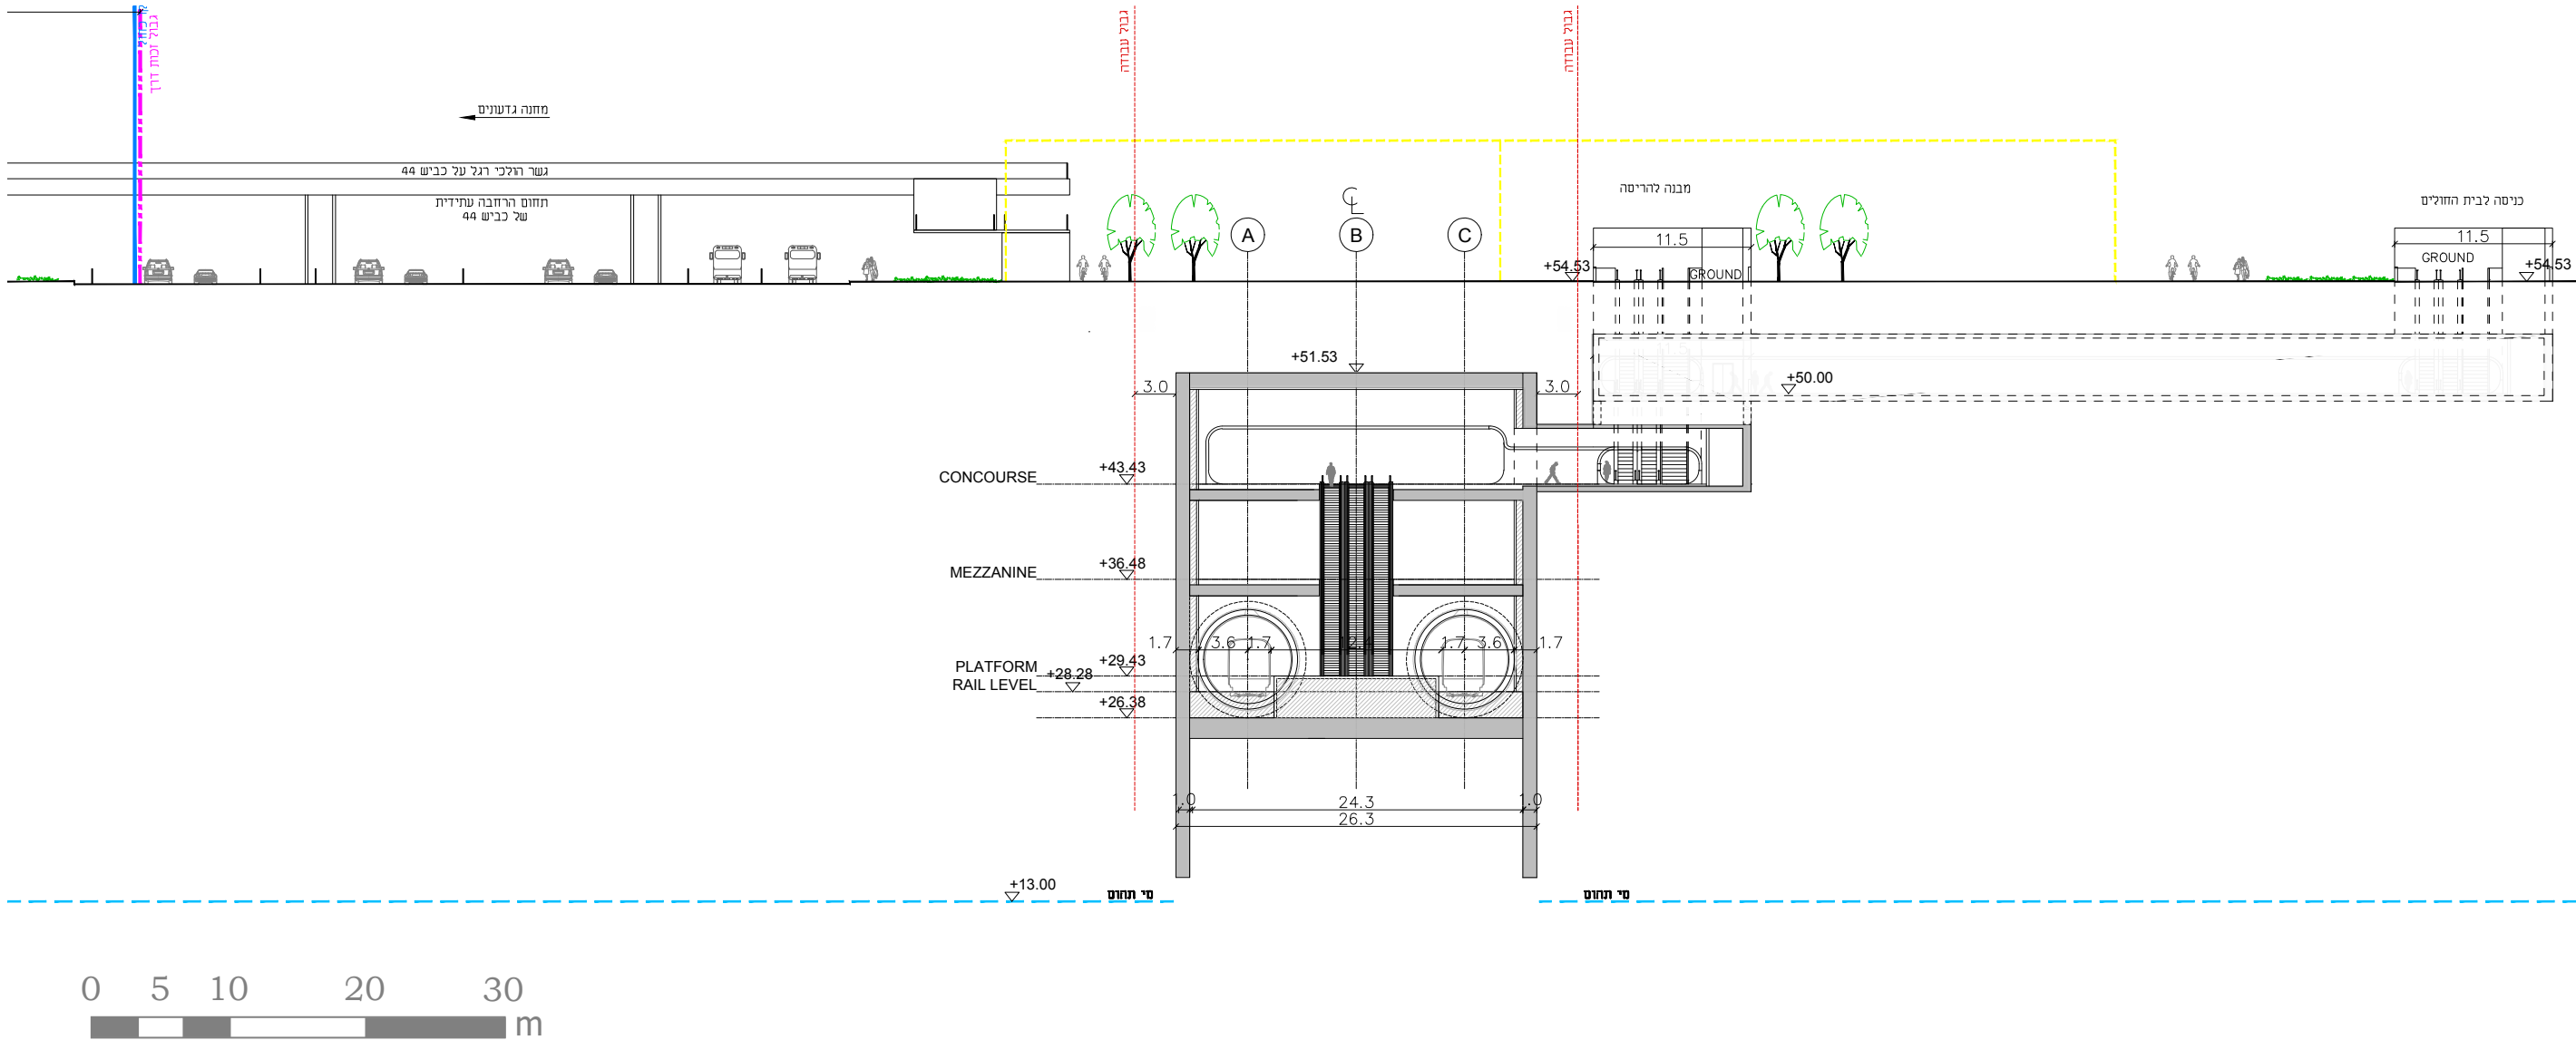

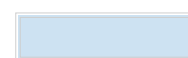

תחנת מטרו תת"ק



כניסה לתחנה

מסקנות והמלצות

תחנה מסי 39 | אסף הרופא

1. התחנה ממוקמת על שטח בסיס צבאי המיועד לפינוי ממערב לכביש 44, בסמוך לכניסה לבית החולים אסף הרופא.
2. מיקום התחנה והכניסות תואמו עם תכניות ההרחבה והפיתוח של כביש 44 ועם נתיב התחבורה הציבורית המתוכנן לאורכו. כמו כן תואמו מול ביה"ח ותכנית המתאר הכוללנית של באר יעקב.
3. תוכננו שלוש כניסות. הכניסה הצפונית היא כניסה עתידית שתשרת פיתוח עתידי מצפון מערב. הכניסה הדרומית מפוצלת לשתי כניסות: כניסה אחת משרתת את הבסיס הצבאי ממערב, את תחנת הקו החום ואת תחנות האוטובוס על כביש 44. כמו כן משרתת את בסיס גדעונים ואת תחנות האוטובוס ממזרח לכביש דרך גשר הולכי הרגל. מכניסה זו יבוצע שרוול תת-קרקעי אל תוך תחום בית החולים, עם יציאה בסמוך למבנה בית הספר הקיים.
4. לצורך בניית התחנה יש לפנות מבנה השייך לבסיס צבאי. הבסיס מיועד לפינוי.

אפיון התחנה

תחנה מסי 40 | צריפין

מיקום התחנה

צריפין, התחנה ממוקמת בתוך צריפין – בתחום מחנה צבאי לפינוי, מדרום לבית החולים אסף הרופא. בעתיד על רחוב נעמי שמר – ציר אורך ראשי מתוכנן בפיתוח מתחמי צריפין. מצפון, בית החולים אסף הרופא. לבית החולים תכניות להרחבה דרומה. מדרום מזרח ומערב מתוכננות שכונות מגורים על שטח בסיס צריפין המתפנה.

סוג תחנה

תחנה רגילה

אפיון פיסי | סביבת התחנה

כיום בסיס צבאי. בעתיד מתוכננות שכונות מגורים: מתחם 7 – מתוכנן 1,600,000 מ"ר תעסוקה, 1800 יח"ד. הבסיס הצבאי במתחם זה מיועד לפינוי ב-2024.

מוקדי עניין

בית החולים אסף הרופא- כניסה עתידית (200 מ'). מוקדי עניין נוספים יגזרו בתכניות מפורטות עפ"י מיקום התחנה.

קישוריות ונגישות


קישוריות במרחק של כ-200 מ' לתחנת הקו החום העתידית על הרחוב העתידי נעמי שמר. מתוכננת רשת הולכי רגל בפיתוח השכונה העתידית. אין שבילי אופניים קיימים מתוכננים בשלב זה בסביבת התחנה

קיבולת נוסעים צפויה

תחזית נוסעים לשנת 2040 צופה כ- 2200 נוסעים עולים ויורדים בשעת שיא.

היבטים נוספים

מתוכננת הרחבת בית החולים דרומה. איזור לפיתוח עתידי למגורים ותעסוקה.

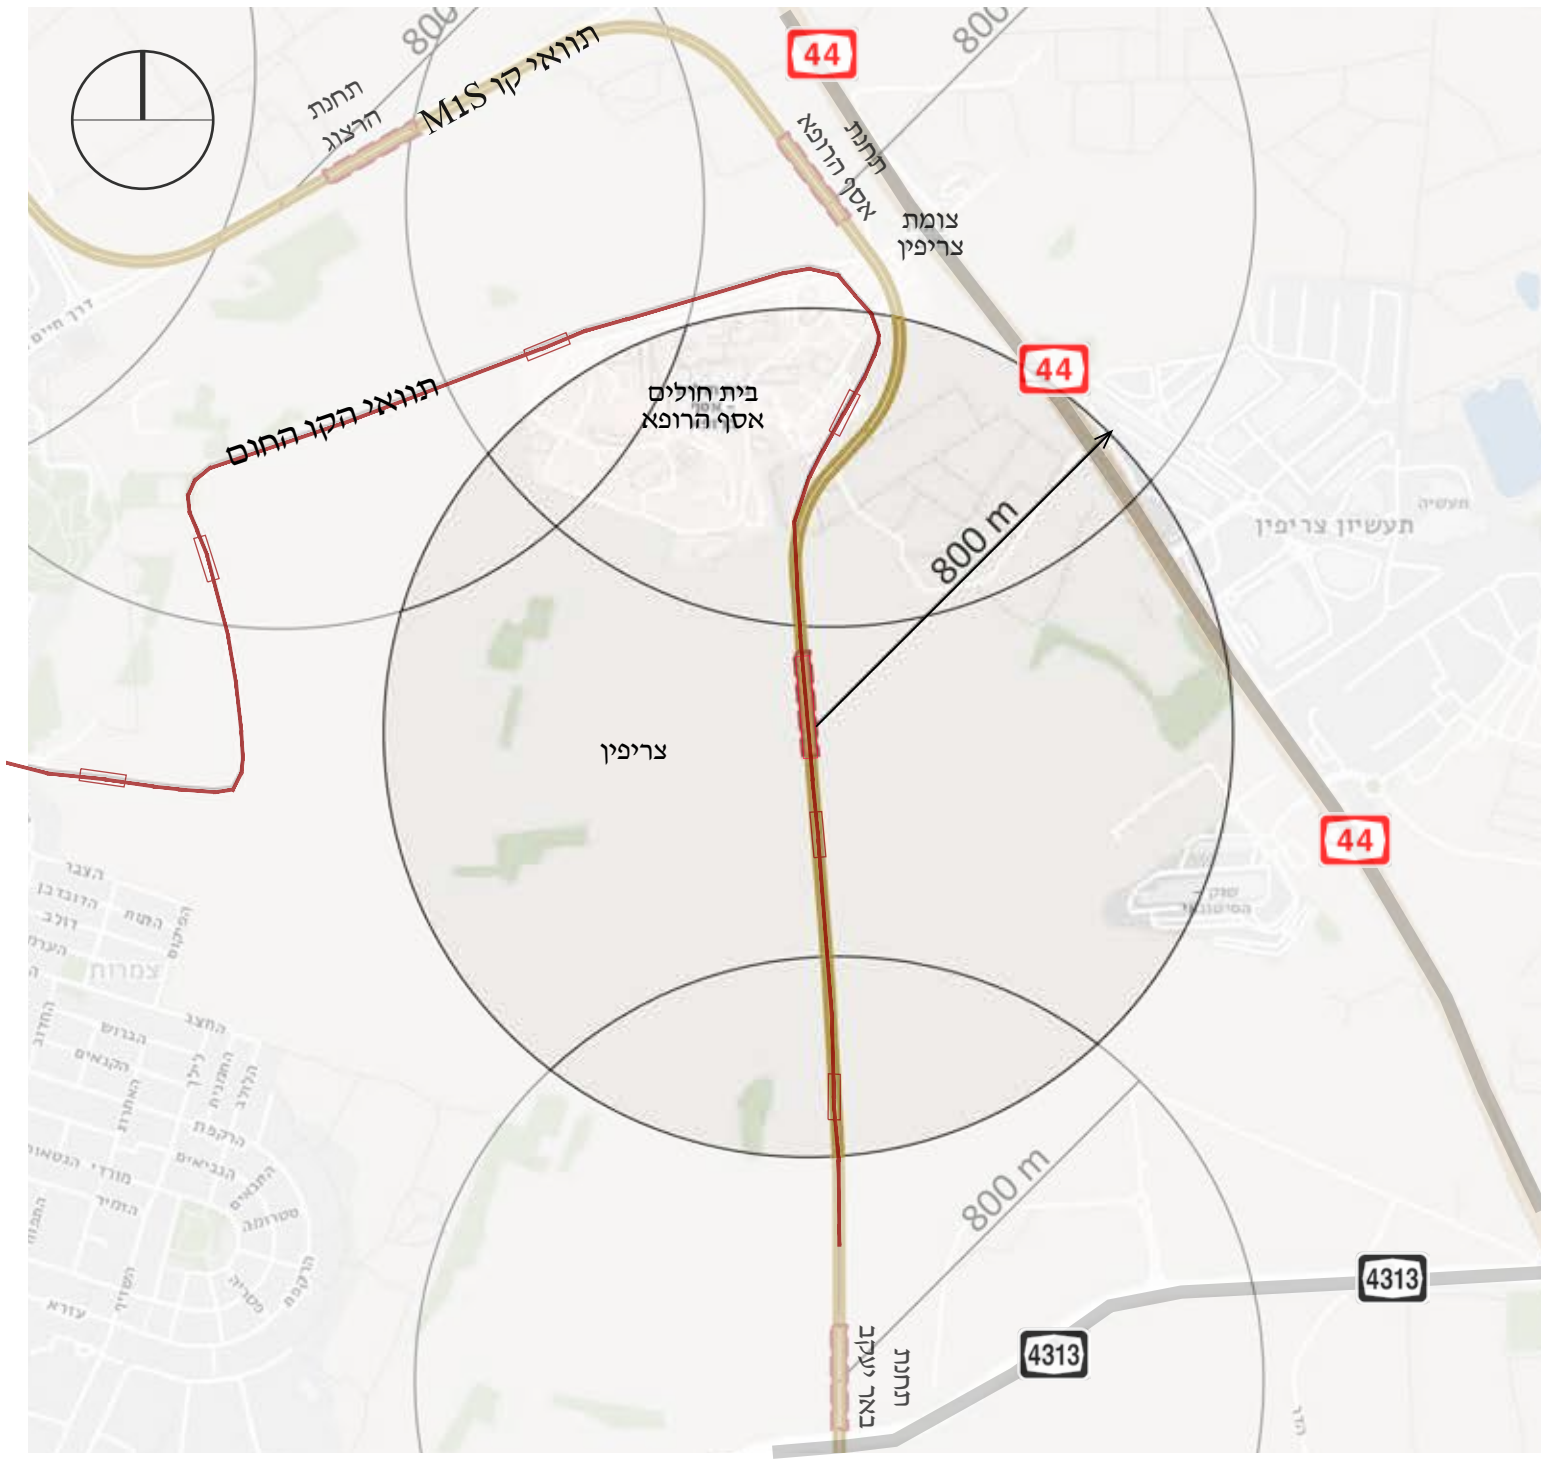

* שטח צבאי- לא ניתן לצלם