


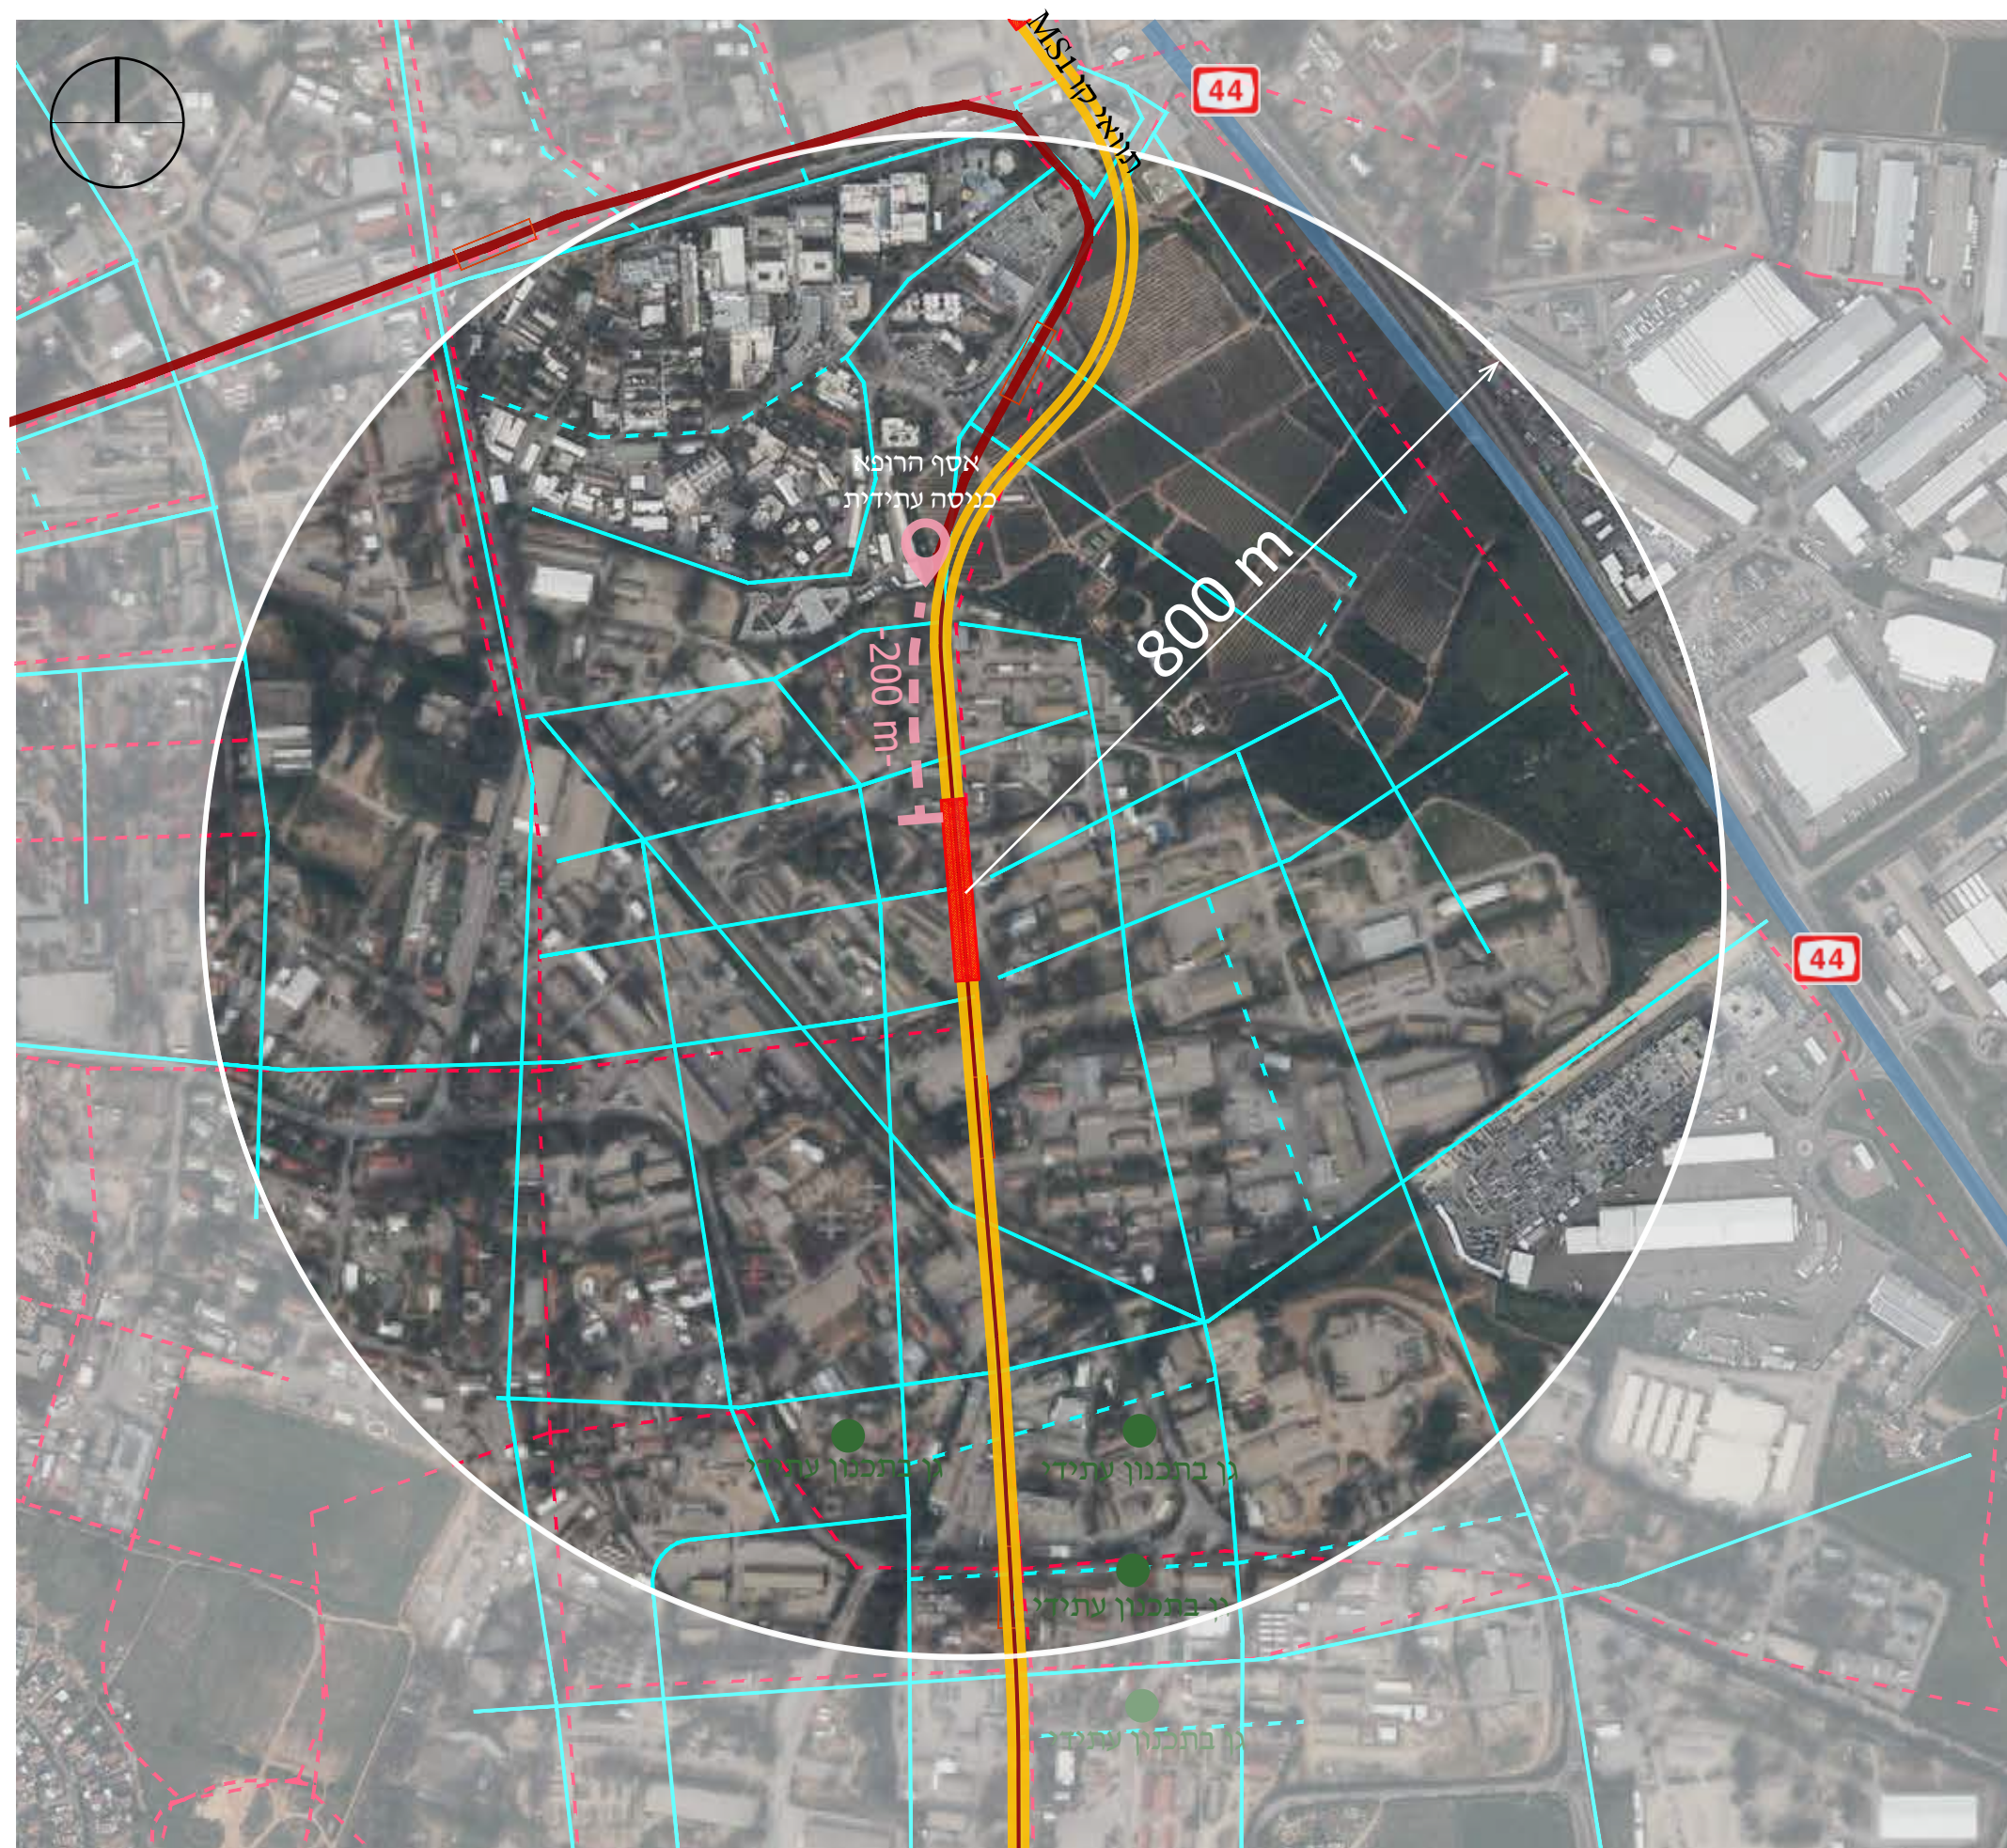


תחנה מס' 40 | צריפין



Page 10 of 10

1. **Introduction**



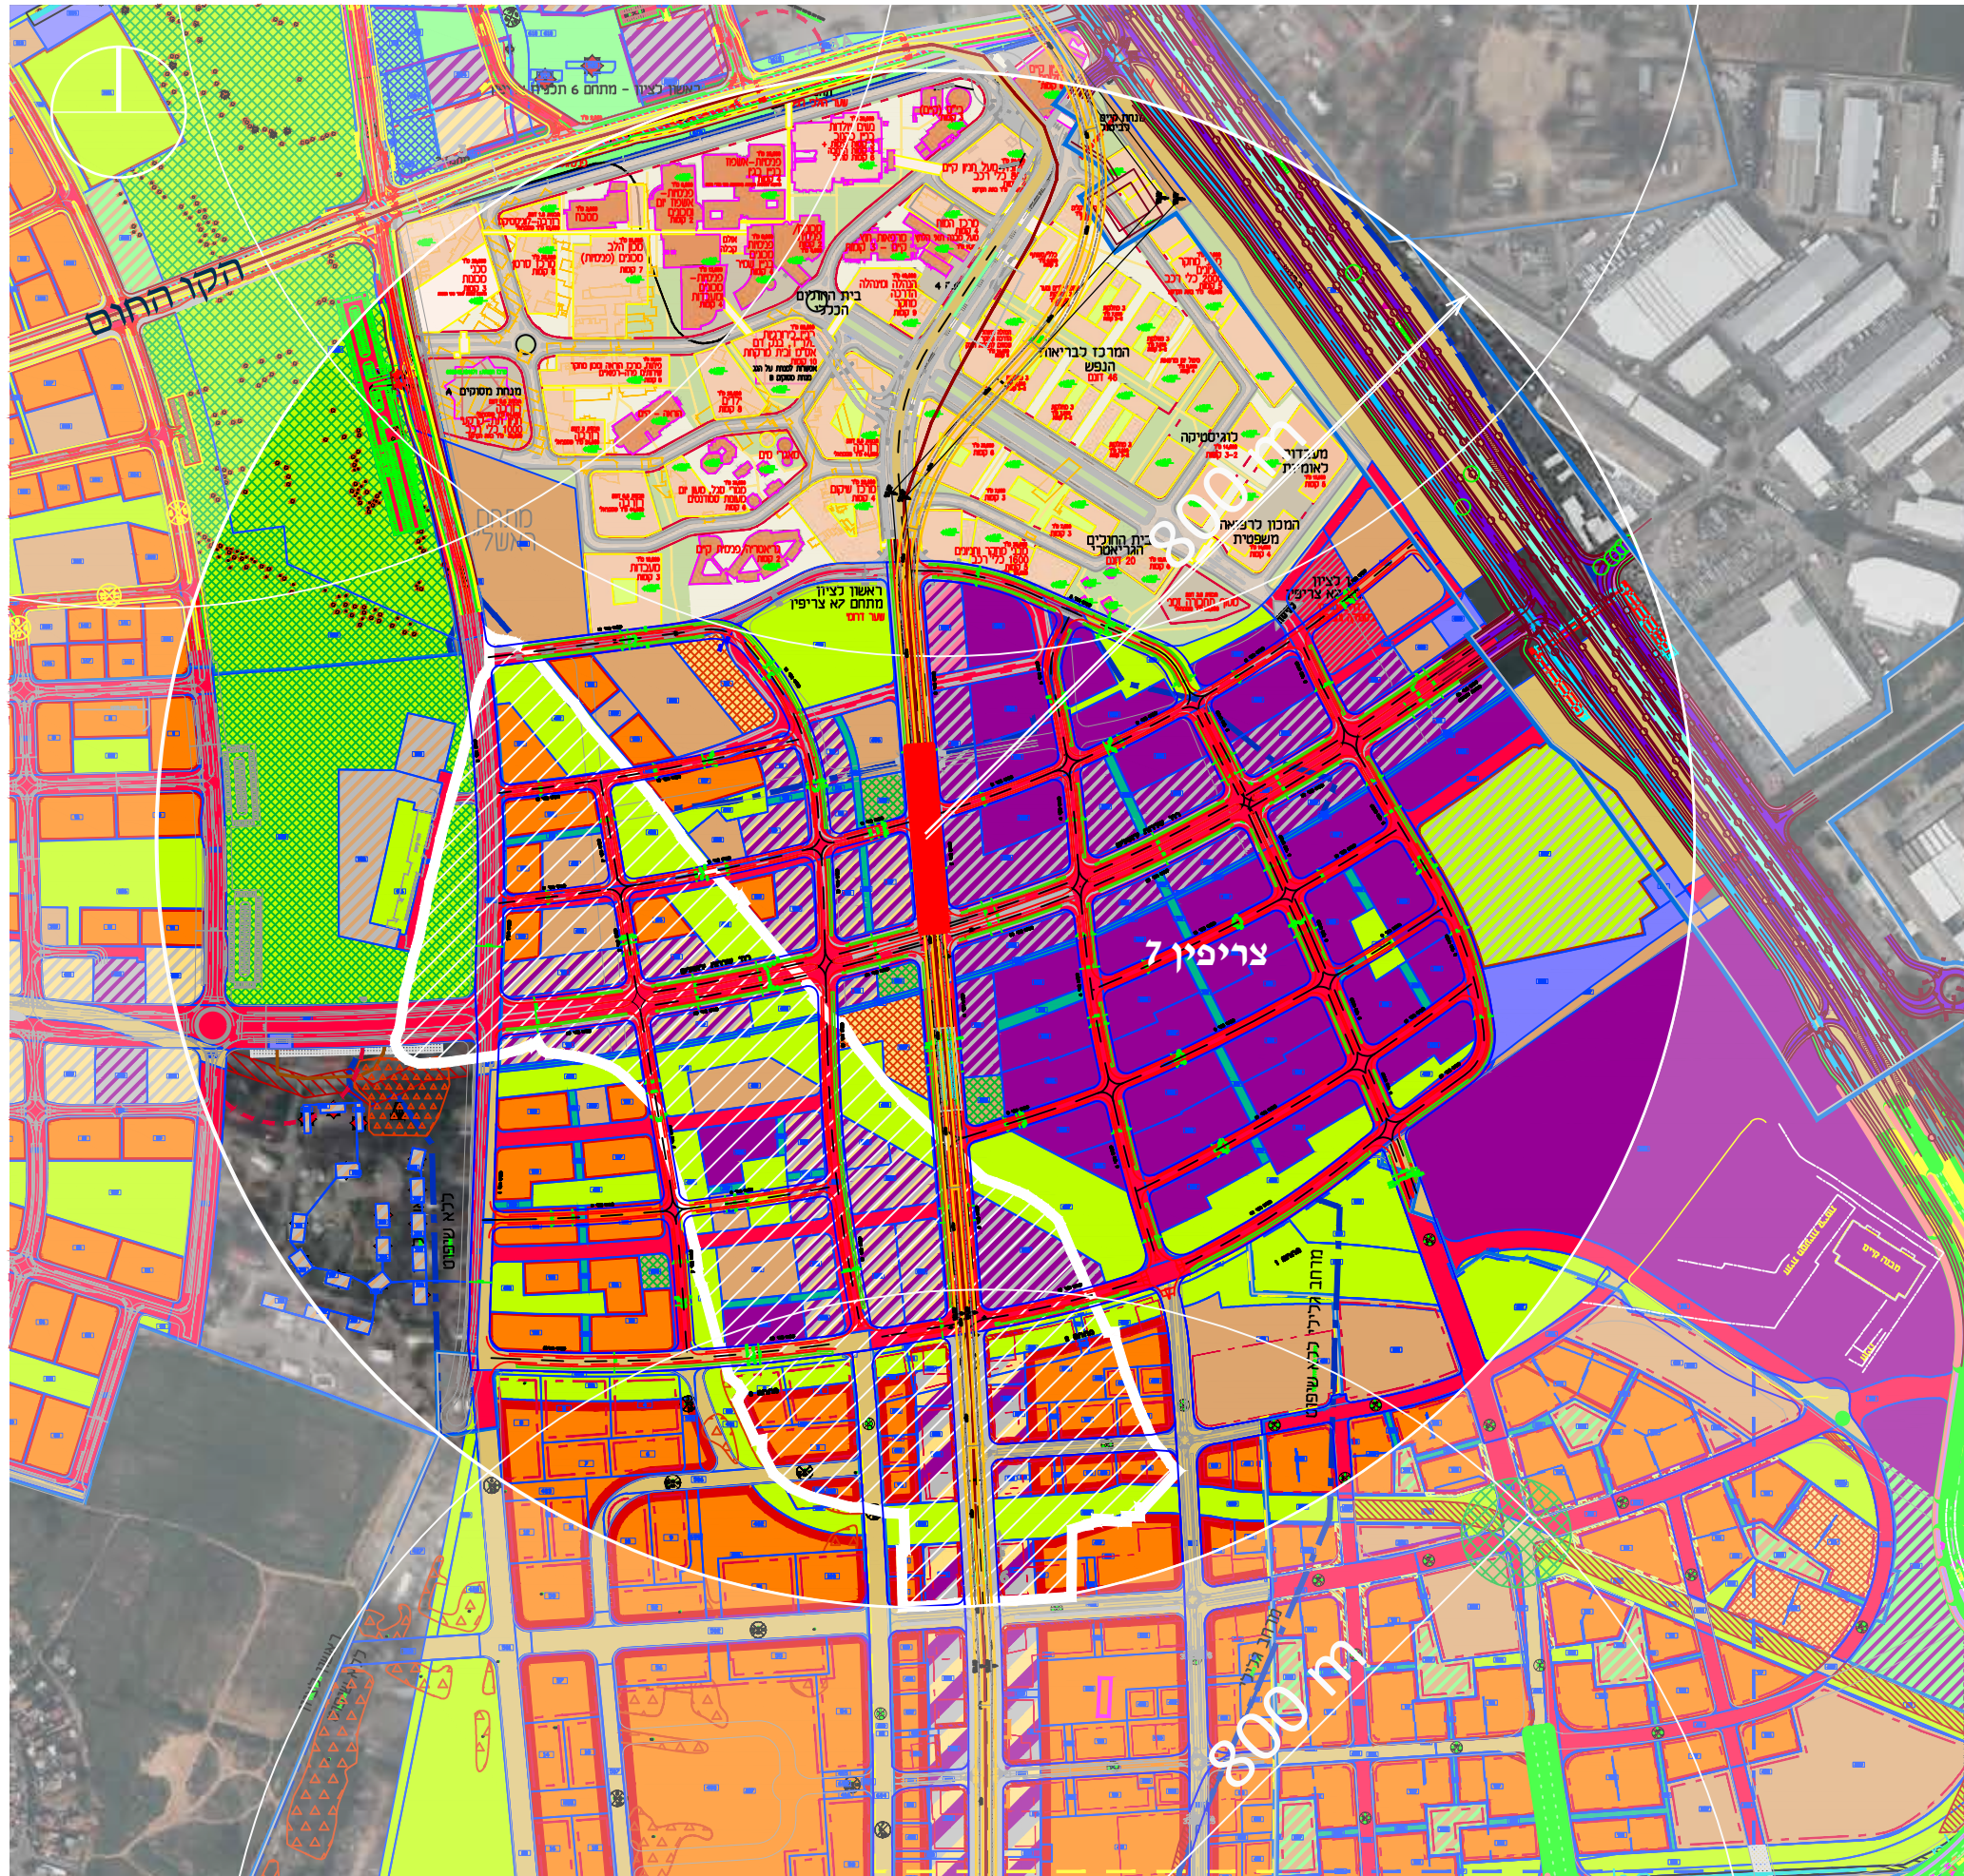

תכניות בהכנה

תחנה מס' 40 | צריפין


תכניות בהכנה

בסביבת התחנה

שם התכנית: אסף הרופא- 455-0631754
בתכנון: קולקר אדריכלים
סטטוס: מילוי תנאים להפקדה
מתוכנן: 1.1 מיליון מ"ר לשירותים
רופאיים.

שם התכנית: מתחם 7
בתכנון: קולקר אדריכלים
סטטוס: מילוי תנאים להפקדה
מתוכנן: 1,600,000 מ"ר תעסוקה,
1800 יח"ד.

רדיוס שירות

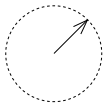

תוואי מטר



תחנת מטר



הקו החום





M1S

ת. צריפין

ייעודי קרקע

1:2500

המרחב הציבורי

תחנה מס' 40 | צריפין

פיתוח קיים ומתוכנן

כיום באזור זה נמצא מחנה צבאי, מחנה 108 - צריפין. הבסיס מיועד לפינוי ב-2024. התחנה בתחום תכניות מתחם 7 א' וב' בהכנה המציעות 1,600,000 מ"ר תעסוקה, 1800 יח"ד. התחנה ממוקמת בסמוך לשתי כיכרות עירוניות עתידיות לפי תכנית.

עוגנים למיקום התחנה והכניסות


התחנה מוקמה ברחוב עתידי בתחום תכנית בהכנה. התחנה מוקמה באזור של מחנה לפינוי. התוואי דרומה עובר בתחום מחנות שעדיין לא מיועדים לפינוי. תוכננו שלוש כניסות. כניסה צפון מערבית, כניסה מתוך כיכר עירונית, עפ"י התכנית בהכנה למתחם 7 בצריפין. כניסה מזרחית, בסמוך לצומת עם רחוב עתידי החוצה את רחוב נעמי שמר. כניסה דרום-מערבית משולבת בכיכר ציבורית, עפ"י התכנית בהכנה למתחם 7 בצריפין. כניסה זו תשמש גם לקישוריות עם תחנת הקו החום.

קישוריות ונגישות

קישוריות לתחנת קו חום עתידית במרחק של כ-200 מ' מהתחנה. מתוכננת רשת הולכי רגל בפיתוח השכונה העתידית. שביל אופניים בציר המרכזי של תוכנית הבינוי העתידית, עובר בסמוך לתחנת צריפין.

תחנת מטרו

- תוואי מטרו
- תחנת מטרו תת"ק
- מעברים תת קרקעיים
- מבנה כניסה לתחנה
- כניסה לתחנה
- מבנים
- שצ"פ סטטוטורי
- מבנים ומוסדות ציבור סטטוטוריים
- הקו החום
- שביל אופניים קיים
- שביל אופניים מתוכנן
- ציר הולכי רגל ראשי
- ציר הולכי רגל משני

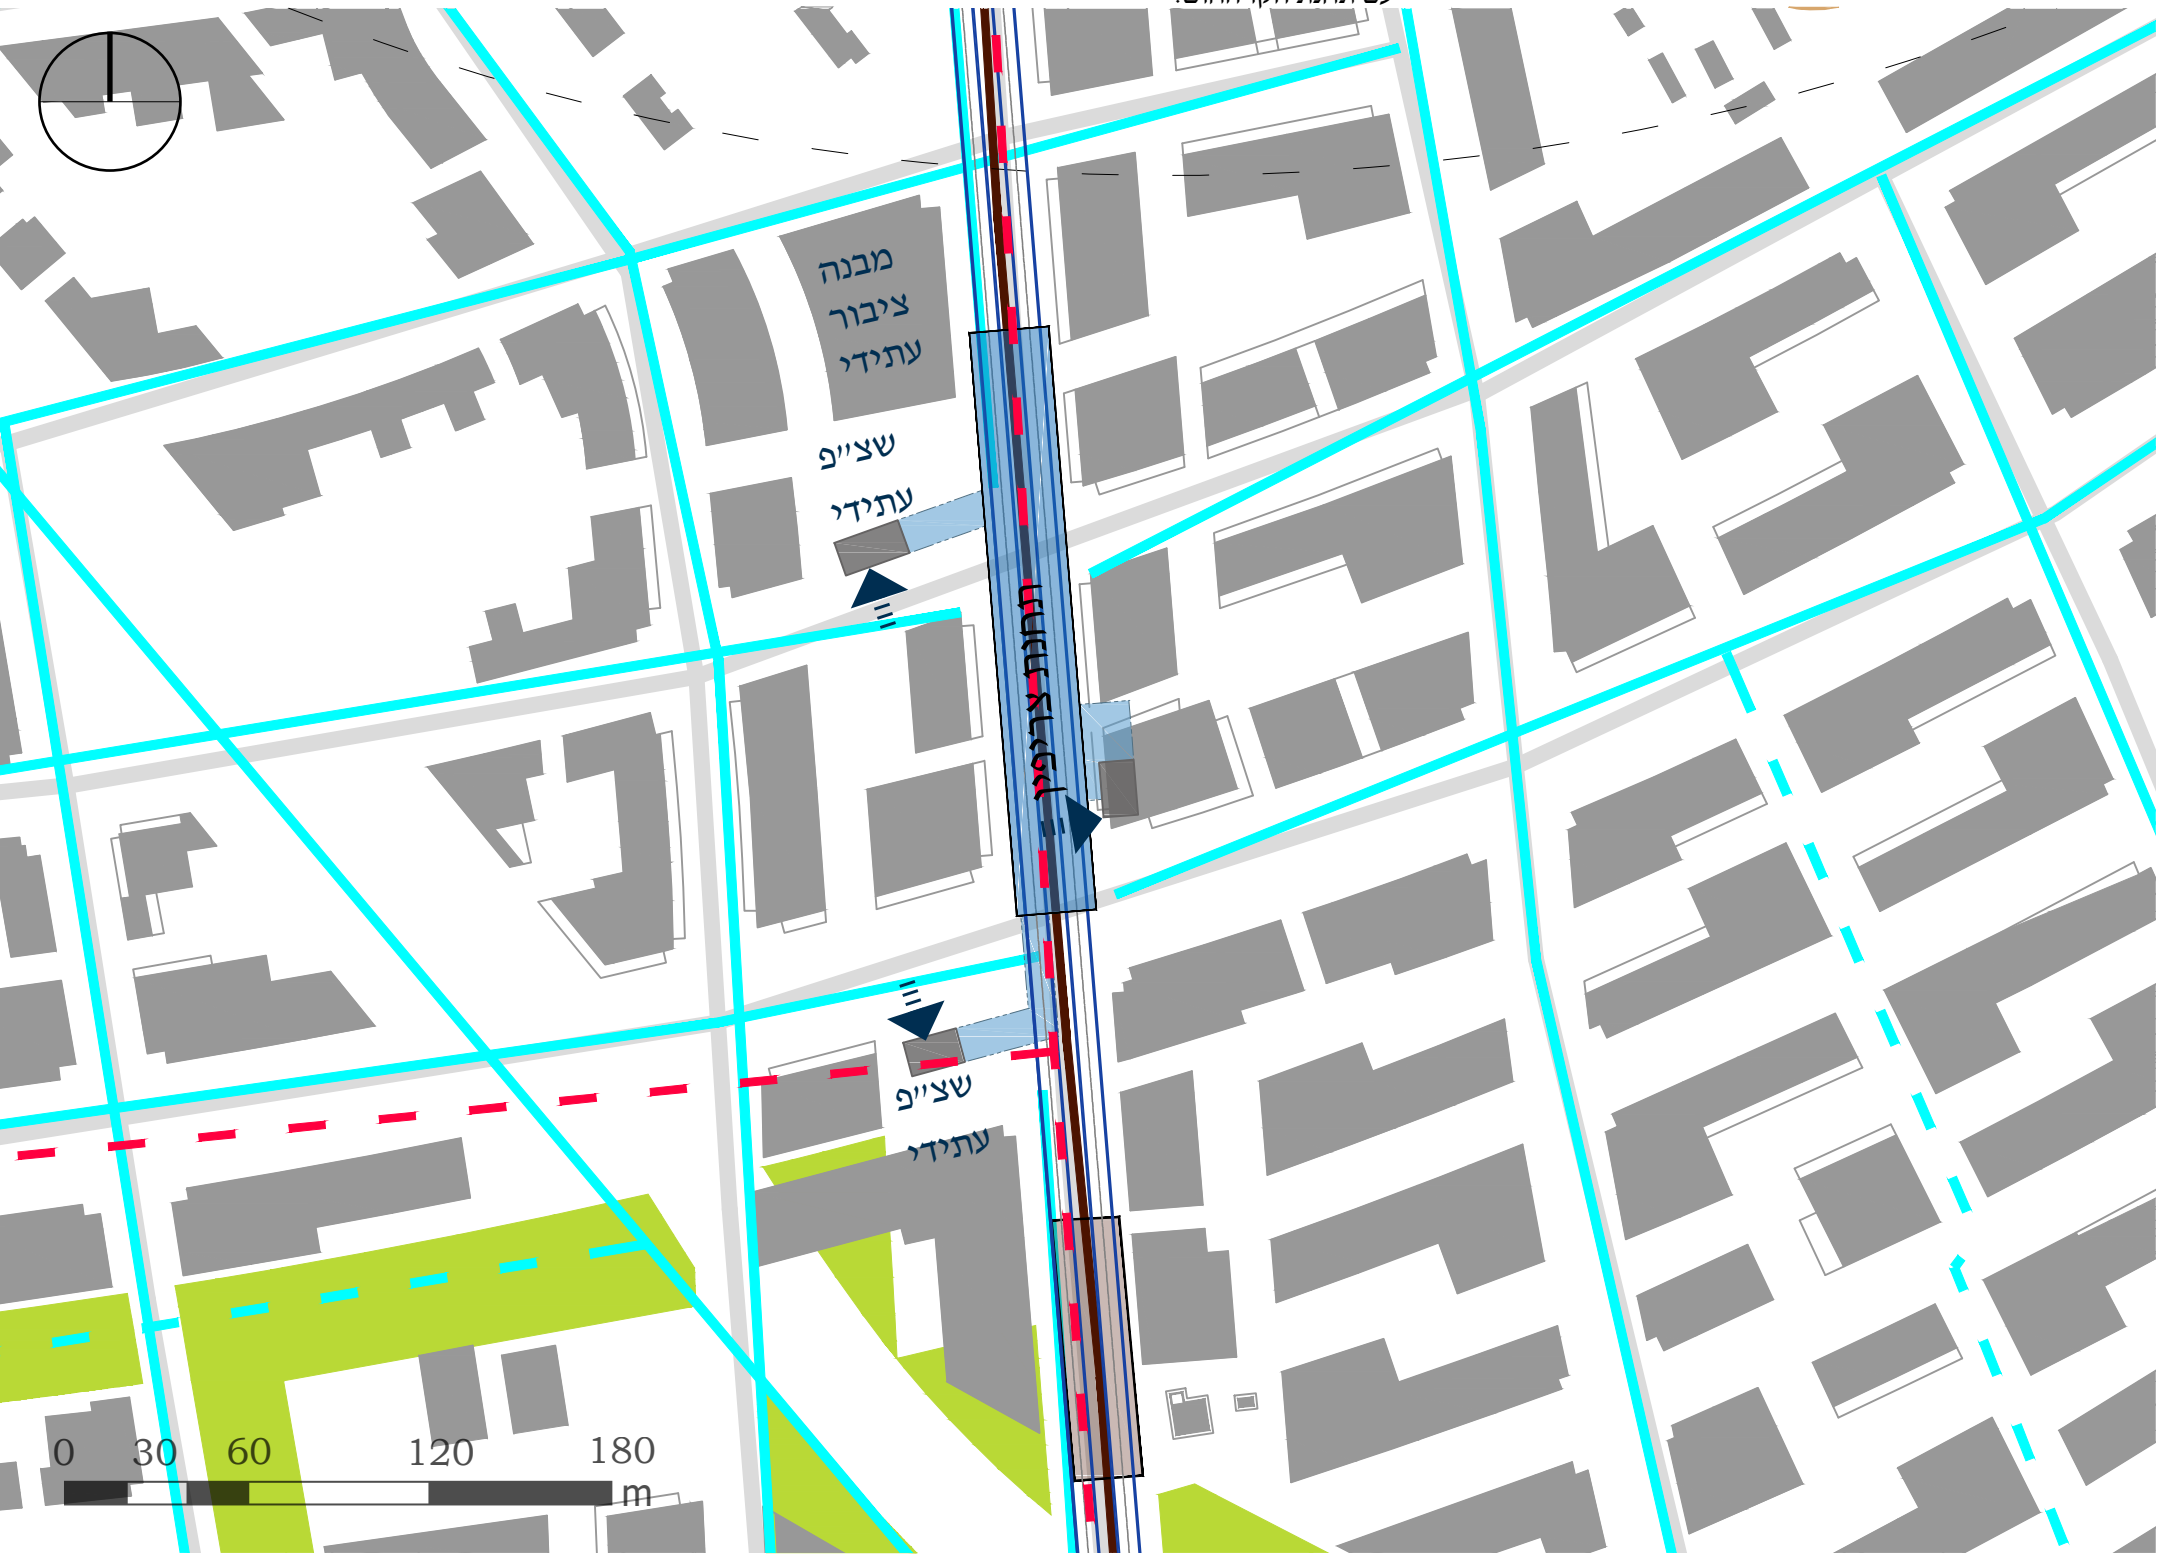



מצב מאושר

תחנה מסי 40 | צריפין

ייעודי קרקע מאושרים

-  מסילת ברזל
-  רצועת מתעיין עפ"י תכנית בהכנה
-  שטח חקלאי

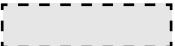-  כניסה לתחנה
-  תחנת מטרו תת"ק
-  מעברים תת קרקעיים

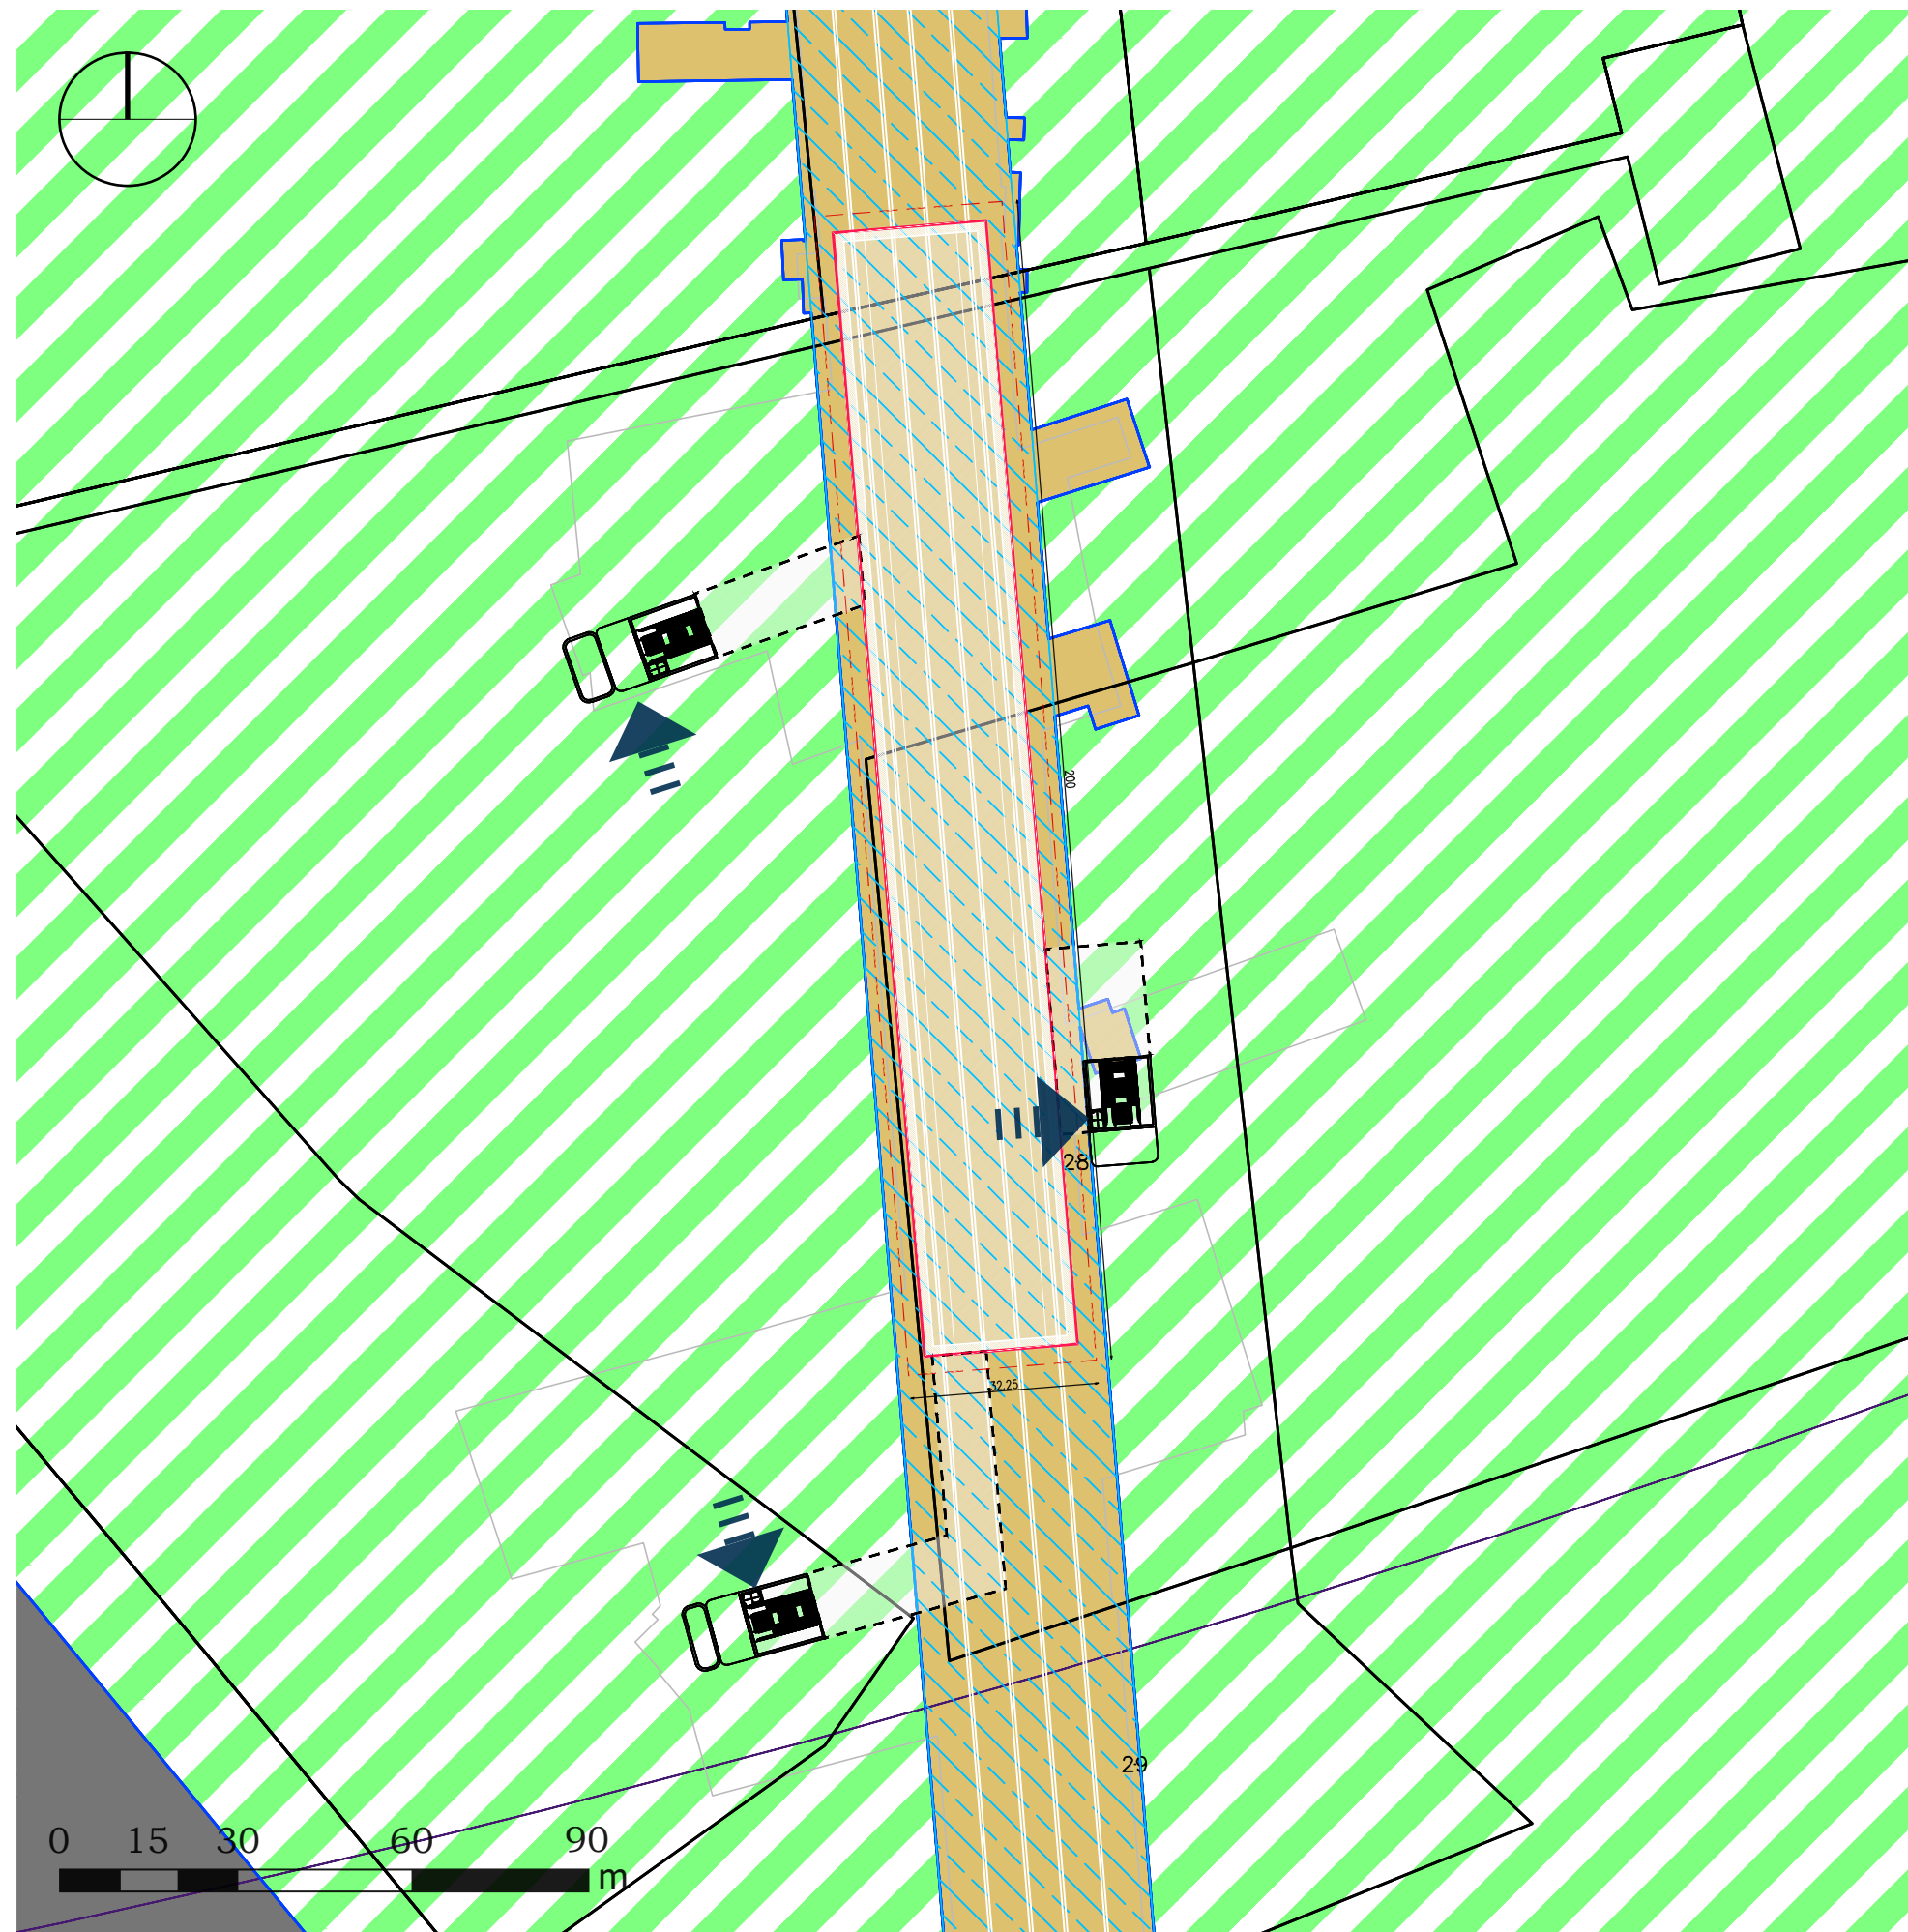


M1S

ת. צריפין


תכנית מאושרות

1:1250


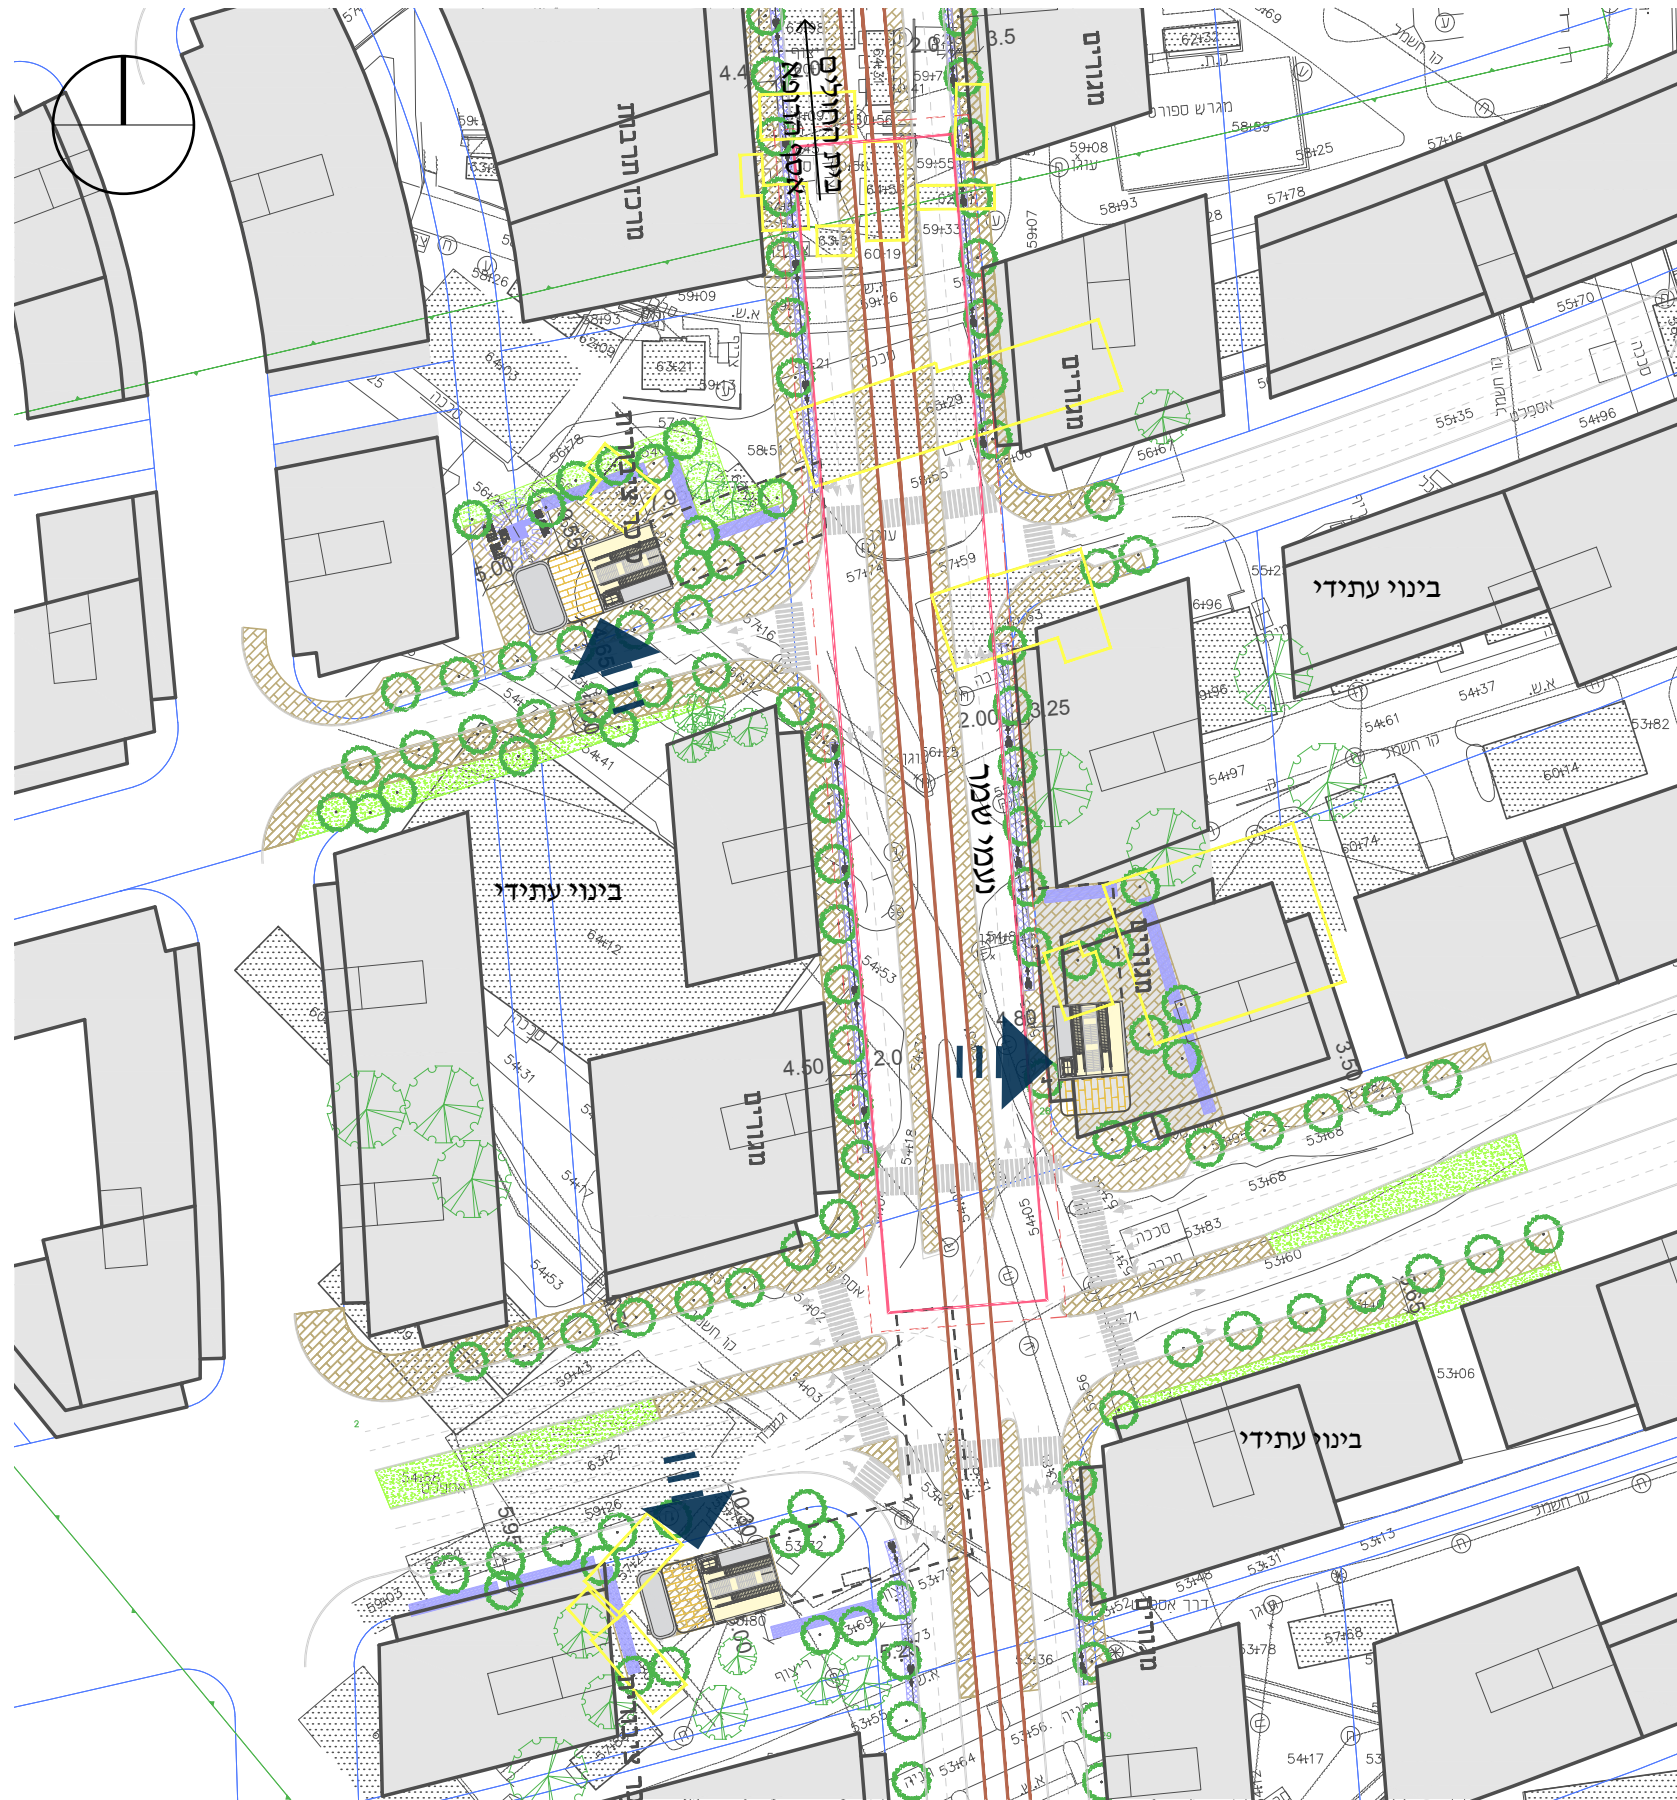


השתלבות במערך
הסביבתי


תחנה מס' 40 | צריפין

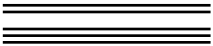-  עץ קיים
-  עץ מתוכנן
-  גיזון
-  מדרכה
-  זכות הדרך
-  תחנת מטרו תת"ק
-  מעברים תת קרקעיים
-  תוואי מטרו
-  הקו החום
-  כניסה לתחנה
-  מבנה להריסה
-  תחנת אוטובוס



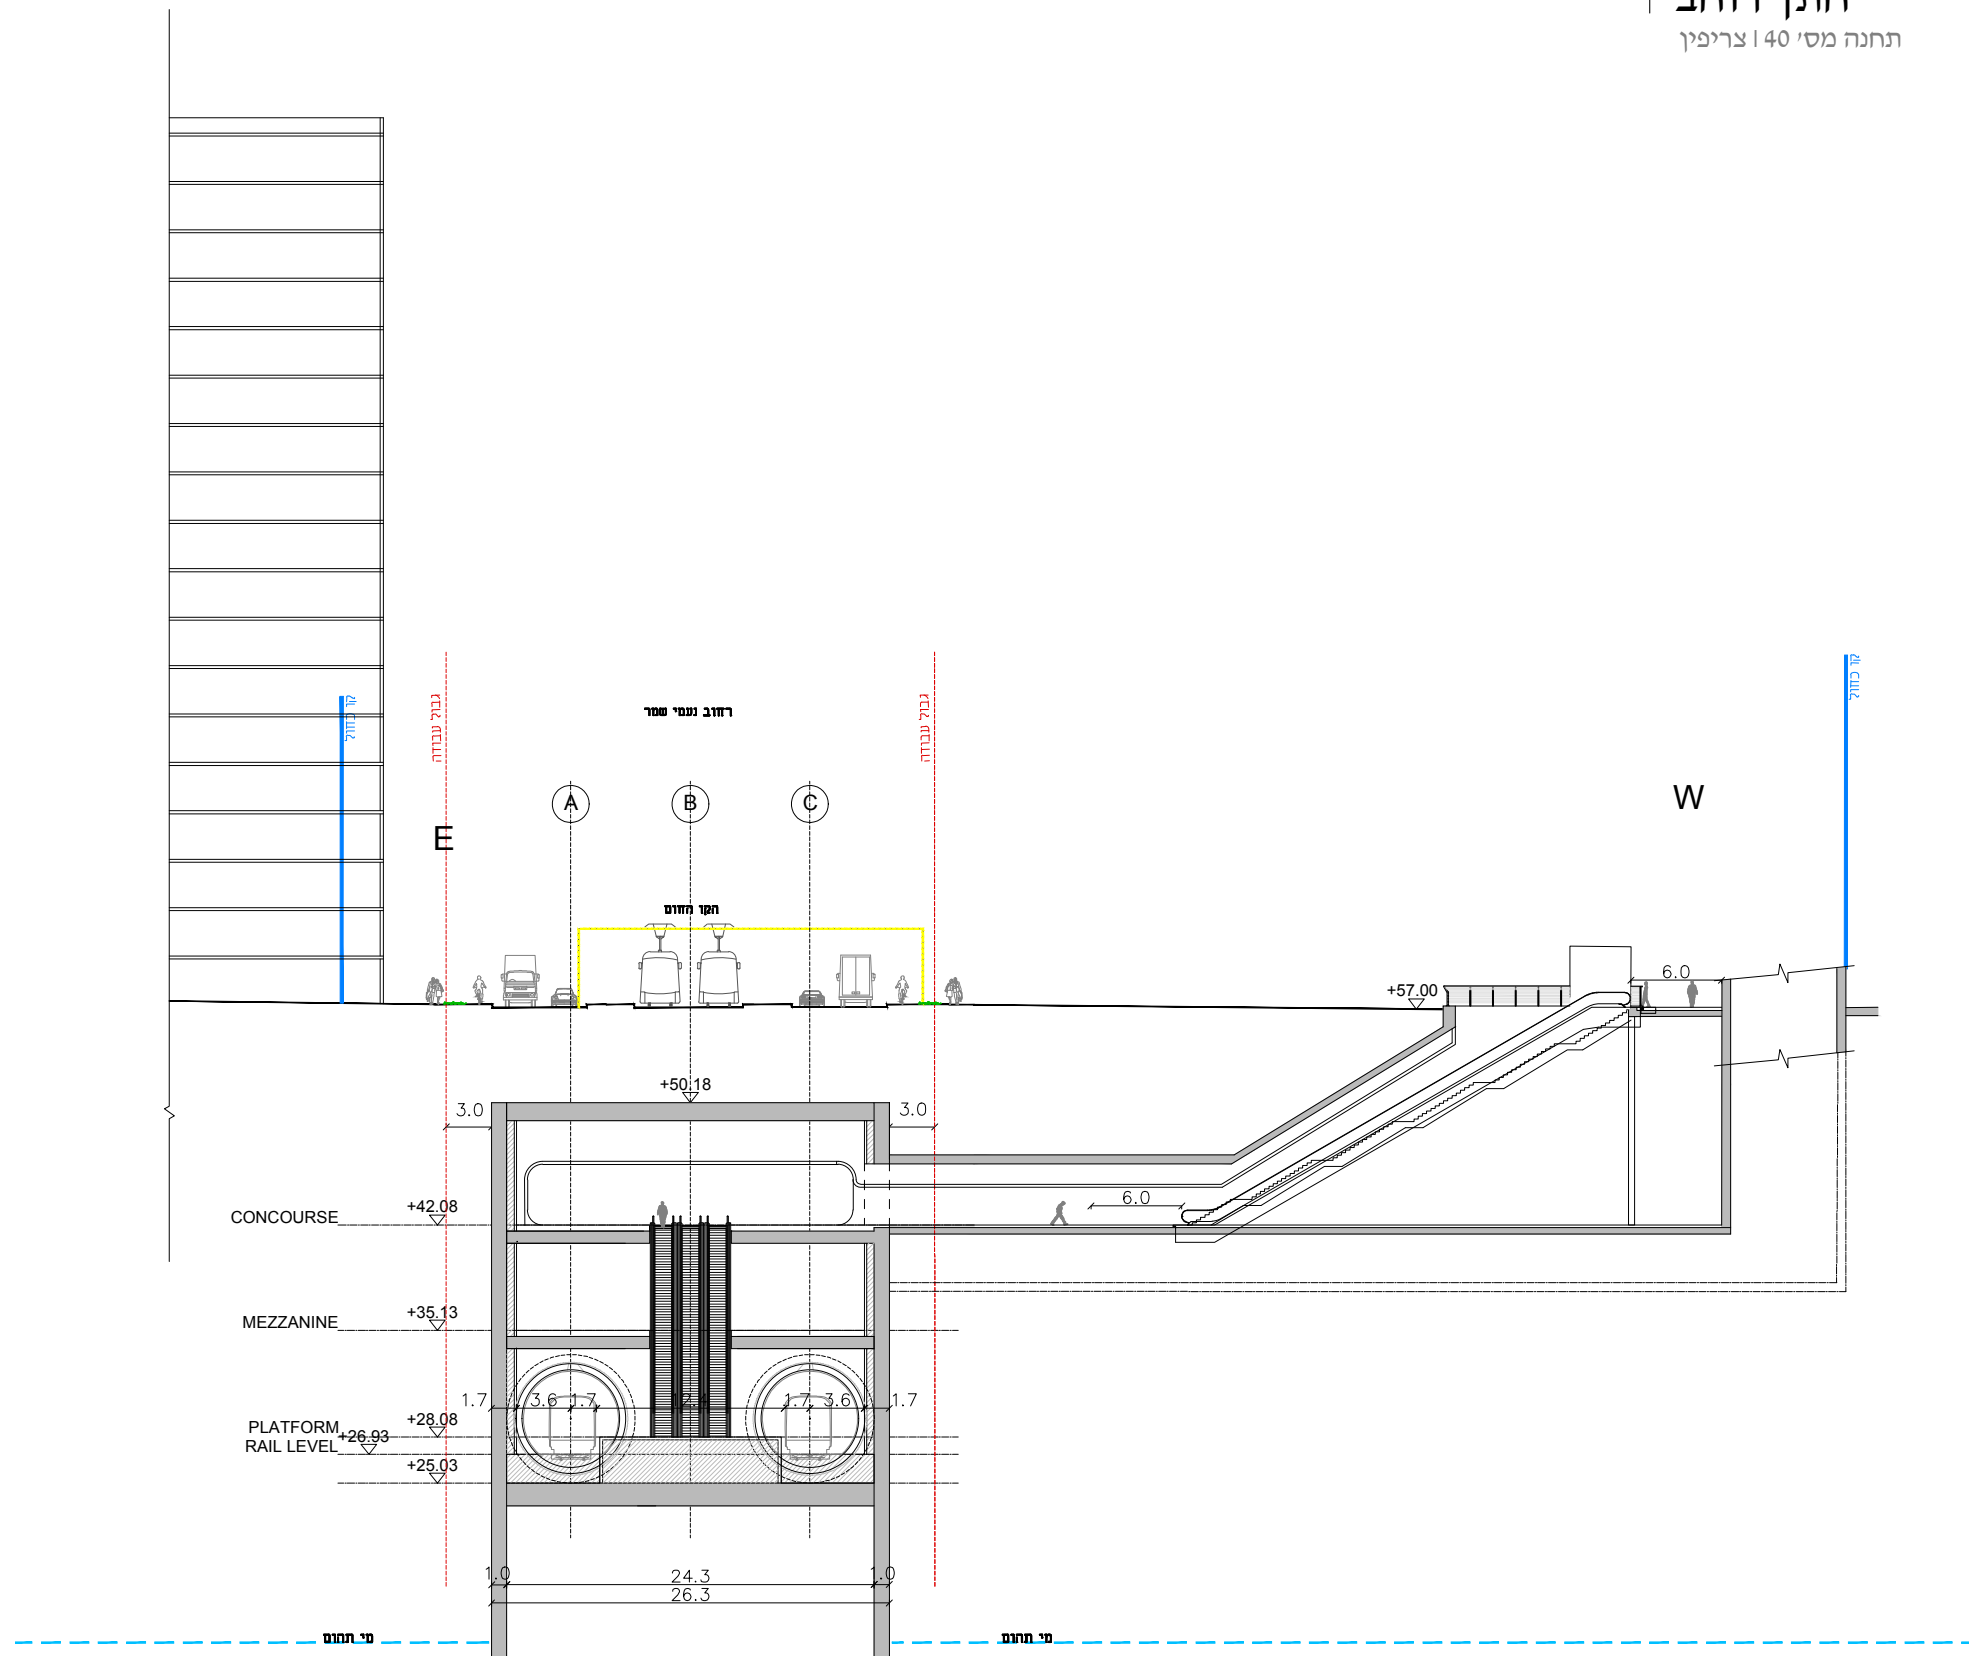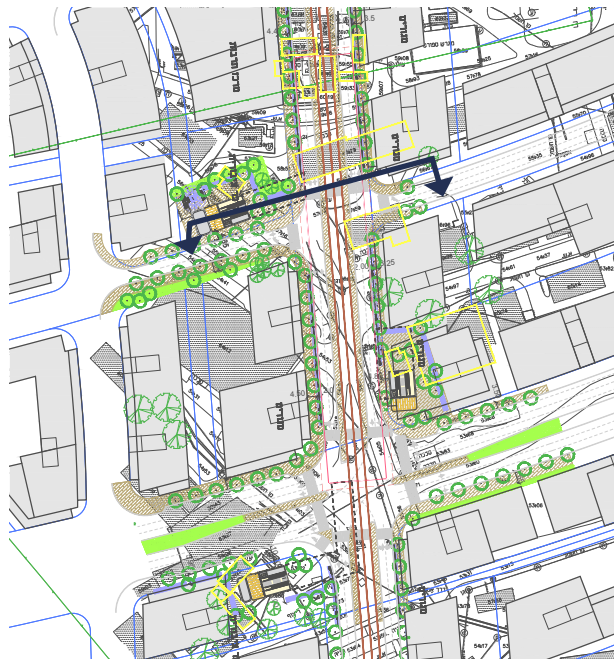

חתך רוחב
תחנה מסי 40 | צריפין

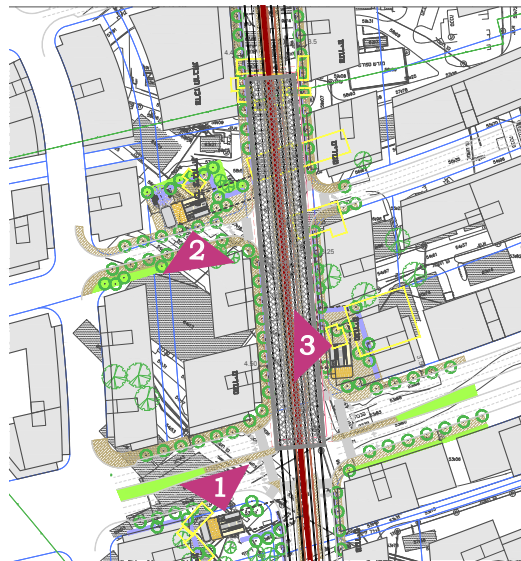

מסקנות והמלצות
תחנה מס' 40 | צריפין

1. התחנה מתוכננת בתחום מחנה צבאי קיים צריפין המתפנה ב2024.
2. תכנון התחנה והכניסות תואם עם תכנית השלד למתחמי צריפין ועם תכנית מתחם 7, הנמצאת בשלבי תכנון.
3. התחנה מתוכננת על רחוב נעמי שמר העתידי.
4. תוכננו 3 כניסות המשרתות את רח' נעמי שמר העתידי. רח' מע"ר ראשי אורכי לכל אורך באר יעקב. שתי הכניסות המערביות על שטחים המתוכננים ככיכרות עירוניות. הכניסה המזרחית, על שטח ביעוד תעסוקה. יהיה צורך להתאים את הבינוי העתידי לתכנית הכניסה.

אפיון התחנה

תחנה מס' 41 | באר יעקב

מיקום התחנה

באר יעקב, התחנה ממוקמת בתחום צריפין - מחנה צבאי לפינוי. בעתיד על רחוב נעמי שמר - ציר אורך ראשי מתוכנן בפיתוח מתחמי צריפין. מצפון לכביש 4313.

מצפון, מזרח ומערב מתוכננות שכונות מגורים על שטח בסיס צריפין המתפנה. מדרום איזור תעשייה באר יעקב ושכונת רמב"ם.

תחנה רגילה

סוג תחנה

אפיון פיסי | סביבת התחנה

מתחמי תכנון עתידי בצריפין - כיום בסיס צבאי בעתיד מתוכננות שכונות מגורים. מתחם 1 - 3700 יח"ד, מסחר, תעסוקה ומבני ציבור. מאושר. מתחם 2 - 3200 יח"ד, 180 אלף מ"ר מסחר תעסוקה וכן ציבור. מאושר. מתחם 3 - 2750 יח"ד, 11,132 מסחר מתחם 6 באר יעקב (לא ממתחמי צריפין) - 2148 יח"ד, 115 אלף מ"ר תעסוקה. בהכנה.

מוקדי העניין יגזרו בתכניות מפורטות עפ"י מיקום התחנה כעוגן אורבני.

מוקדי עניין

(במרחק של עד 800 מ' מהתחנה)

קישוריות ונגישות


נגישות הולכי רגל ברחובות ובשבילים מתוכננים המקשרים בין גנים ציבוריים עתידיים וברחובות קיימים בשכונה שד' רומית לתחנה. לא ידוע על שבילי אופניים בסביבת התחנה. קישוריות צמודה לקו החום.

קיבולת נוסעים צפויה

תחזית נוסעים לשנת 2040 צופה כ- 1700 נוסעים עולים ויורדים בשעת שיא.

היבטים נוספים

איזור לפיתוח עתידי למגורים ותעסוקה.

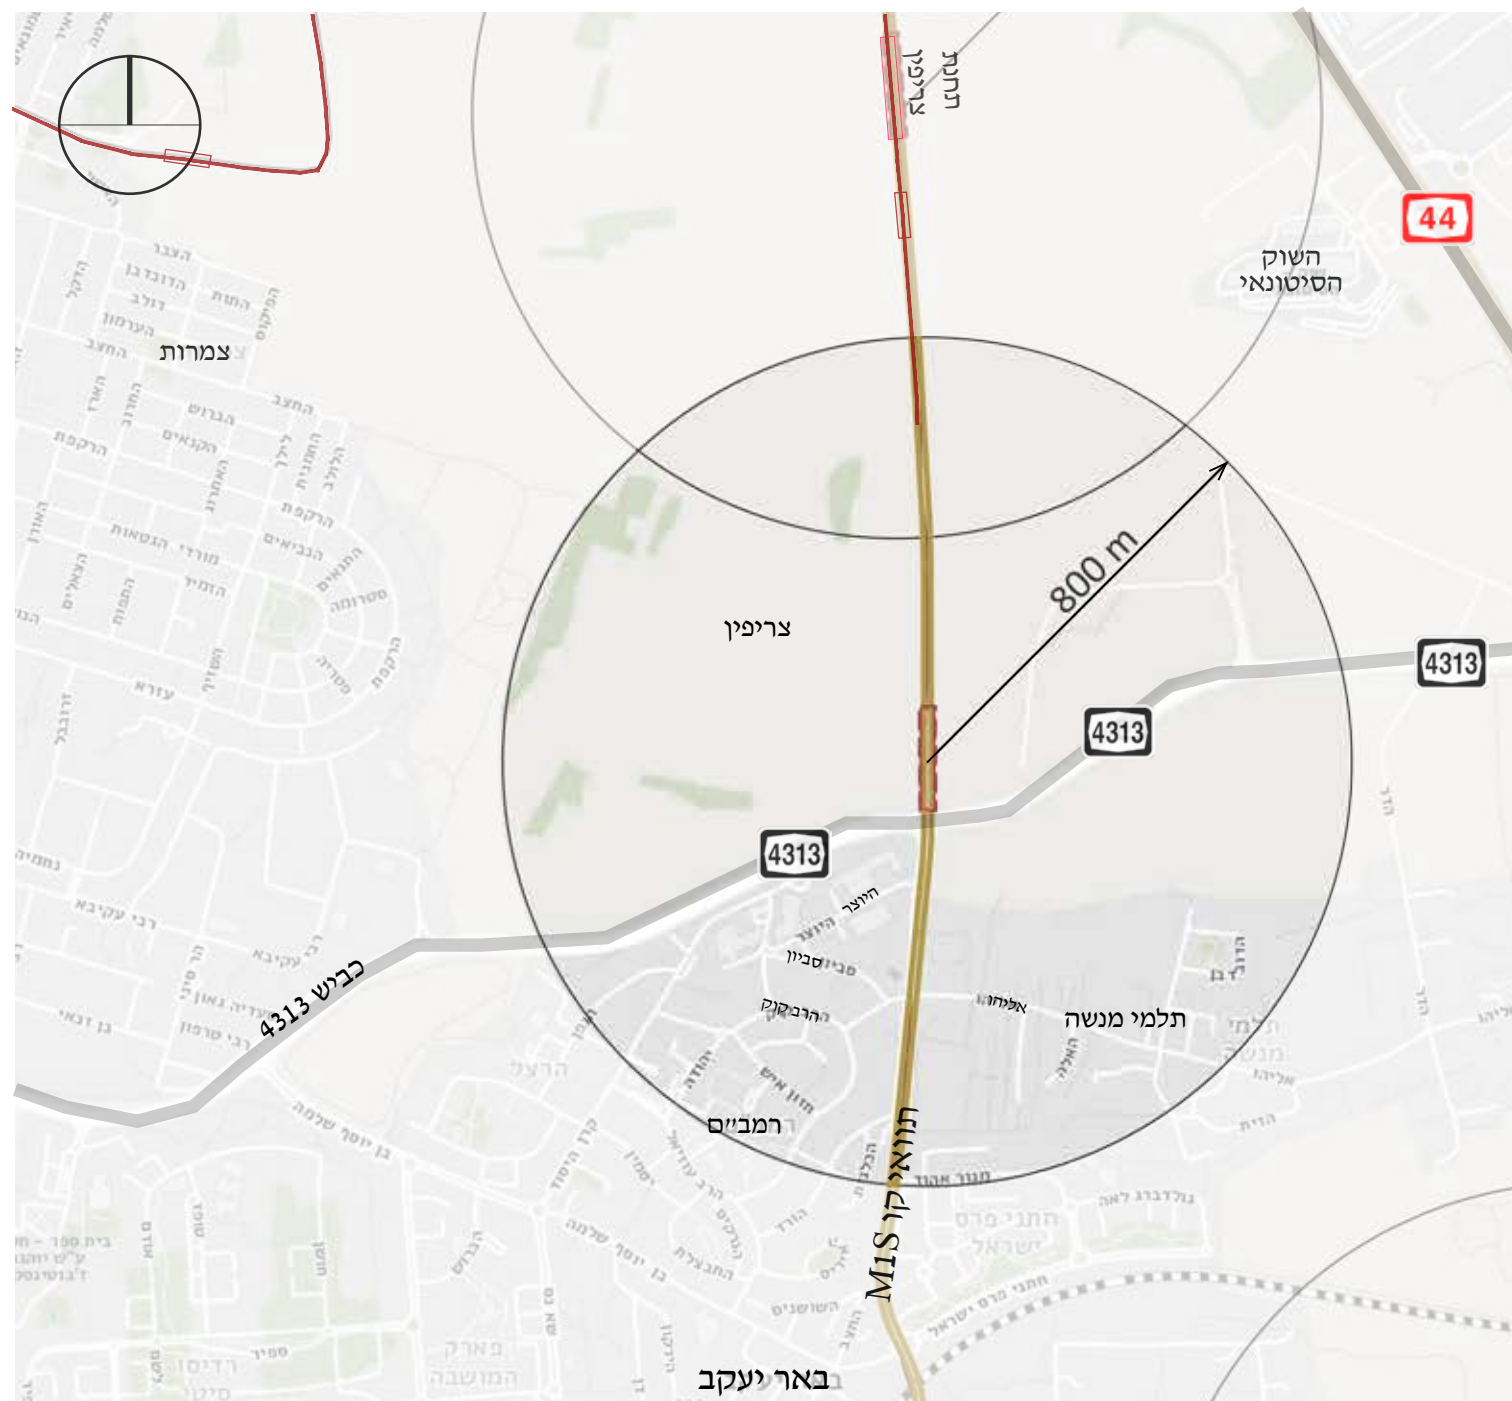

* שטח צבאי- לא ניתן לצלם